
日建学院


「１階平面兼配置プラン」を記入してください。（縮尺1／100）

(注)不正確な内容では、皆さんのプランを正しく評価できません。敷地、屋外施設、室名、柱、開口部、寸法等を正確に記入してください。

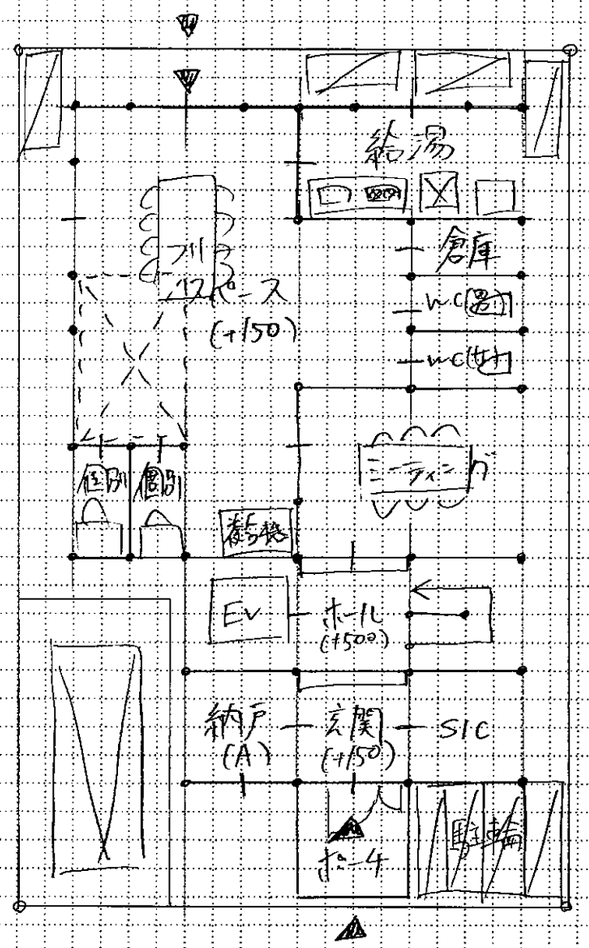

「２階平面プラン」を記入してください。（縮尺1／100）


(注)不正確な内容では、皆さんのプランを正しく評価できません。屋根、庇、室名、柱、開口部、寸法等を正確に記入してください。

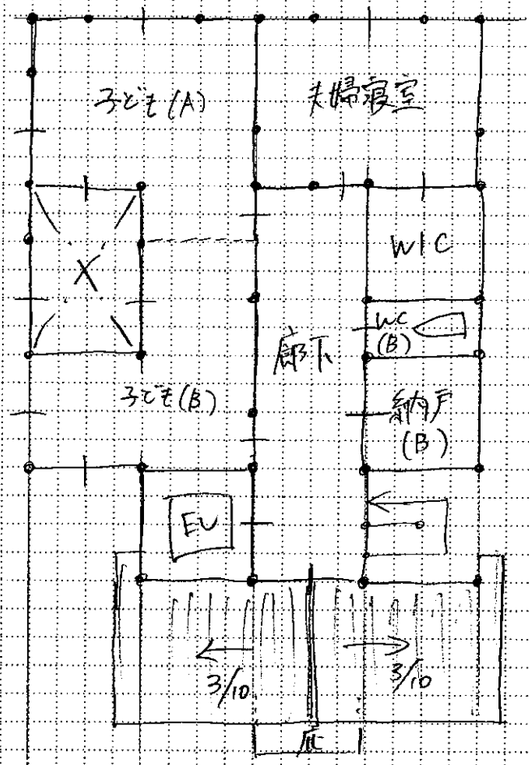

校名		学生番号	—	—	受験番号	—	氏名	道畑 佳希	

「３階平面プラン」を記入してください。（縮尺1／100）

（注）不正確な内容では、皆さんのプランを正しく評価できません。屋根、庇、室名、柱、開口部、寸法等を正確に記入してください。

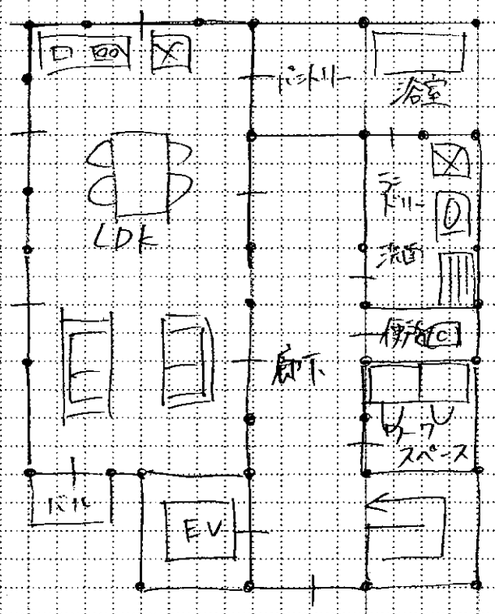

「計画の要点等の回答」を記入してください。

設問①：建物を北側道路にできる限り寄せて計画し道路側からの視認性を上げることで、気軽に利用できるよう配慮した。また3階にバルコニーは南側に設けることで、商店側から洗濯物が見えないようプライバシーに配慮した。

設問②：隣接する子ども室(A)と子ども室(B)の間に吹抜けを設けることで、将来ワーキングスペース部分として活用する際も、開放感や一体感が感じられるよう工夫した。

設問③：外壁にはガルバリウム鋼板小波を使用し、建物を準耐火構造とした。また、延焼のおそれのある部分にある外壁の開口部に防火設備を設けた。

「面積表」を記入してください。（※印は出題された場合に記入してください）

敷地面積			126	㎡
建築面積		(計算式) (7.28×7.28)+(5.46×3.64)	72.87	㎡
床面積	1階	(計算式) (7.28×7.28)+(5.46×3.64)	72.87	㎡
	2階	(計算式) (7.28×7.28)+(5.46×1.82)-(2.73×1.82)	57.96	㎡
	3階	(計算式) (7.28×7.28)+(5.46×1.82)	62.93	㎡
延べ面積			193.76	㎡
※建蔽率		建築面積 72.87 ／ 敷地面積 126 ㎡	57.83	%
※容積率		延べ面積 193.76 ／ 敷地面積 126 ㎡	153.77	%

「作業時間・見直しの有無など」を記入してください。

プランニング	70 分	プラン完成後の見直し	☑した ☐していない
記述・面積表	20 分	作業に要した時間は普段と比べてどうでしたか？	☐短い ☑同じ ☐長い
平面図	90 分	作業に要した時間は普段と比べてどうでしたか？	☐短い ☐同じ ☑長い
立面図	20 分	作業に要した時間は普段と比べてどうでしたか？	☐短い ☑同じ ☐長い
伏　図	20 分	作業に要した時間は普段と比べてどうでしたか？	☐短い ☑同じ ☐長い
部分詳細図	20 分	作業に要した時間は普段と比べてどうでしたか？	☐短い ☑同じ ☐長い
見直し・仕上げ	60 分	答案完成後の見直し	☑した ☐していない

「本試験を受験して気になる事」を記入してください。（例：○○の意味が分からなかった。）


・吹抜けを子ども室(A)と子ども室(B)の両方に隣接こでちゃったこと、
・ワーキング駐輪
・バルコニー
・面積計算ミスないか

講師記入欄

氏名 道畑 佳希


「１階平面兼配置プラン」を記入してください。（縮尺1／100）

（注）不正確な内容では、皆さんのプランを正しく評価できません。敷地、屋外施設、室名、柱、開口部、寸法等を正確に記入してください。

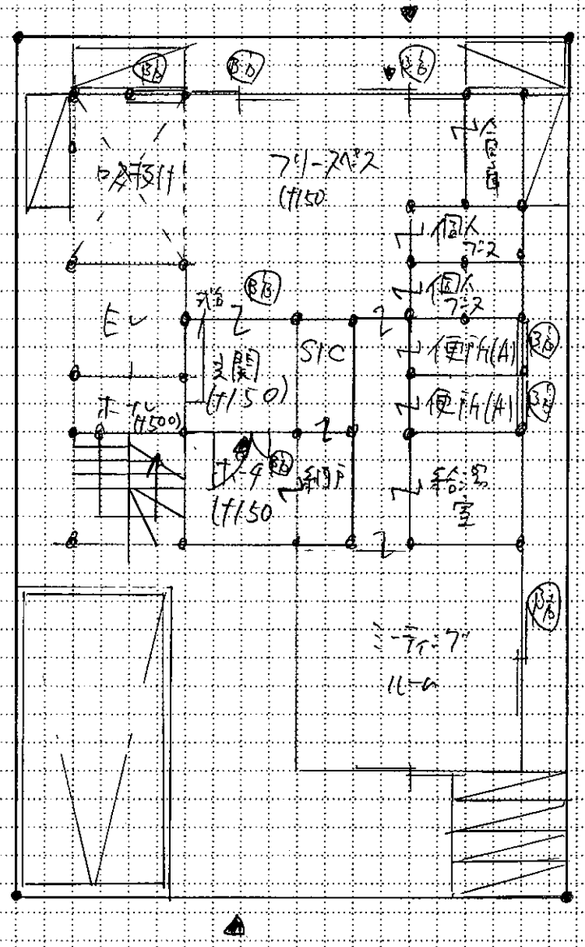

「２階平面プラン」を記入してください。（縮尺1／100）

（注）不正確な内容では、皆さんのプランを正しく評価できません。屋根、庇、室名、柱、開口部、寸法等を正確に記入してください。

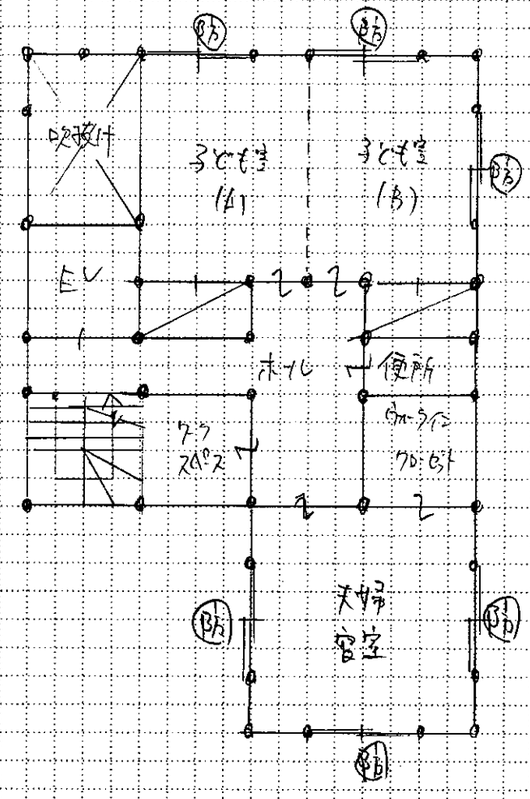


※2階は製図で全て延焼のおそれのお範囲内

校名		学生番号	－	－	受験番号	－	氏名	奥田 実佳	

「３階平面プラン」を記入してください。（縮尺1／100）

（注）不正確な内容では、皆さんのプランを正しく評価できません。屋根、庇、室名、柱、開口部、寸法等を正確に記入してください。

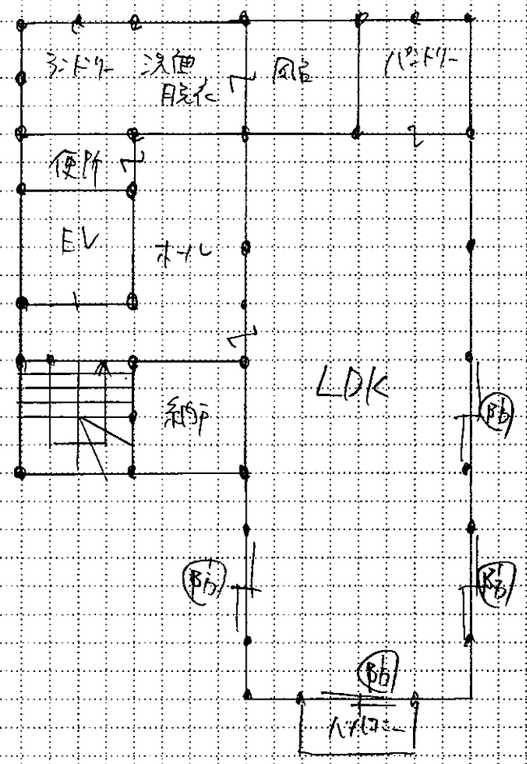

※ 3階は敷地全面可建築のおそれのある範囲内

氏名　奥田 真佐

「計画の要点等の回答」を記入してください。

設問①：コワーキングスペースを北側に面して配置しなるべく直結との離隔を小さくすることで集客性に配慮した。また、住宅部分は南側に面して配置し道路からなるべく離して配置することでセキュリティやプライバシーに配慮する工夫をした。

設問②：将来コワーキングスペースとして使用するのを考慮し、北側に面して配置することで商店街からの集客性に配慮した。また吹抜けを子ども室に隣接して配置することで採光に配慮し、より心地良い空間にする工夫をした。

設問③：主要構造部を一定の耐火性能を持つ準耐火建築物とした。

「面積表」を記入してください。（※印は出題された場合に記入してください）

敷地面積		126.00 ㎡	
建築面積		(計算式) (7.28×7.28)+(3.64×3.64)	66.39 ㎡
床面積	1階	(計算式) (7.28×7.28)+(3.64×3.64)−(1.82×1.82)	62.93 ㎡
	2階	(計算式) (7.28×7.28)+(3.64×3.64)−(1.82×2.28)	61.27 ㎡
	3階	(計算式) (7.28×7.28)+(3.64×3.64)	66.29 ㎡
延べ面積			190.44 ㎡
※建蔽率		建築面積 ／ 敷地面積 ㎡	%
※容積率		延べ面積 ／ 敷地面積 ㎡	%

「作業時間・見直しの有無など」を記入してください。

プランニング	60 分	プラン完成後の見直し ☑した □していない
記述・面積表	15 分	作業に要した時間は普段と比べてどうでしたか？ ☑短い □同じ □長い
平面図	80 分	作業に要した時間は普段と比べてどうでしたか？ ☑短い □同じ □長い
立面図	20 分	作業に要した時間は普段と比べてどうでしたか？ □短い ☑同じ □長い
伏　図	20 分	作業に要した時間は普段と比べてどうでしたか？ □短い ☑同じ □長い
部分詳細図	20 分	作業に要した時間は普段と比べてどうでしたか？ □短い ☑同じ □長い
見直し・仕上げ	85 分	答案完成後の見直し ☑した □していない

「本試験を受験して気になる事」を記入してください。（例：○○の意味が分からなかった。）


最初まで壁の両方を吹抜けと隣接して計画してた。

講師記入欄

下


「１階平面兼配置プラン」を記入してください。（縮尺1／100）

（注）不正確な内容では、皆さんのプランを正しく評価できません。敷地、屋外施設、室名、柱、開口部、寸法等を正確に記入してください。

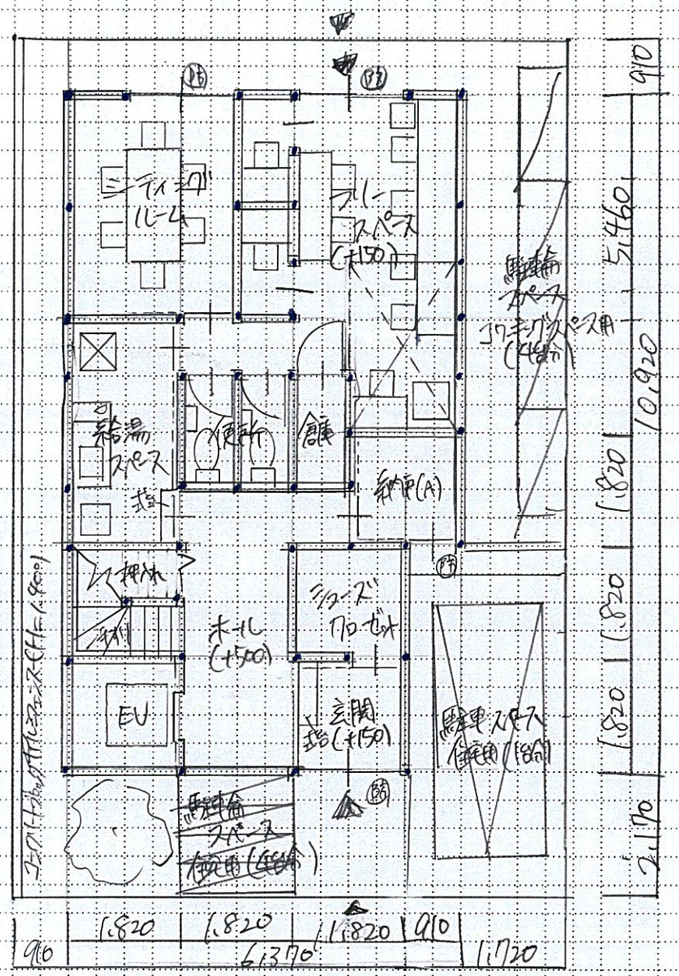

「２階平面プラン」を記入してください。（縮尺1／100）

（注）不正確な内容では、皆さんのプランを正しく評価できません。屋根、庇、室名、柱、開口部、寸法等を正確に記入してください。

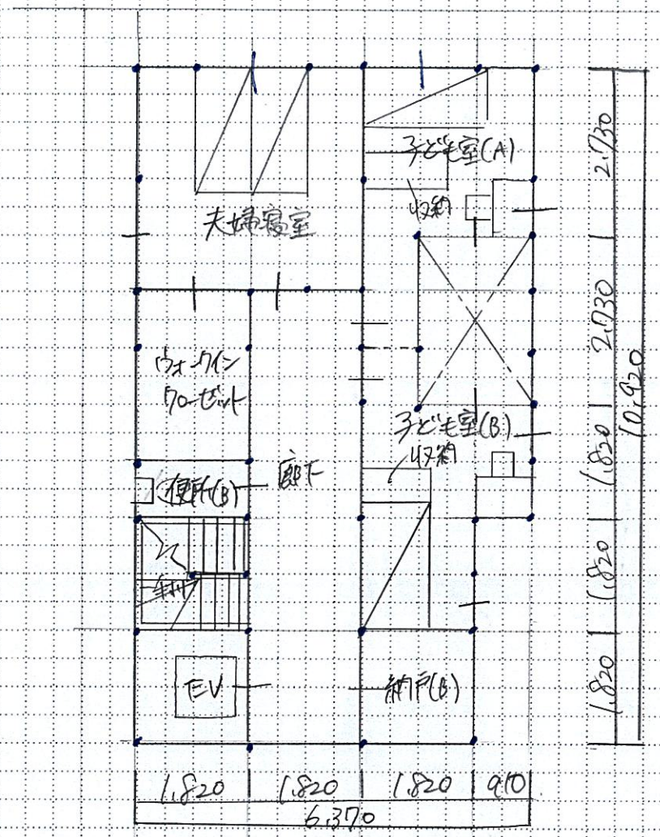


校名	池袋	学生番号	－ －	受験番号	2F－119324	氏名	高林日向子

２０２６年度 ２級建築士 プラン復元用紙 〔2/2〕（本試験プランを丁寧に記入しましょう。）

日建学院

「３階平面プラン」を記入してください。（縮尺1／100）

(注)不正確な内容では、皆さんのプランを正しく評価できません。屋根、庇、室名、柱、開口部、寸法等を正確に記入してください。

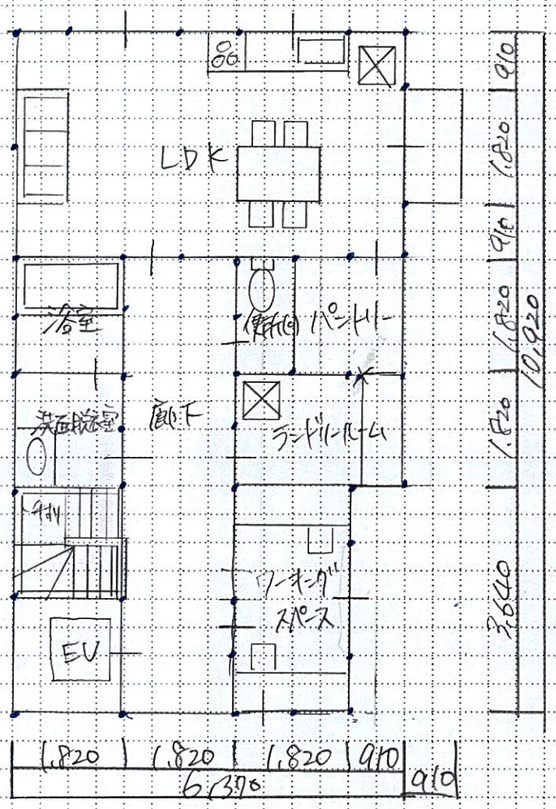

「計画の要点等の回答」を記入してください。

設問①：建物をなるべく北側道路に寄せ、利用者が気軽に入りやすいように工夫した。2階の北側はコワーキングスペース部分、南側は住宅部分と明確にわけることでプライバシーを確保した。

設問②：子ども室(A)と子ども室(B)の間に吹抜けを配置することで、将来1つの部屋として使用するときに、部屋の内部から1階の様子をながめることができるようにした

設問③：通常の火災において延焼を抑制するために必要とされる政令で定める技術的基準に適合した性能をもつ構造とした

「面積表」を記入してください。（※印は出題された場合に記入してください）

敷地面積		126	㎡
建築面積	(計算式) 7.28×6.37+3.64×5.46	66.24	㎡
床面積 1階	(計算式) 7.28×6.37+3.64×5.46	66.24	㎡
床面積 2階	(計算式) 7.28×6.37+3.64×5.46−1.82×2.73	61.27	㎡
床面積 3階	(計算式) 7.28×6.37+3.64×5.46	66.24	㎡
延べ面積		193.75	㎡
※建蔽率	建築面積 66.24 ／ 敷地面積 126 ㎡	52	%
※容積率	延べ面積 193.75 ／ 敷地面積 126 ㎡	153	%

「作業時間・見直しの有無など」を記入してください。

プランニング	80 分	プラン完成後の見直し ☑した ☐していない
記述・面積表	20 分	作業に要した時間は普段と比べてどうでしたか？ ☐短い ☐同じ ☐長い
平面図	130 分	作業に要した時間は普段と比べてどうでしたか？ ☑短い ☐同じ ☐長い
立面図	20 分	作業に要した時間は普段と比べてどうでしたか？ ☐短い ☑同じ ☐長い
伏　図	20 分	作業に要した時間は普段と比べてどうでしたか？ ☐短い ☑同じ ☐長い
部分詳細図	30 分	作業に要した時間は普段と比べてどうでしたか？ ☐短い ☐同じ ☑長い
見直し・仕上げ	0 分	答案完成後の見直し ☐した ☑していない

300分

「本試験を受験して気になる事」を記入してください。（例：○○の意味が分からなかった。）

部分詳細図があまり自信がない。
子ども室の形がいびつになってしまった。


講師記入欄

氏名 高林 日向子

日建学院


「１階平面兼配置プラン」を記入してください。（縮尺1／100）

(注) 不正確な内容では、皆さんのプランを正しく評価できません。敷地、屋外施設、室名、柱、開口部、寸法等を正確に記入してください。

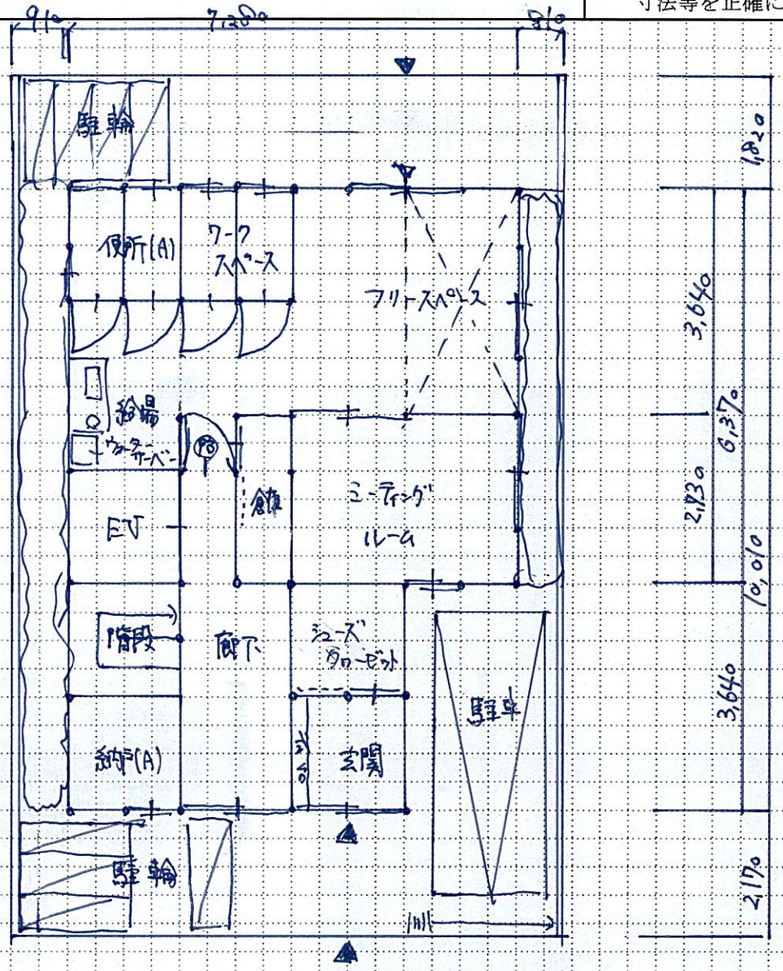

「２階平面プラン」を記入してください。（縮尺1／100）

(注) 不正確な内容では、皆さんのプランを正しく評価できません。屋根、庇、室名、柱、開口部、寸法等を正確に記入してください。

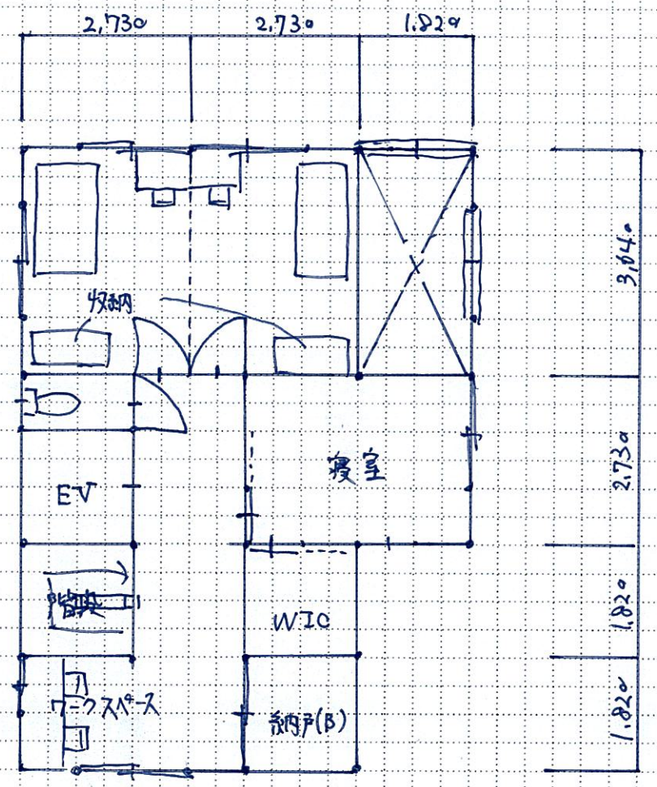


校名	池袋	学生番号	02800 − 0013 − 0402	受験番号	2F − 20832N	氏名	西上友哉	

２０２６年度 ２級建築士 プラン復元用紙 〔2/2〕（本試験プランを丁寧に記入しましょう。）

日建学院

「３階平面プラン」を記入してください。（縮尺1／100）

(注)不正確な内容では、皆さんのプランを正しく評価できません。屋根、庇、室名、柱、開口部、寸法等を正確に記入してください。

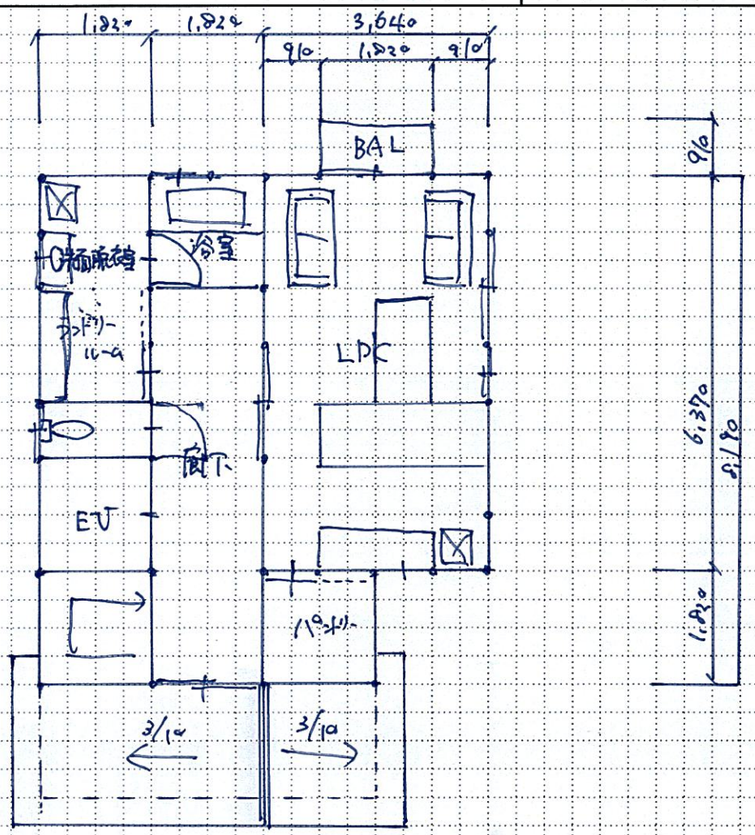

「計画の要点等の回答」を記入してください。

設問①：コワーキングスペース部分を、なるべく北面の道路に近接させることで、通行人の目に留まり中の様子がうかがえるような設計とした。また、将来的なうち宅のコワーキングスペースとしての利用を考慮し、2階には日中に利用することの少ないプライベートな部屋を配置するよう工夫した。

設問②：子ども室について、将来的に利用しやすいよう、間仕切壁を取外した時に、部屋が整形になるよう工夫した。また吹抜けを東面に配置することで、将来的に東面と西面から採光が得られ、一日中安定した明るさを確保することができるように配慮した。

設問③：準耐火構造となるように窓、外壁など適切な材をそれぞれ用いた。またコワーキングスペース部分を住宅部分の間は防火仕様の扉で区切ることで、火災時に火や煙が短時間で広がるのを防ぐことができるように工夫した。

「面積表」を記入してください。（※印は出題された場合に記入してください）

敷地面積		126 m²		
建築面積	(計算式) (7.28×6.37)+(5.46×3.64)	66.24 m²		
床面積 1階	(計算式) (7.28×6.37)+(5.46×3.64)	66.24 m²		
床面積 2階	(計算式) (7.28×6.37)+(5.46×3.64)-(1.82×3.64)	59.62 m²		
床面積 3階	(計算式) (7.28×6.37)+(5.46×1.82)	56.31 m²		
延べ面積	182.17 m²			
※建蔽率	建築面積 66.24 ／ 敷地面積 126 m²	52.5 %		
※容積率	延べ面積 182.17 ／ 敷地面積 126 m²	144.5 %		

「作業時間・見直しの有無など」を記入してください。

プランニング	90 分	プラン完成後の見直し	☑した ☐していない
記述・面積表	15 分	作業に要した時間は普段と比べてどうでしたか？	☐短い ☑同じ ☐長い
平面図	100 分	作業に要した時間は普段と比べてどうでしたか？	☑短い ☐同じ ☐長い
立面図	30 分	作業に要した時間は普段と比べてどうでしたか？	☐短い ☑同じ ☐長い
伏　図	25 分	作業に要した時間は普段と比べてどうでしたか？	☐短い ☑同じ ☐長い
部分詳細図	30 分	作業に要した時間は普段と比べてどうでしたか？	☐短い ☐同じ ☑長い
見直し・仕上げ	10 分	答案完成後の見直し	☑した ☐していない

「本試験を受験して気になる事」を記入してください。（例：○○の意味が分からなかった。）


部分詳細図がいまいち何の記述をおめられているのか分かりにくかった。
終了ギリギリで火打梁を入れていないことに気づき、フリーハンドで記入となってしまった。
エレベーター幅800を書き忘れてしまった。
その他は一通り描き上げました。

講師記入欄

氏名 邑上 友哉


「１階平面兼配置プラン」を記入してください。（縮尺1／100）

(注)不正確な内容では、皆さんのプランを正しく評価できません。敷地、屋外施設、室名、柱、開口部、寸法等を正確に記入してください。

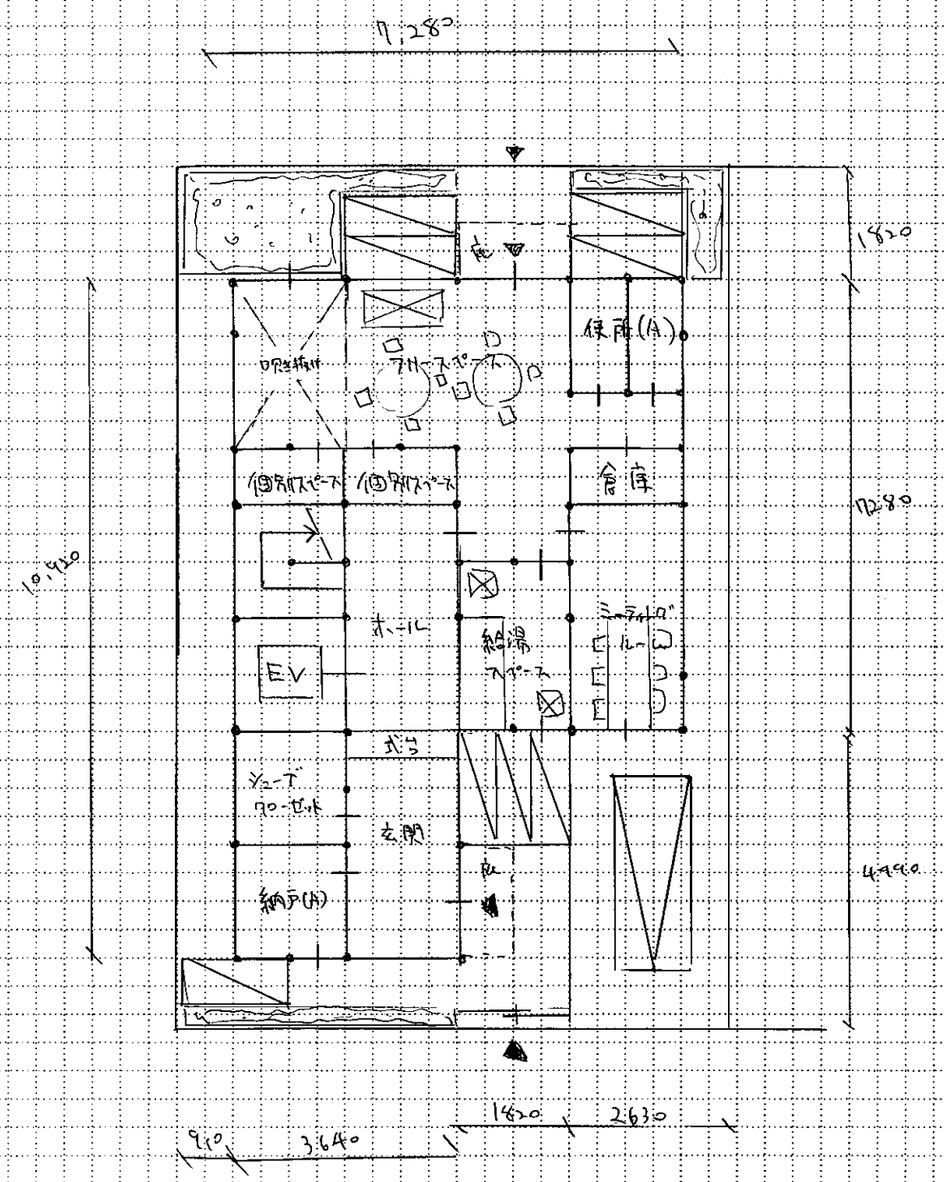

「２階平面プラン」を記入してください。（縮尺1／100）

(注)不正確な内容では、皆さんのプランを正しく評価できません。屋根、庇、室名、柱、開口部、寸法等を正確に記入してください。

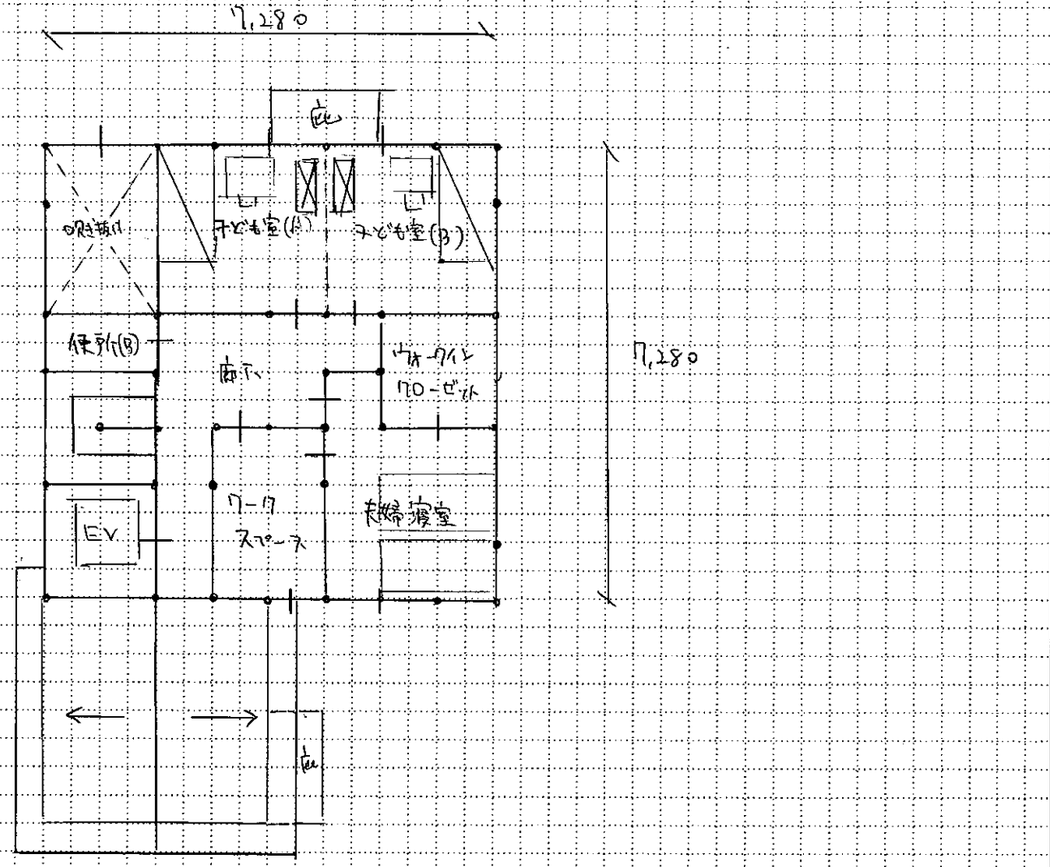


校名	池袋校	学生番号	02800 － 0013 － 0408	受験番号	－	氏名	松田 大輝	(4)

２０２６年度 ２級建築士 プラン復元用紙 〔2/2〕（本試験プランを丁寧に記入しましょう。）

日建学院

「３階平面プラン」を記入してください。（縮尺1／100）

(注)不正確な内容では、皆さんのプランを正しく評価できません。屋根、庇、室名、柱、開口部、寸法等を正確に記入してください。

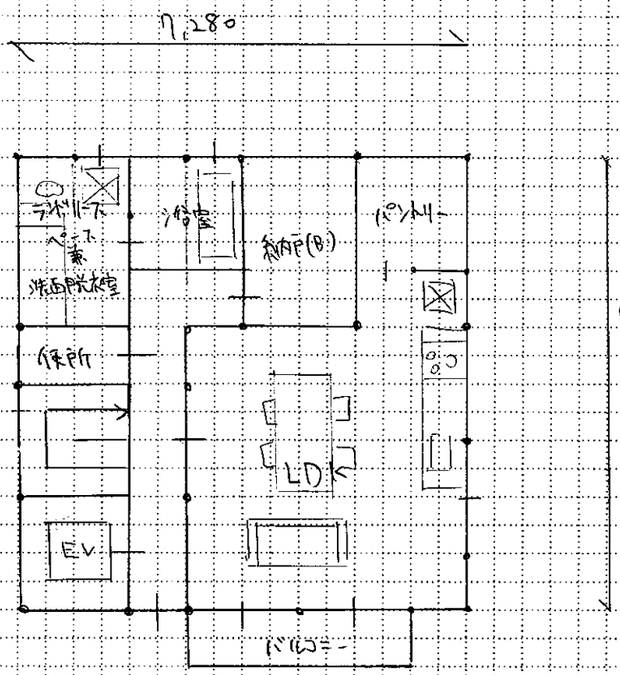

「計画の要点等の回答」を記入してください。

設問①：・フリースペースを北側（商店街側）に配置し、中の様子を伺えるようにした。
・住宅部分との扉は奥まった所に配置し、なるべく動線が被らないようにした。

設問②：・子ども室を商店街側及びフリースペース上部に計画することで、将来コワーキングスペースとした時に明確に切り離せるようにした。
・吹き抜けに階段をつくれるスペースを設け、将来使いやすい動線とした。

設問③：・外壁、天井、壁、軒裏など、一定時間火災に耐えうる材料とし、耐火被覆をした。
・異種用途部分の扉を防火設備とした。

「面積表」を記入してください。（※印は出題された場合に記入してください）

敷地面積		126.00 ㎡	
建築面積	(計算式) (7.28×7.28)+(3.64×3.64)	66.24 ㎡	
床面積 1階	(計算式) (7.28×7.28)+(3.64×3.64)	66.24 ㎡	
床面積 2階	(計算式) (7.28×7.28)−(1.82×2.73)	48.02 ㎡	
床面積 3階	(計算式) 7.28×7.28	52.98 ㎡	
延べ面積		167.24 ㎡	
※建蔽率	建築面積 66.24 ／ 敷地面積 126 ㎡	52 %	
※容積率	延べ面積 167.24 ／ 敷地面積 126 ㎡	132 %	

「作業時間・見直しの有無など」を記入してください。

プランニング	80 分	プラン完成後の見直し ☑した ☐していない
記述・面積表	15 分	作業に要した時間は普段と比べてどうでしたか？ ☐短い ☑同じ ☐長い
平面図	90 分	作業に要した時間は普段と比べてどうでしたか？ ☐短い ☑同じ ☐長い
立面図	15 分	作業に要した時間は普段と比べてどうでしたか？ ☐短い ☑同じ ☐長い
伏図	30 分	作業に要した時間は普段と比べてどうでしたか？ ☐短い ☑同じ ☐長い
部分詳細図	20 分	作業に要した時間は普段と比べてどうでしたか？ ☐短い ☑同じ ☐長い
見直し・仕上げ	45 分	答案完成後の見直し ☑した ☐していない


「本試験を受験して気になる事」を記入してください。（例：○○の意味が分からなかった。）

講師記入欄

氏名 松田 大輝


「１階平面兼配置プラン」を記入してください。（縮尺1／100）

(注)不正確な内容では、皆さんのプランを正しく評価できません。敷地、屋外施設、室名、柱、開口部、寸法等を正確に記入してください。

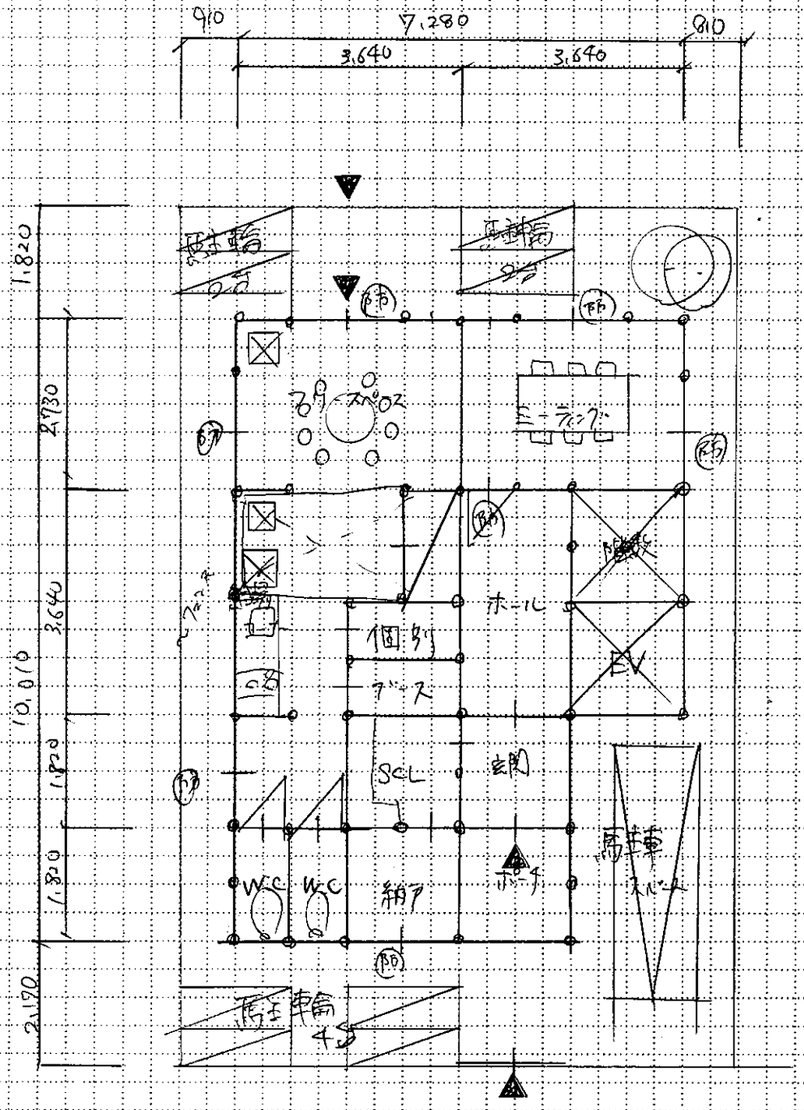

「２階平面プラン」を記入してください。（縮尺1／100）


(注)不正確な内容では、皆さんのプランを正しく評価できません。屋根、庇、室名、柱、開口部、寸法等を正確に記入してください。

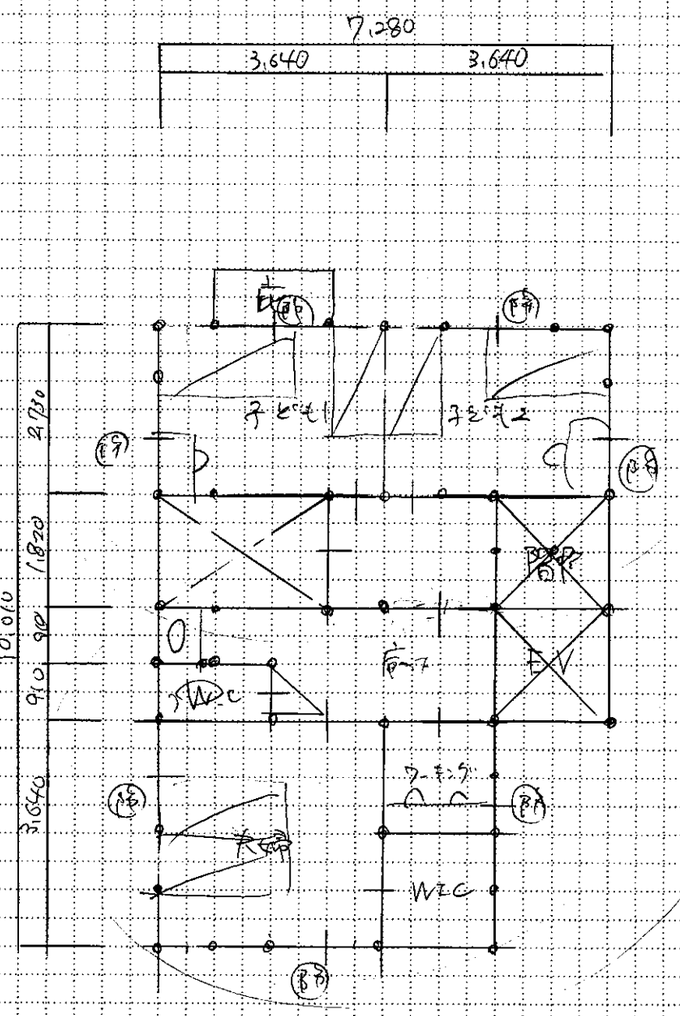

校名	池袋	学生番号	02800 － 00 －	受験番号	－	氏名	下田宿敏	(4)

「3階平面プラン」を記入してください。（縮尺1／100）

(注)不正確な内容では、皆さんのプランを正しく評価できません。屋根、庇、室名、柱、開口部、寸法等を正確に記入してください。

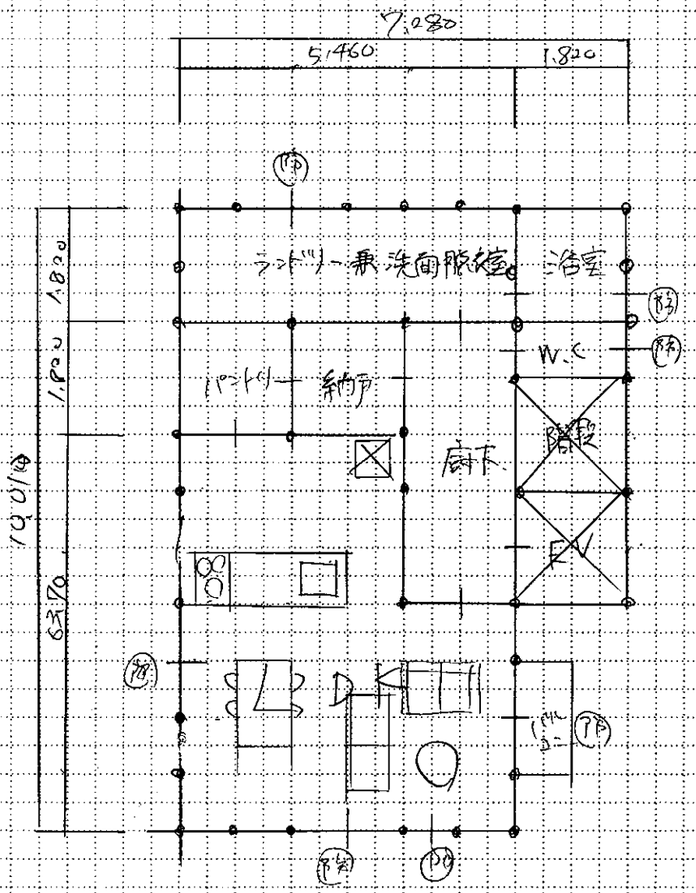

「計画の要点等の回答」を記入してください。

設問①：商店街のある北側にかうスを多用することで、人を多く取り入れるファサードデザインとした。また、住宅部分に門を設けることでプライバシーへの配慮をした。

設問②：吹き抜けを隣接させ、一体利用ができるようにした。廊下に扉を設けることで子ども室と吹き抜け空間を間仕切れるように配慮した。

設問③：準防火地域にある木造三階建てを建てるにあたり、主要構造部を耐火性能のある準耐火建築物とした。

「面積表」を記入してください。（※印は出題された場合に記入してください）

敷地面積			126.00	㎡
建築面積		(計算式) (7.28×6.37)+(3.64×5.46)	66.24	㎡
床面積	1階	(計算式) (7.28×6.37)+(3.64×5.46)-(1.82×1.82)	62.93	㎡
	2階	(計算式) (7.28×6.37)+(3.64×5.46)-(2.73×1.82)	61.27	㎡
	3階	(計算式) (7.28×6.37)+(3.64×5.46)	66.24	㎡
延べ面積			190.44	㎡
※建蔽率		建築面積 66.24 / 敷地面積 126. ㎡	52.57	%
※容積率		延べ面積 190.44 / 敷地面積 126.44 ㎡	150	%

「作業時間・見直しの有無など」を記入してください。

プランニング	80 分	プラン完成後の見直し	☑した ☐していない
記述・面積表	15 分	作業に要した時間は普段と比べてどうでしたか？	☐短い ☑同じ ☐長い
平面図	90 分	作業に要した時間は普段と比べてどうでしたか？	☐短い ☑同じ ☐長い
立面図	15 分	作業に要した時間は普段と比べてどうでしたか？	☐短い ☑同じ ☐長い
伏　図	30 分	作業に要した時間は普段と比べてどうでしたか？	☐短い ☑同じ ☐長い
部分詳細図	20 分	作業に要した時間は普段と比べてどうでしたか？	☐短い ☑同じ ☐長い
見直し・仕上げ	45 分	答案完成後の見直し	☑した ☐していない

「本試験を受験して気になる事」を記入してください。（例：○○の意味が分からなかった。）


~~設定~~ 伏せ図の矢印が、ここまで書いてあるが、文字ちもメモしまいました。

講師記入欄

氏名 下田空良


「１階平面兼配置プラン」を記入してください。（縮尺1／100）

(注)不正確な内容では、皆さんのプランを正しく評価できません。敷地、屋外施設、室名、柱、開口部、寸法等を正確に記入してください。

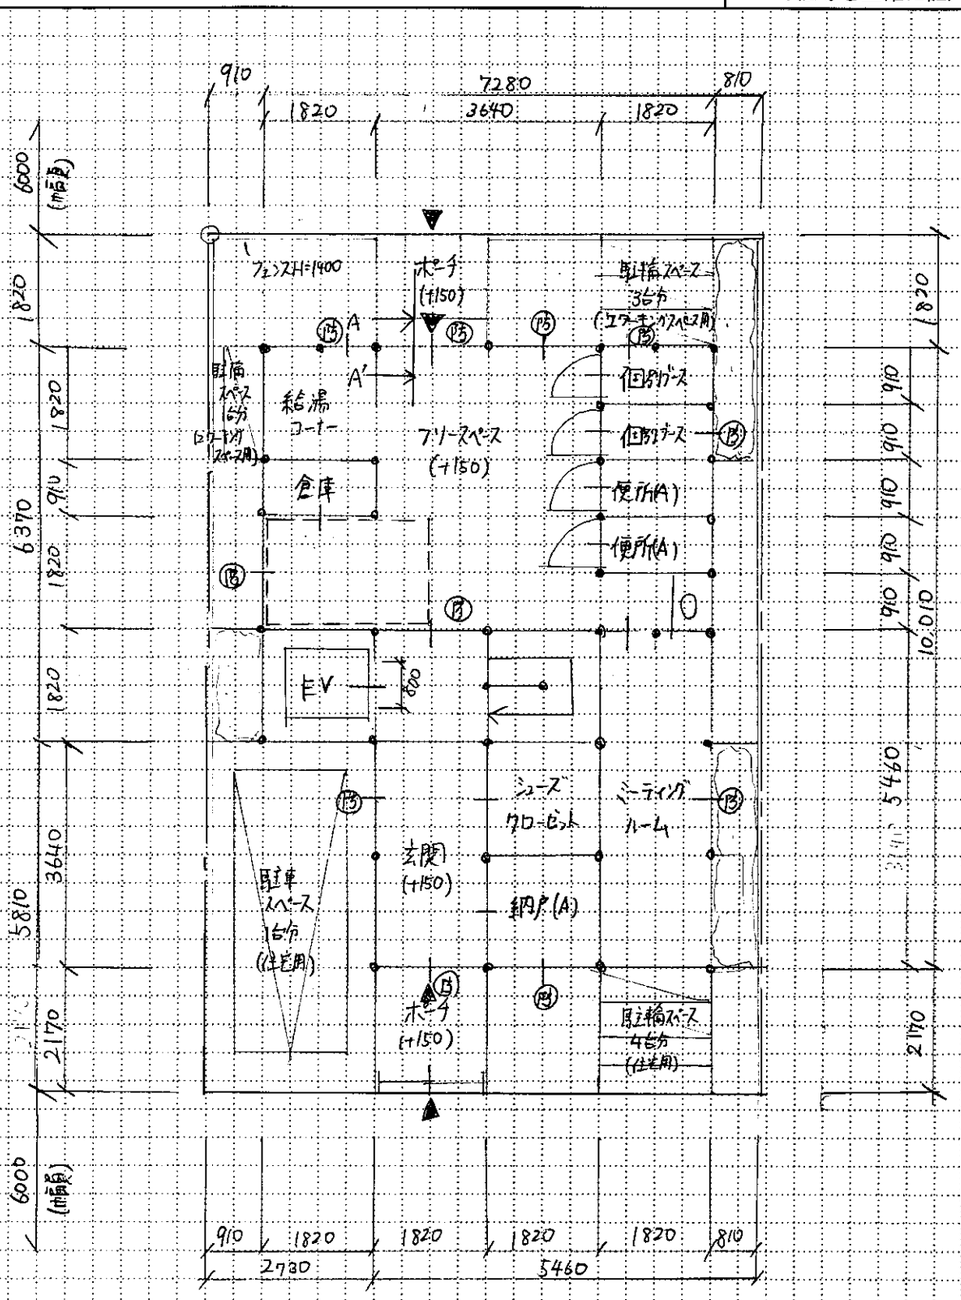

「２階平面プラン」を記入してください。（縮尺1／100）

(注)不正確な内容では、皆さんのプランを正しく評価できません。屋根、庇、室名、柱、開口部、寸法等を正確に記入してください。

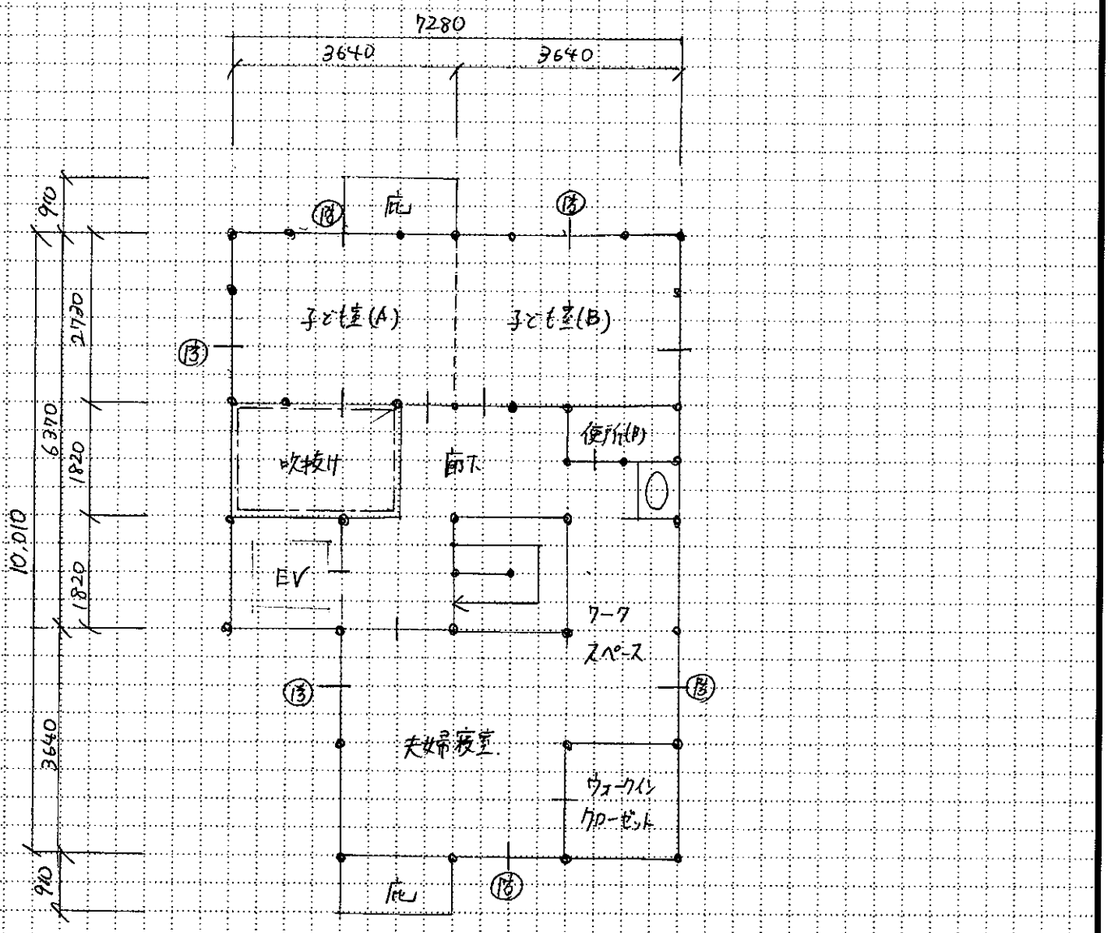


校名	池袋校	学生番号	02800 − 0010 − 0304	受験番号	2F − 15792N	氏名	藤井 遥

２０２６年度 ２級建築士 プラン復元用紙 〔2/2〕（本試験プランを丁寧に記入しましょう。）

日建学院

「３階平面プラン」を記入してください。（縮尺1／100）

(注)不正確な内容では、皆さんのプランを正しく評価できません。屋根、庇、室名、柱、開口部、寸法等を正確に記入してください。

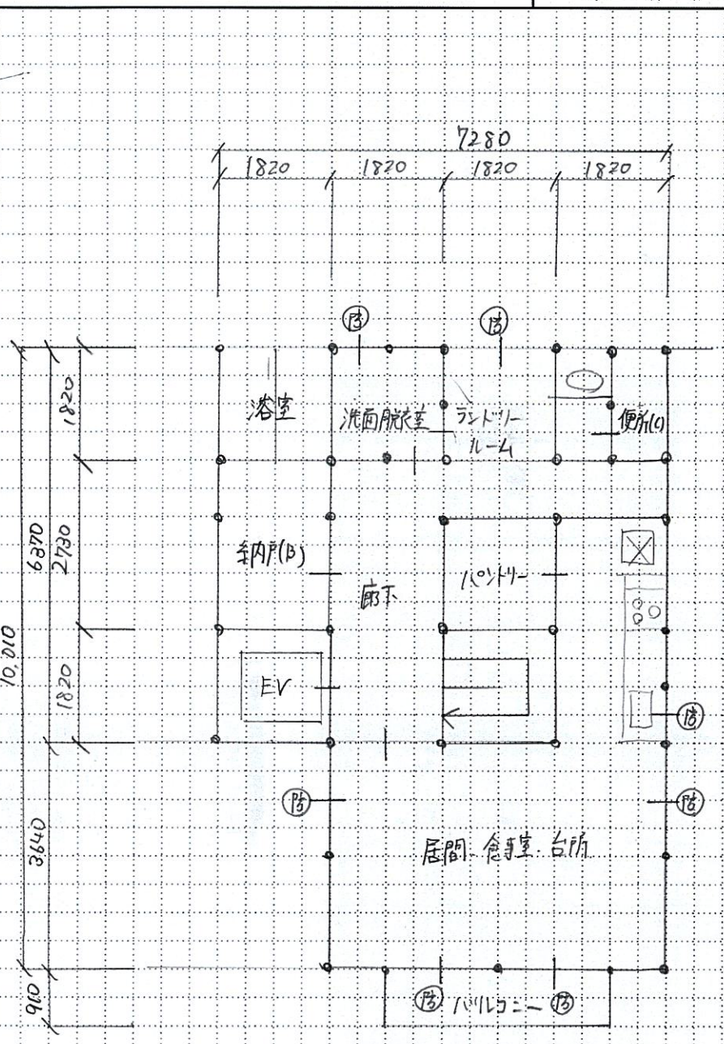

「計画の要点等の回答」を記入してください。

設問①：コワーキングスペース部分のアプローチを南庭のある北側道路に面して設けることで集客性に配慮した。また、北側道路に面してフリースペースを設けることで視認性に配慮した。住宅部分のアプローチには門を設け、エレベーター、階段等を奥に配置することでセキュリティ面の計画を工夫した。

設問②：将来、子ども室をコワーキングスペース部分として利用するにあたり、コワーキングスペース部分の上部に子ども室を配置し、子ども室(A)から、下階のフリースペースを見れるように工夫した。

設問③：主要な構造部を一定の耐火性能をもつ準耐火構造とした。また、コワーキングスペース部分と住宅部分を防火区画とし、開口部には防火設備等を用いた。

「面積表」を記入してください。（※印は出題された場合に記入してください）

敷地面積		126.00 ㎡	
建築面積	(計算式) (7.28×6.37)+(5.46×3.64)	66.24 ㎡	
床面積 1階	(計算式) (7.28×6.37)+(5.46×3.64)	66.24 ㎡	
床面積 2階	(計算式) (7.28×6.37)+(5.46×3.64)−(2.73×1.82)	61.27 ㎡	
床面積 3階	(計算式) (7.28×6.37)+(5.46×3.64)	66.24 ㎡	
延べ面積		193.75 ㎡	
※建蔽率	建築面積 66.24 ／ 敷地面積 126.00 ㎡	52 %	
※容積率	延べ面積 193.75 ／ 敷地面積 126.00 ㎡	153. %	

「作業時間・見直しの有無など」を記入してください。

プランニング	60 分	プラン完成後の見直し ☑した ☐していない
記述・面積表	30 分	作業に要した時間は普段と比べてどうでしたか？ ☐短い ☑同じ ☐長い
平面図	100 分	作業に要した時間は普段と比べてどうでしたか？ ☐短い ☑同じ ☐長い
立面図	15 分	作業に要した時間は普段と比べてどうでしたか？ ☐短い ☑同じ ☐長い
伏　図	20 分	作業に要した時間は普段と比べてどうでしたか？ ☐短い ☑同じ ☐長い
部分詳細図	15 分	作業に要した時間は普段と比べてどうでしたか？ ☐短い ☑同じ ☐長い
見直し・仕上げ	60 分	答案完成後の見直し ☑した ☐していない

「本試験を受験して気になる事」を記入してください。（例：○○の意味が分からなかった。）

ⓐ子ども室(A)と吹抜けを隣設した際、吹抜けが面する部分に窓を設けましたが、ここに防は必要でしょうか。

ⓐ「L・D・K」を「居間・食事室・台所」と名記してしまいましたが、これは失格になりますか。


L・D・Kを1室にまとめるとのことでしたが、L室は1室あっていいでしょうか。

講師記入欄

氏名 藤井 遥


「１階平面兼配置プラン」を記入してください。（縮尺1／100）

(注)不正確な内容では、皆さんのプランを正しく評価できません。敷地、屋外施設、室名、柱、開口部、寸法等を正確に記入してください。

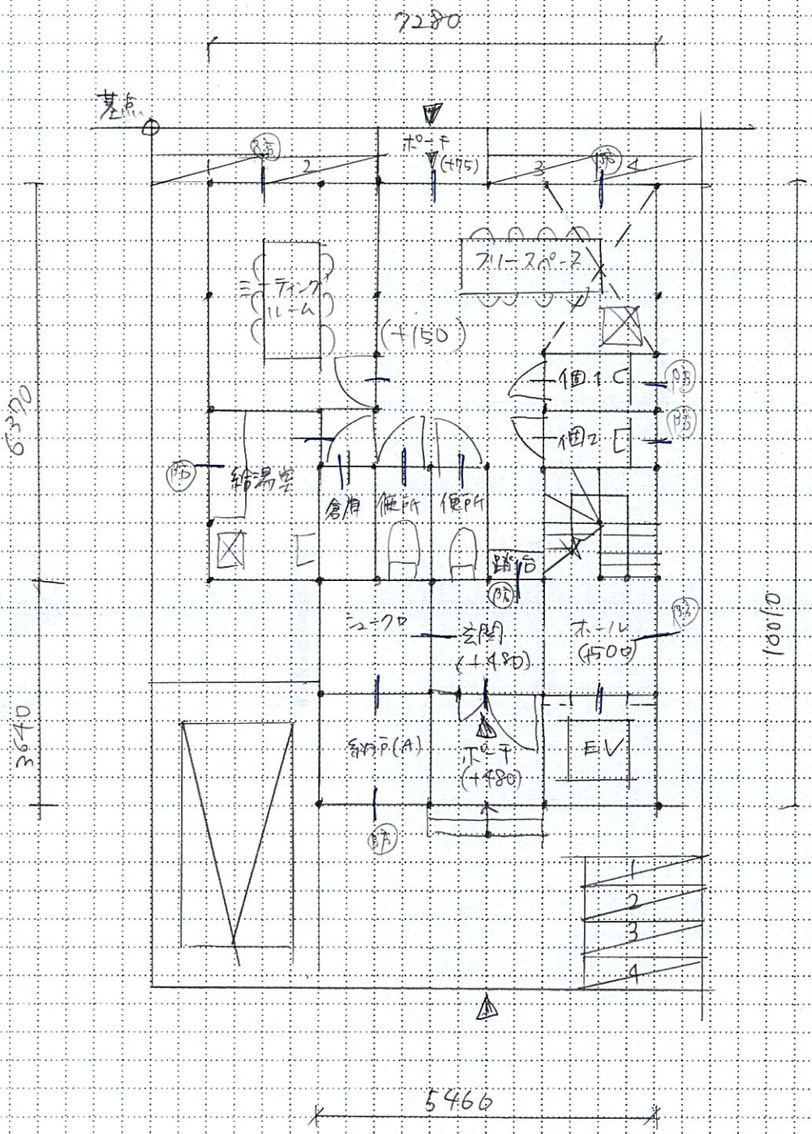

「２階平面プラン」を記入してください。（縮尺1／100）

(注)不正確な内容では、皆さんのプランを正しく評価できません。屋根、庇、室名、柱、開口部、寸法等を正確に記入してください。

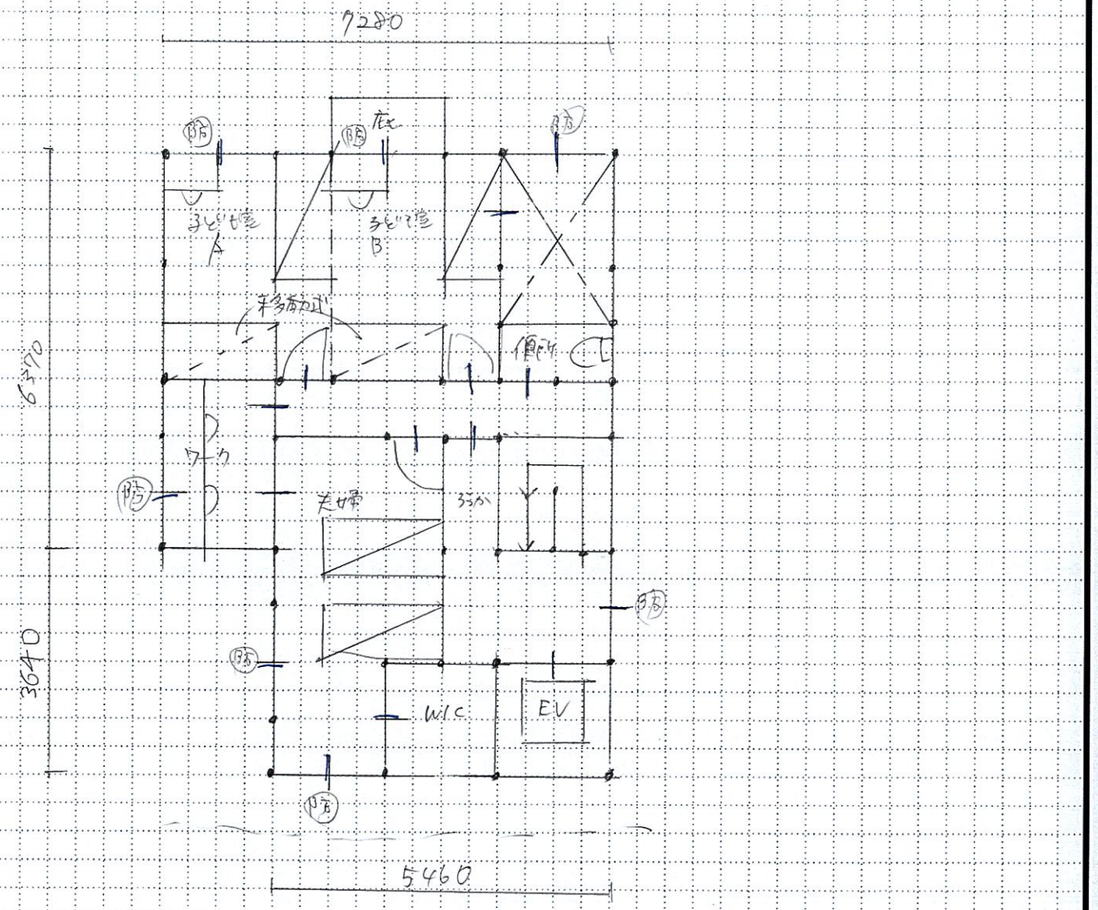


校名	池袋	学生番号	－	－	受験番号	－	氏名	柳 茉奈歩	(4)

２０２６年度 ２級建築士 プラン復元用紙 〔2/2〕（本試験プランを丁寧に記入しましょう。）

日建学院

「３階平面プラン」を記入してください。（縮尺1／100）

(注)不正確な内容では、皆さんのプランを正しく評価できません。屋根、庇、室名、柱、開口部、寸法等を正確に記入してください。

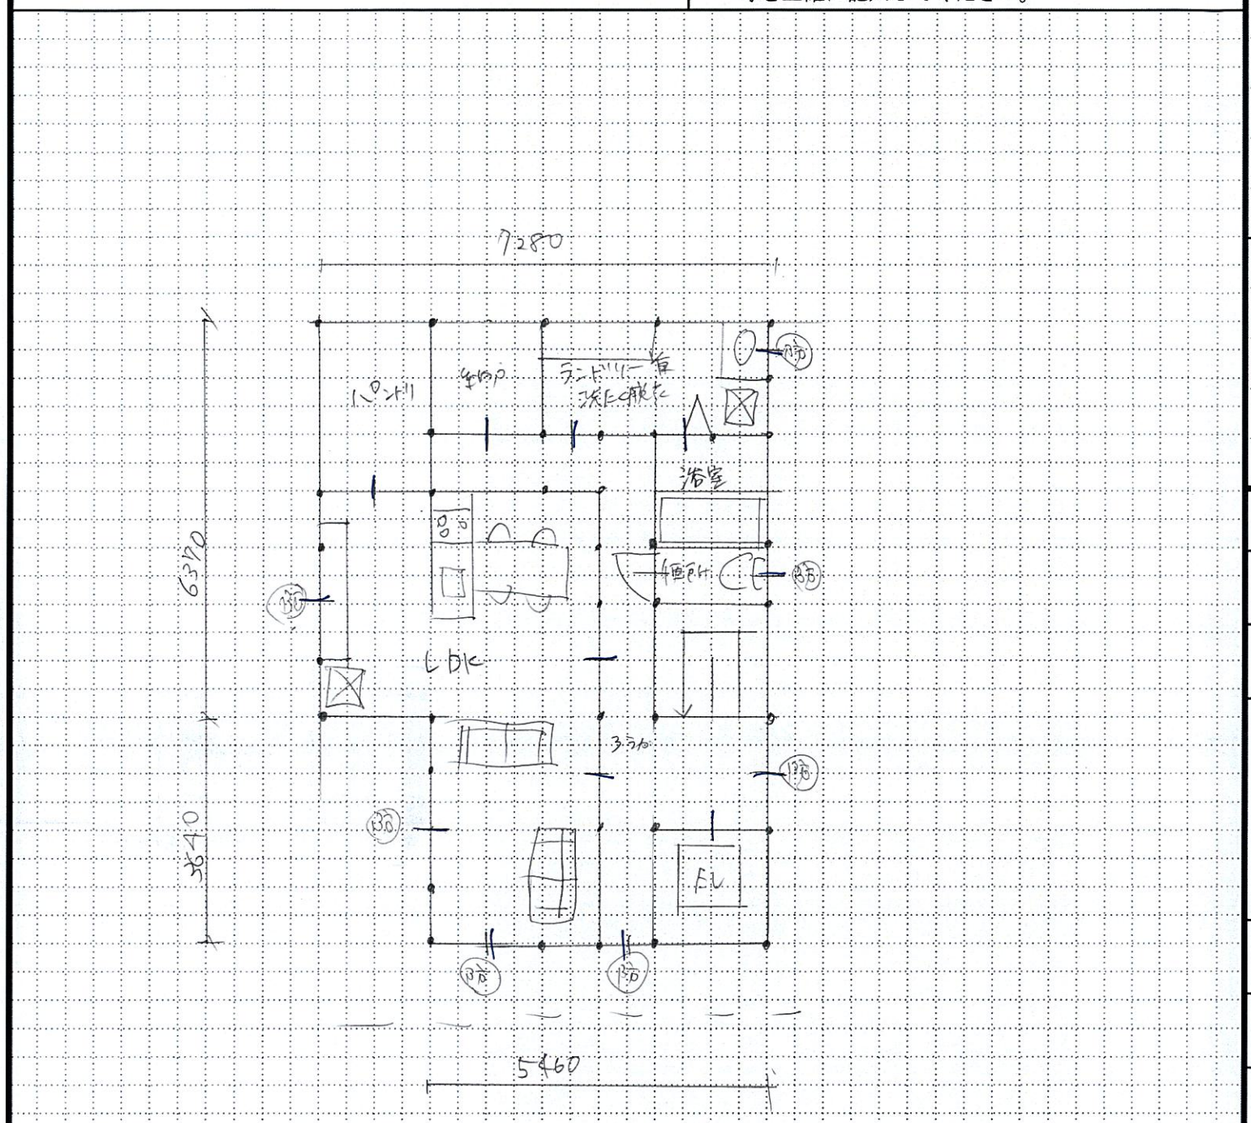

氏名 林 圭奈歩

「計画の要点等の回答」を記入してください。

設問①：商店街の北側に開口を多く設けることで、視認性を高め、気軽に利用できるように工夫した。また、住宅と店舗の間には扉をつけることで明確に分離し、セキュリティを確保した。

設問②：将来、1室として子ども室を利用できるように同じ大きさかつとなりに並べることを工夫した。1階には フリースペースとミーティングルームが大体同じ大きさになるように配置することで、構造的安定に期待する。

設問③：準耐火構造への配慮として、外壁にはガルバリウム鋼板を使用した。屋根は平スレート葺とすることで火に強い外回りにすることを工夫した。

「面積表」を記入してください。（※印は出題された場合に記入してください）

敷地面積		126.00 ㎡	
建築面積	(計算式) (7,28×6,37)+(3,64×5,46)	66.24 ㎡	
床面積	1階	(計算式) (7,28×6,37)+(3,64×5,46)−(1,82×1,82) ホール	62.93 ㎡
	2階	(計算式) (7,28×6,37)+(3,64×5,46)−(1,82×2,73) 吹抜け	61.27 ㎡
	3階	(計算式) (7,28×6,37)+(3,64×5,46)	66.24 ㎡
延べ面積		190.44 ㎡	
※建蔽率	建築面積 ／ 敷地面積 ㎡		%
※容積率	延べ面積 ／ 敷地面積 ㎡		%

「作業時間・見直しの有無など」を記入してください。

プランニング	90 分	プラン完成後の見直し ☑した □していない
記述・面積表	15 分	作業に要した時間は普段と比べてどうでしたか？ □短い ☑同じ □長い
平面図	1h20 分	作業に要した時間は普段と比べてどうでしたか？ □短い ☑同じ □長い
立面図	17 分	作業に要した時間は普段と比べてどうでしたか？ ☑短い □同じ □長い
伏　図	22 分	作業に要した時間は普段と比べてどうでしたか？ □短い ☑同じ □長い
部分詳細図	15 分	作業に要した時間は普段と比べてどうでしたか？ ☑短い □同じ □長い
見直し・仕上げ	60 分	答案完成後の見直し ☑した □していない

「本試験を受験して気になる事」を記入してください。（例：○○の意味が分からなかった。）

総延べ面積は何度も見直しました。
外形描き始めの本当は1820南にセットバックの予定が910に。
なんとか自転車をおさめ生した。

2Fワークスペースの採光し、㊱が多かったかもしれない。


敷地の③行き止まりは見にのが迷走しました。

講師記入欄

日建学院


「１階平面兼配置プラン」を記入してください。（縮尺1／100）

(注)不正確な内容では、皆さんのプランを正しく評価できません。敷地、屋外施設、室名、柱、開口部、寸法等を正確に記入してください。

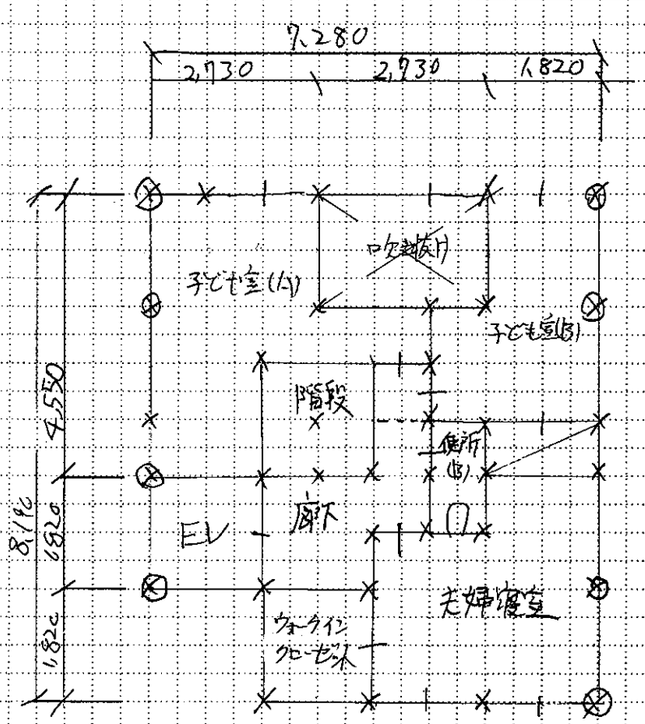

「２階平面プラン」を記入してください。（縮尺1／100）

(注)不正確な内容では、皆さんのプランを正しく評価できません。屋根、庇、室名、柱、開口部、寸法等を正確に記入してください。

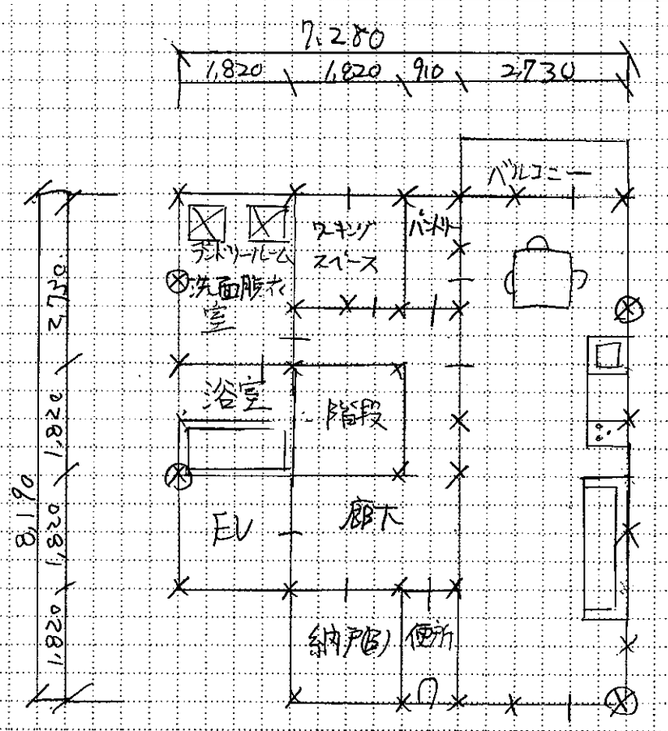


校名	池袋	学生番号	002800 - 0013 - 0407	受験番号	2F - 21868N	氏名	榎本 雄介	(4)

２０２６年度 ２級建築士 プラン復元用紙 〔2/2〕（本試験プランを丁寧に記入しましょう。）

日建学院

「３階平面プラン」を記入してください。（縮尺1／100）

(注)不正確な内容では、皆さんのプランを正しく評価できません。屋根、庇、室名、柱、開口部、寸法等を正確に記入してください。

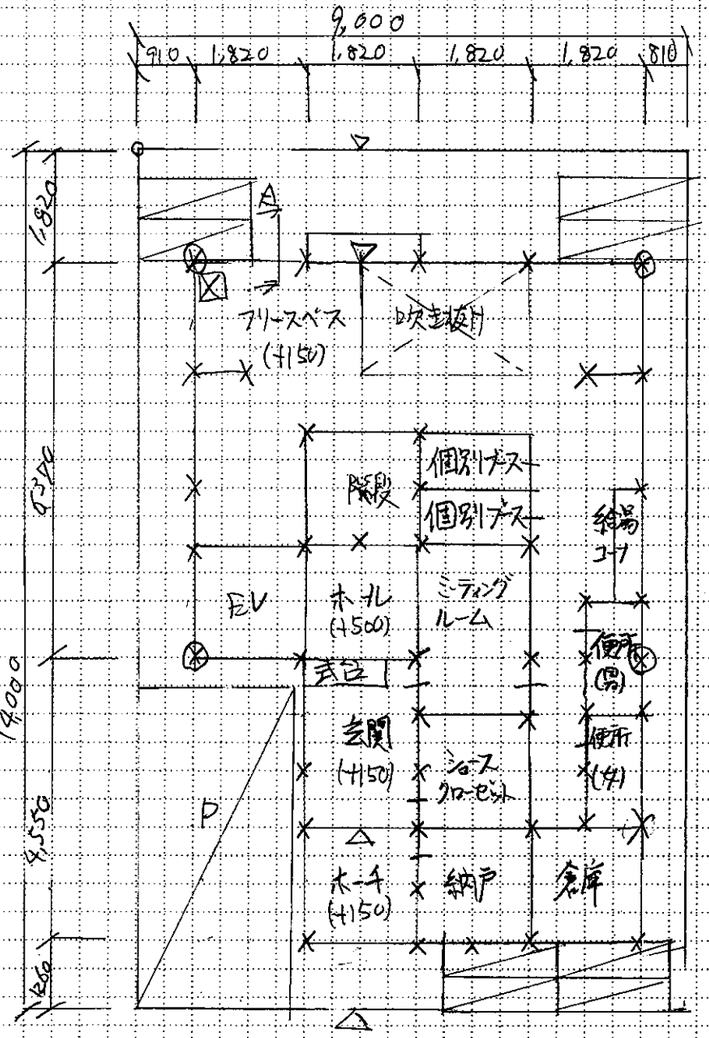

「計画の要点等の回答」を記入してください。

設問①：

店舗は、商店街に面している北側に最大限開口をとり、視認性を高め、入り易いつくりとし、住宅は南側玄関とし、動線がまじらない様にした。また、1Fの行き来きできる計画もミーティング室という異なった部屋とすることでセキュリティーを確保した。

設問②：

フリースペースの上部に吹き抜けを配置することで、部屋の採光をより多くとりいれると共に、将来2Fがコワーキングスペースになった時、上下で一体間が出る様に工夫した。

設問③：

準耐火構造に適合した建材を使用した。
また、準耐火構造に適合する様に耐力壁を上下左右バランスよく配置した。

「面積表」を記入してください。（※印は出題された場合に記入してください）

敷地面積		126 m²	
建築面積	(計算式) 7.28×10.92−4.55×1.82	71.21 m²	
床面積 1階	(計算式) 7.28×10.92−4.55×1.82−1.82×1.82	67.90 m²	
床面積 2階	(計算式) 7.28×8.19−1.82×1.82	56.31 m²	
床面積 3階	(計算式) 7.28×8.19−1.82×1.82	56.31 m²	
延べ面積		180.52 m²	
※建蔽率	建築面積 71.21 ／ 敷地面積 126 m²	56 %	
※容積率	延べ面積 180.52 ／ 敷地面積 126 m²	143 %	

「作業時間・見直しの有無など」を記入してください。

プランニング	75 分	プラン完成後の見直し ☑した □していない
記述・面積表	15 分	作業に要した時間は普段と比べてどうでしたか？ ☑短い □同じ □長い
平面図	140 分	作業に要した時間は普段と比べてどうでしたか？ □短い ☑同じ □長い
立面図	25 分	作業に要した時間は普段と比べてどうでしたか？ □短い ☑同じ □長い
伏図	30 分	作業に要した時間は普段と比べてどうでしたか？ □短い ☑同じ □長い
部分詳細図	25 分	作業に要した時間は普段と比べてどうでしたか？ □短い ☑同じ □長い
見直し・仕上げ	10 分	答案完成後の見直し ☑した □していない


「本試験を受験して気になる事」を記入してください。（例：○○の意味が分からなかった。）

講師記入欄

氏名 榎本 雄介


「１階平面兼配置プラン」を記入してください。（縮尺1／100）

(注)不正確な内容では、皆さんのプランを正しく評価できません。敷地、屋外施設、室名、柱、開口部、寸法等を正確に記入してください。

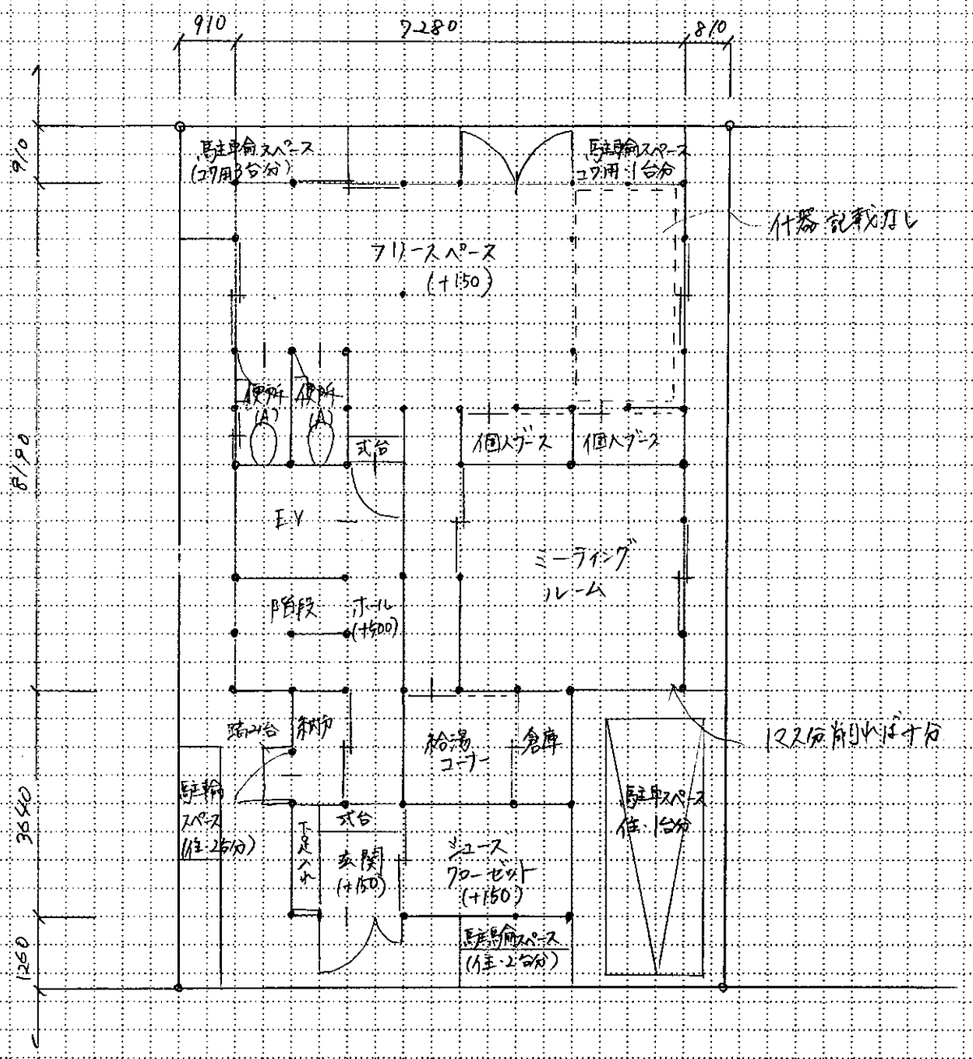

「２階平面プラン」を記入してください。（縮尺1／100）

(注)不正確な内容では、皆さんのプランを正しく評価できません。屋根、庇、室名、柱、開口部、寸法等を正確に記入してください。

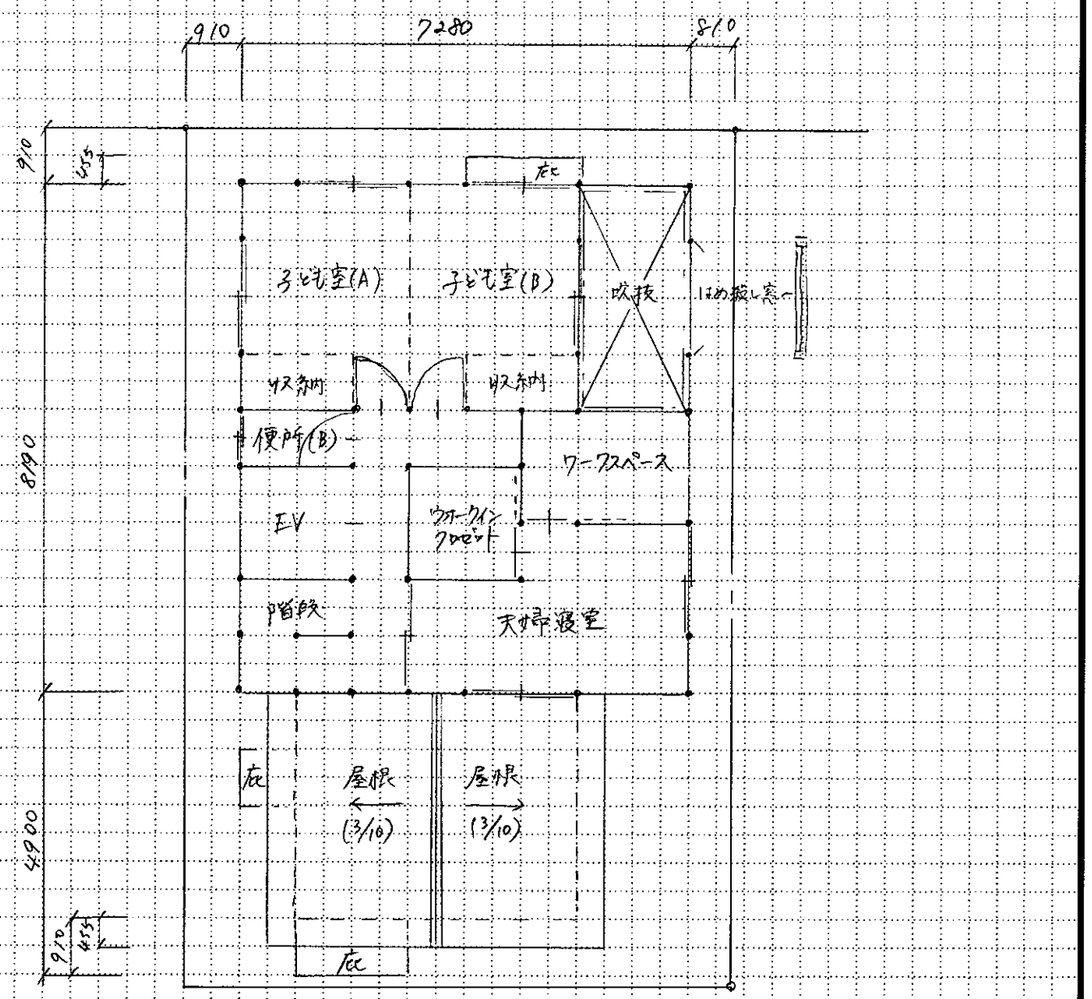


校名	池袋	学生番号	02800 − 0013 − 0406	受験番号	2F − 118547	氏名	飯星 花音	(4)

２０２６年度 ２級建築士 プラン復元用紙 〔2/2〕（本試験プランを丁寧に記入しましょう。）

日建学院

「3階平面プラン」を記入してください。（縮尺1／100）

(注)不正確な内容では、皆さんのプランを正しく評価できません。屋根、庇、室名、柱、開口部、寸法等を正確に記入してください。

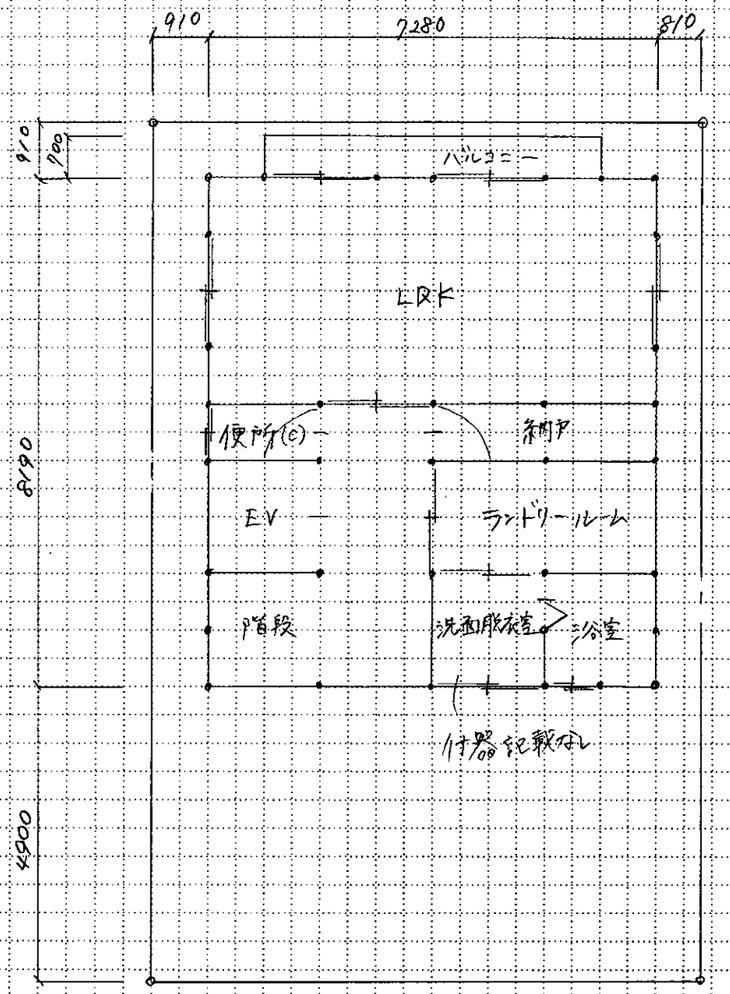

氏名 飯星 花音

「計画の要点等の回答」を記入してください。

設問①：コワーキングスペース部分を道路側に広がるように、開口部を大きく取って開放感を持たせる計画とした。住宅部分はコワーキングスペースから奥まった場所に入口を配置することで、セキュリティやプライバシーを確保した。

設問②：コワーキングスペースの上部に子ども室を配置し、開口部の設置位置などをそろえることで、統一感を持たせるよう計画した。

設問③：準耐火性能であることから、各居室の仕上げについて準耐火構造となるよう選定した。また、住宅部分の面積が200m²以下であるため、竪穴区画とはせず、住宅部分とコワーキングスペース部分を防火設備で区切る計画とした。

「面積表」を記入してください。（※印は出題された場合に記入してください）

敷地面積		9.00 × 14.00	126.	m²
建築面積		(計算式) (7.28×8.19)+(4.55×3.64)	76.18	m²
床面積	1階	(計算式) (7.28×8.19)+(4.55×3.64)	76.18	m²
	2階	(計算式) (7.28×8.19)-(1.82×3.64)	52.99	m²
	3階	(計算式) 7.28×8.19	59.62	m²
延べ面積			188.79	m²
※建蔽率		建築面積 76.18 ／ 敷地面積 126 m²	60.4	%
※容積率		延べ面積 188.79 ／ 敷地面積 126 m²	149	%

「作業時間・見直しの有無など」を記入してください。

プランニング	1.5 分	プラン完成後の見直し ☑した ☐していない
記述・面積表	30 分	作業に要した時間は普段と比べてどうでしたか？ ☑短い ☐同じ ☐長い
平面図	分	作業に要した時間は普段と比べてどうでしたか？ ☑短い ☐同じ ☐長い
立面図	分	作業に要した時間は普段と比べてどうでしたか？ ☑短い ☐同じ ☐長い
伏図	分	作業に要した時間は普段と比べてどうでしたか？ ☑短い ☐同じ ☐長い
部分詳細図	分	作業に要した時間は普段と比べてどうでしたか？ ☑短い ☐同じ ☐長い
見直し・仕上げ	15 分	答案完成後の見直し ☑した ☐していない

オーバー


「本試験を受験して気になる事」を記入してください。（例：○○の意味が分からなかった。）

・土間コンの詳細図の書き方（見本）

講師記入欄


「１階平面兼配置プラン」を記入してください。（縮尺1／100）

(注) 不正確な内容では、皆さんのプランを正しく評価できません。敷地、屋外施設、室名、柱、開口部、寸法等を正確に記入してください。

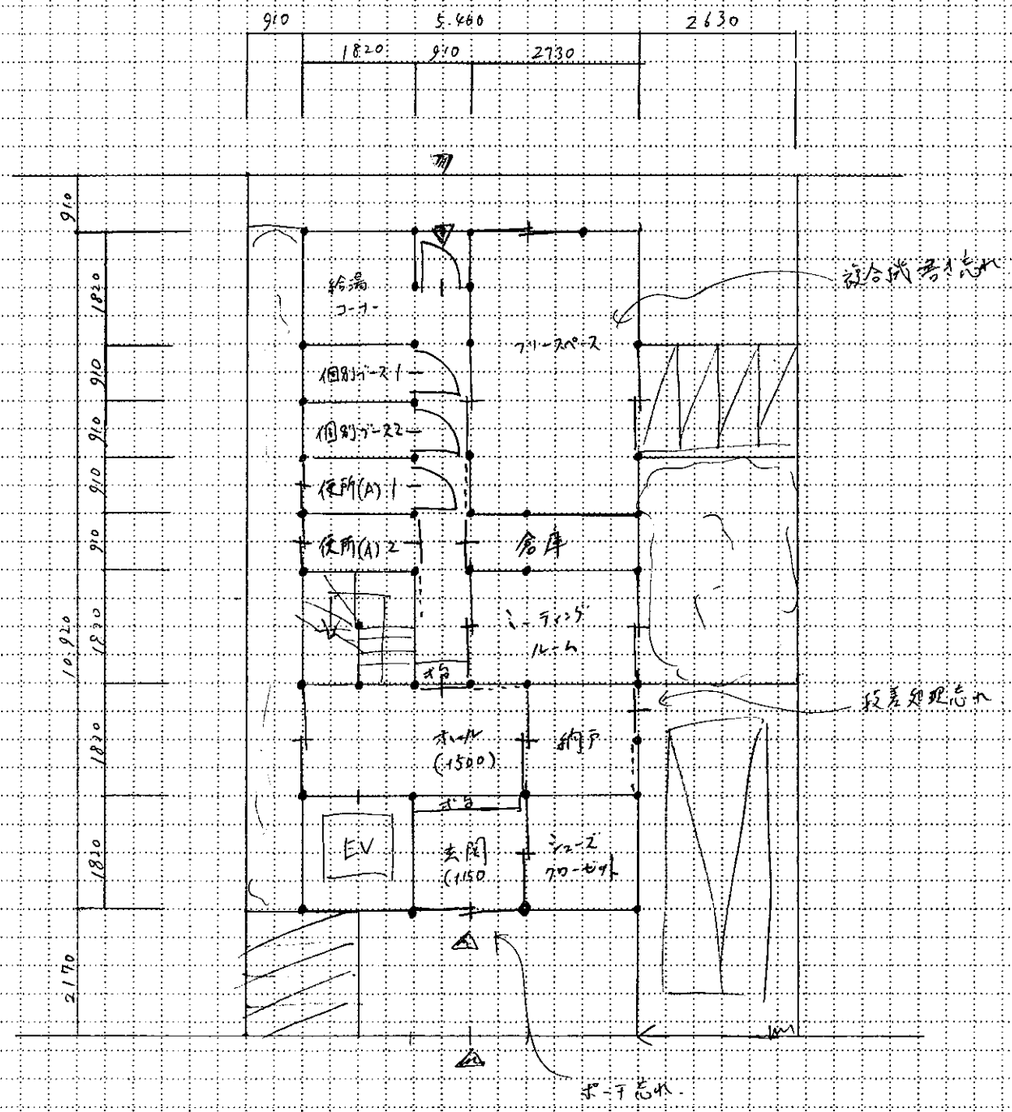

「２階平面プラン」を記入してください。（縮尺1／100）

(注) 不正確な内容では、皆さんのプランを正しく評価できません。屋根、庇、室名、柱、開口部、寸法等を正確に記入してください。

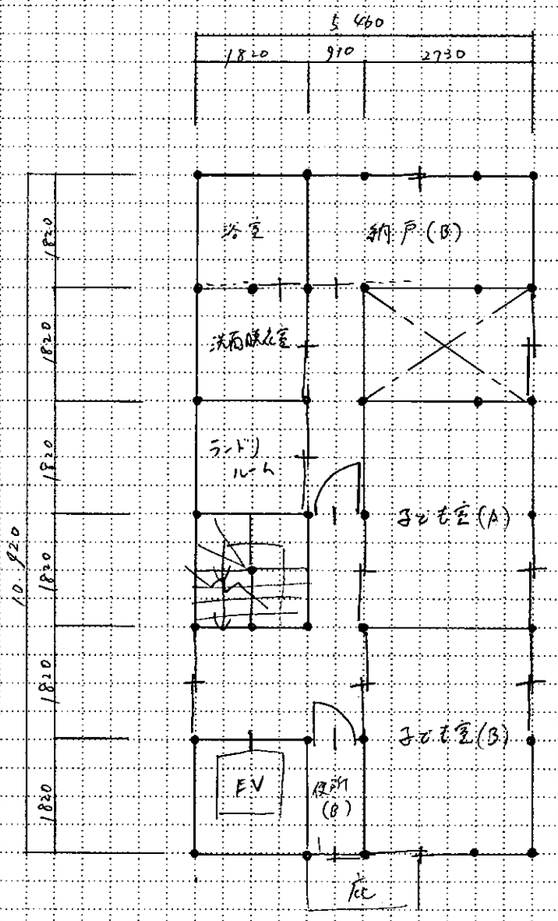


校名		学生番号	— — 0203	受験番号	—	氏名	小谷 龍生	

２０２６年度 ２級建築士 プラン復元用紙 〔2/2〕（本試験プランを丁寧に記入しましょう。）

日建学院

「３階平面プラン」を記入してください。（縮尺1／100）

(注) 不正確な内容では、皆さんのプランを正しく評価できません。屋根、庇、室名、柱、開口部、寸法等を正確に記入してください。

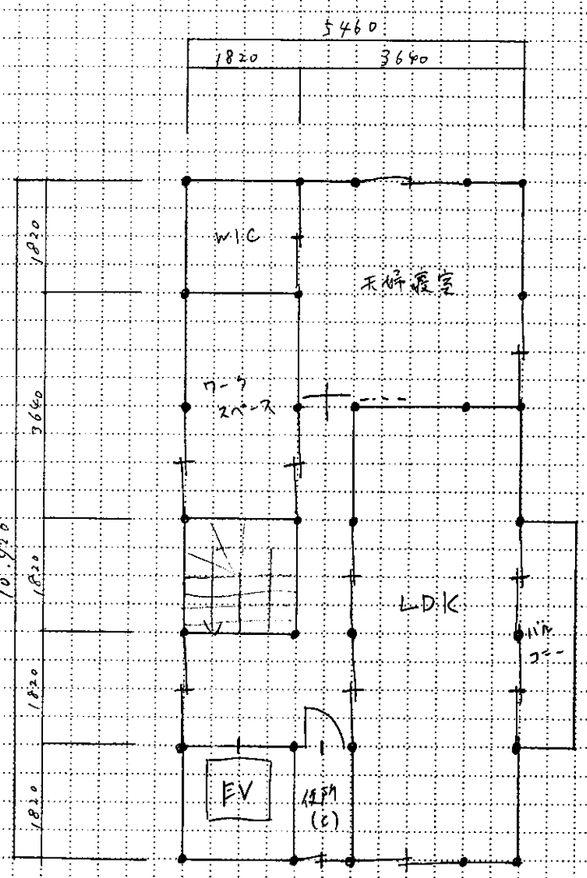

「計画の要点等の回答」を記入してください。

設問①：

・コワーキングスペースは北側道路に近づけて配置し、
各程に立ち寄りやすいアプローチとし、住宅とコワーキング
の間を緑で仕切りつつもゆるやかなプライバシーを確保

設問②：

子ども室を低層・ピロティ部に位置に配置し
スムーズな動線計画とした。共用リビング・スペース
は光が入り、コワーキングスペースの気配が感じられる

設問③：（内容抜粋）

指示された条件を満たした材料を壁・床に
使用した。

「面積表」を記入してください。（※印は出題された場合に記入してください）

敷地面積			126	m²
建築面積		(計算式) 5.46×10.92	59.62	m²
床面積	1階	(計算式) (5.46×10.92)−(0.91×0.91)	58.79	m²
	2階	(計算式) (5.46×10.92)−(2.73×1.82)	54.65	m²
	3階	(計算式) 5.46×10.92	59.62	m²
延べ面積			173.07	m²
※建蔽率		建築面積 59.62 ／ 敷地面積 126 m²	47	%
※容積率		延べ面積 173.07 ／ 敷地面積 126 m²	137	%

「作業時間・見直しの有無など」を記入してください。

プランニング	60 分	プラン完成後の見直し ☑した ☐していない
記述・面積表	30 分	作業に要した時間は普段と比べてどうでしたか？ ☐短い ☑同じ ☐長い
平面図	分	作業に要した時間は普段と比べてどうでしたか？ ☐短い ☐同じ ☐長い
立面図	分	作業に要した時間は普段と比べてどうでしたか？ ☐短い ☐同じ ☐長い
伏　図	分	作業に要した時間は普段と比べてどうでしたか？ ☐短い ☐同じ ☐長い
部分詳細図	分	作業に要した時間は普段と比べてどうでしたか？ ☐短い ☐同じ ☐長い
見直し・仕上げ	20 分	答案完成後の見直し ☑した ☐していない

「本試験を受験して気になる事」を記入してください。（例：○○の意味が分からなかった。）

講師記入欄

氏名 小谷 龍生