

「１階平面兼配置プラン」を記入してください。（縮尺1／100）

（注）不正確な内容では、皆さんのプランを正しく評価できません。敷地、屋外施設、室名、柱、開口部、寸法等を正確に記入してください。

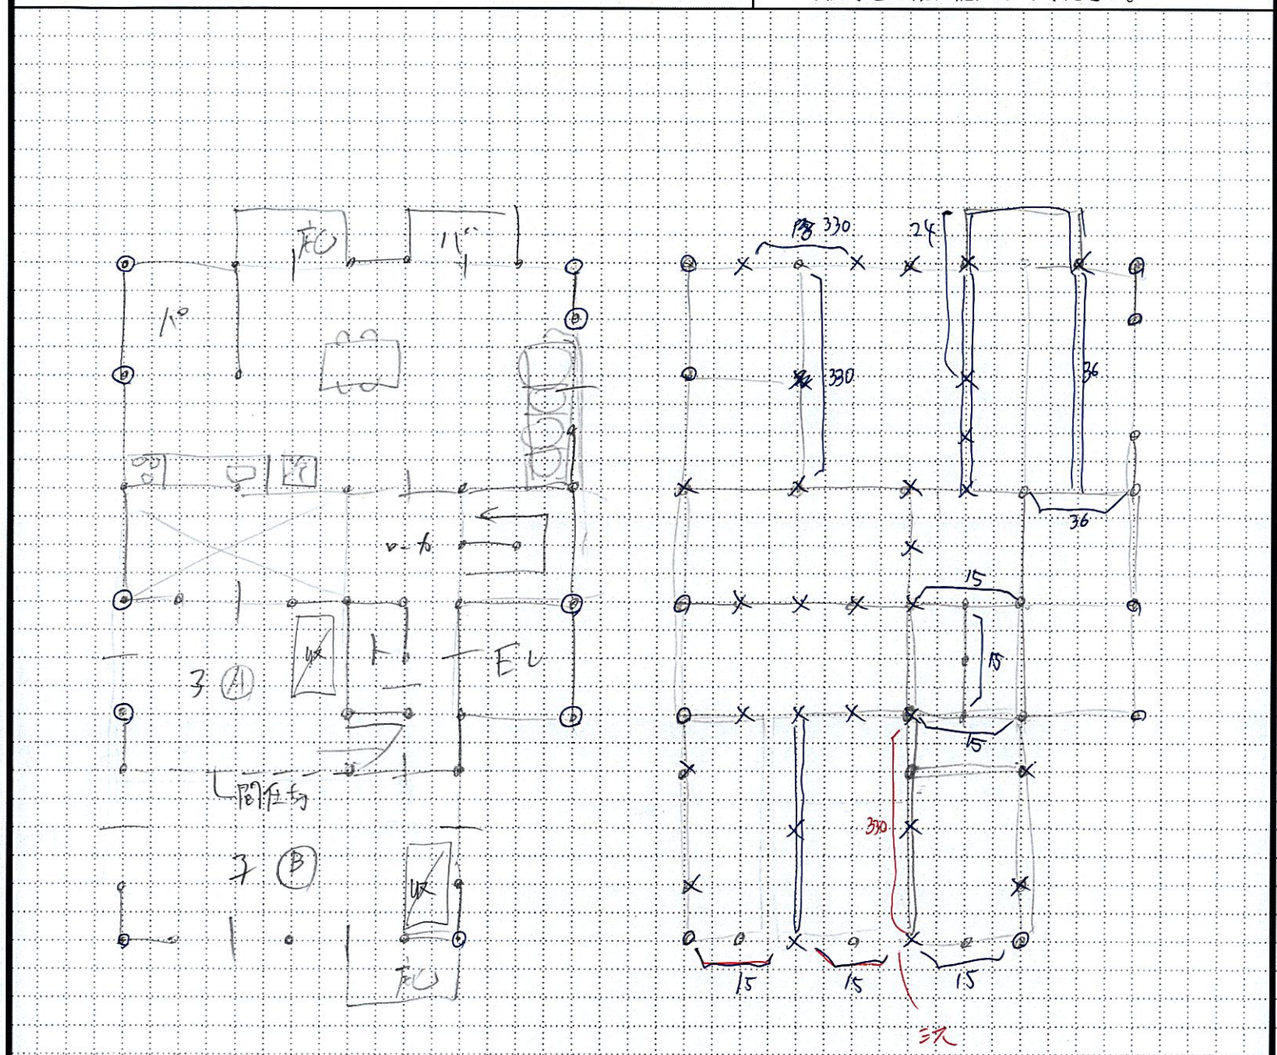

「２階平面プラン」を記入してください。（縮尺1／100）

（注）不正確な内容では、皆さんのプランを正しく評価できません。屋根、庇、室名、柱、開口部、寸法等を正確に記入してください。

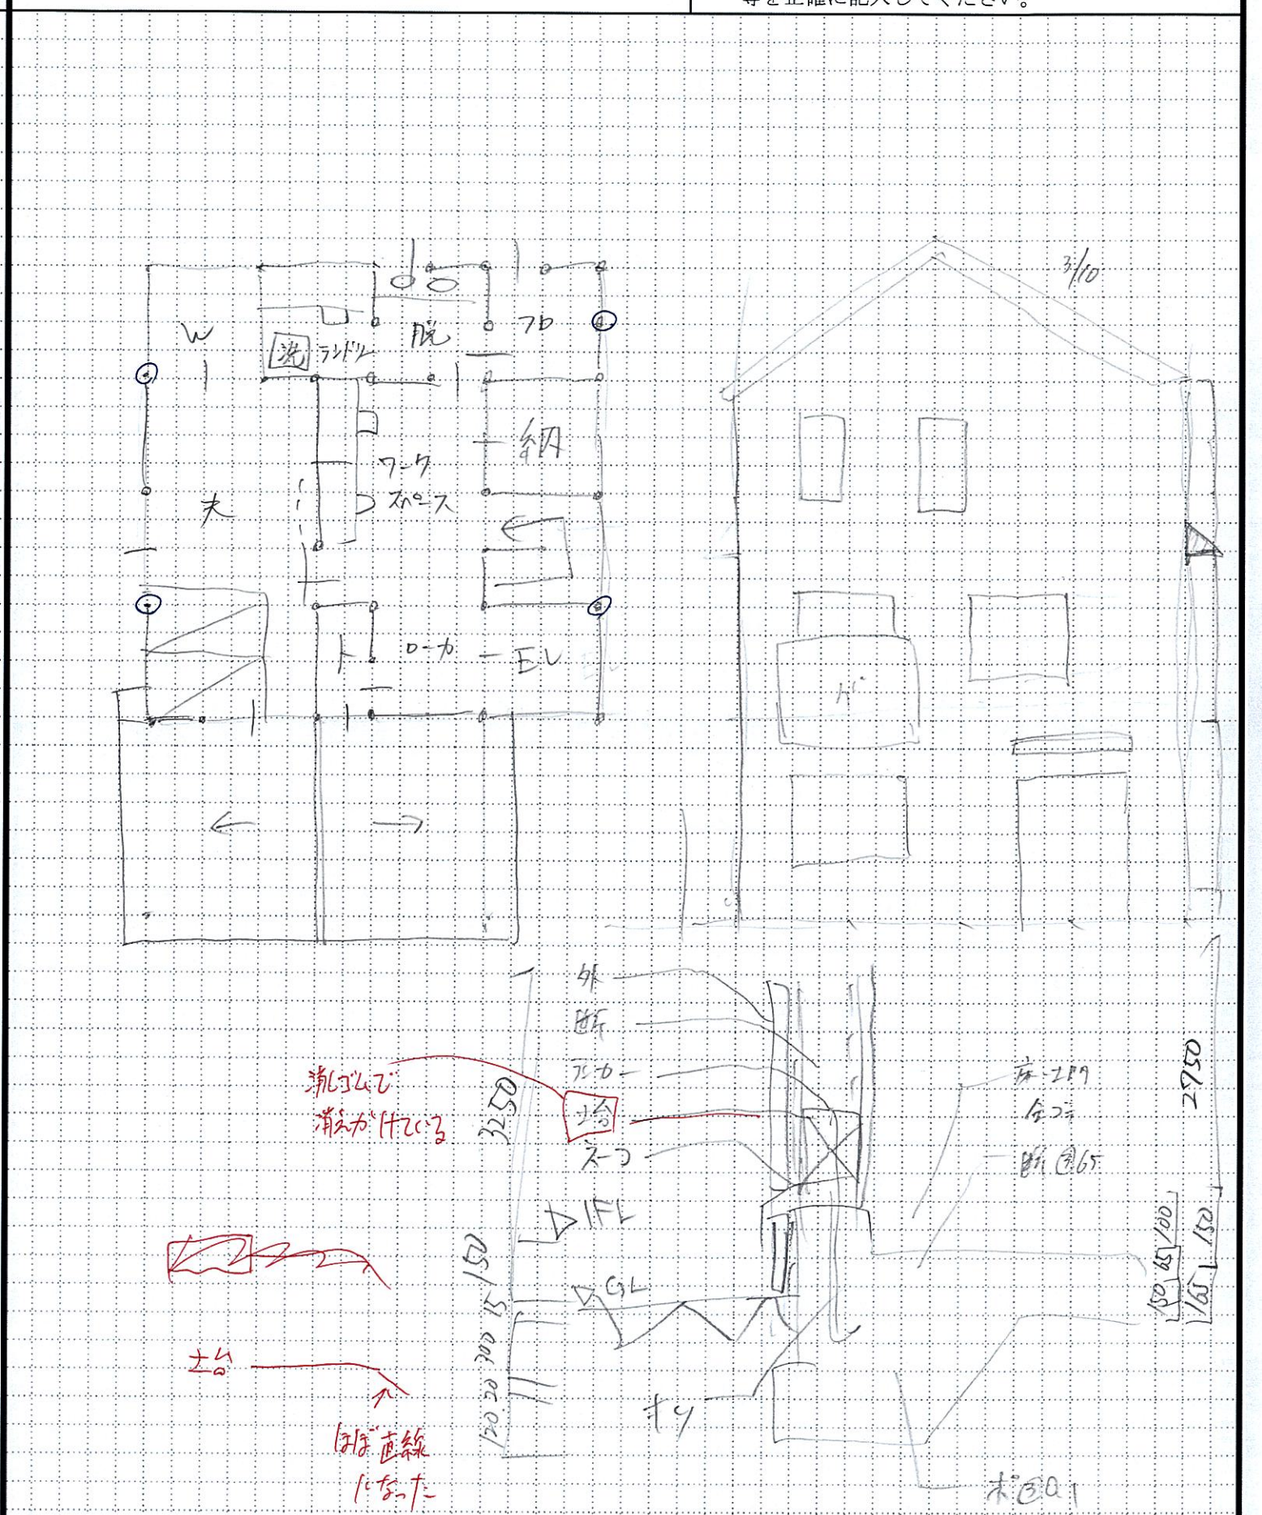


校名		学生番号	－	－	受験番号	－	氏名		

２０２６年度 ２級建築士 プラン復元用紙 〔2/2〕（本試験プランを丁寧に記入しましょう。）

日建学院

「３階平面プラン」を記入してください。（縮尺1／100）

(注)不正確な内容では、皆さんのプランを正しく評価できません。屋根、庇、室名、柱、開口部、寸法等を正確に記入してください。

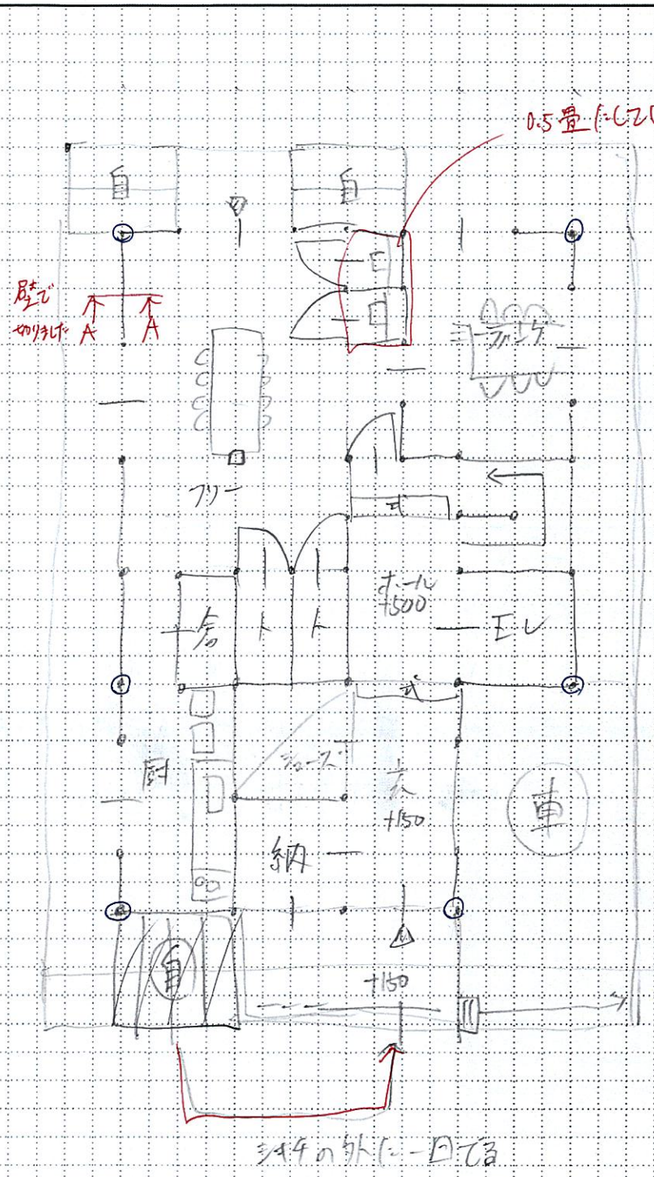

「計画の要点等の回答」を記入してください。

設問①：

ワークスペースを北に寄せて集客性に配慮。
住用を南に配置しプライバシーに配慮。

設問②：

子ども(A)と吹抜を隣接
下階 ワークスペースが見渡せる

設問③：

屋・床を石こう 15mm にし火災の際支障のない計画
外壁を金属にし延焼を軽減

↑ 4行ギ 2.5行 ほどしか うまてな～

「面積表」を記入してください。（※印は出題された場合に記入してください）

敷地面積		㎡	
建築面積	(計算式) (72×72)+(54×36)	72.87 ㎡	
床面積 1階	(計算式) (72×72)+(54×36)	72.87 ㎡	
床面積 2階	(計算式) (72×72)+(54×36)−(36×18)	66.24 ㎡	
床面積 3階	(計算式) 72×72	52.99 ㎡	
延べ面積		192.10 ㎡	
※建蔽率	建築面積 ／ 敷地面積 ㎡	57 %	
※容積率	延べ面積 ／ 敷地面積 ㎡	65 %	

「作業時間・見直しの有無など」を記入してください。

プランニング	90 分	プラン完成後の見直し ☑した ☐していない
記述・面積表	分	作業に要した時間は普段と比べてどうでしたか？ ☐短い ☐同じ ☐長い
平面図	分	作業に要した時間は普段と比べてどうでしたか？ ☐短い ☐同じ ☐長い
立面図	分	作業に要した時間は普段と比べてどうでしたか？ ☐短い ☐同じ ☐長い
伏図	分	作業に要した時間は普段と比べてどうでしたか？ ☐短い ☐同じ ☐長い
部分詳細図	250 分	作業に要した時間は普段と比べてどうでしたか？ ☐短い ☐同じ ☐長い
見直し・仕上げ	50 分	答案完成後の見直し ☐した ☐していない

「本試験を受験して気になる事」を記入してください。（例：○○の意味が分からなかった。）

物動可能 収納を  とかいた。

駐輪スペースが一旦敷地外にでて玄関にまわるつくりとなった

個別ブースを 0.91×0.91で計画してしまった


間仕切の床に深さがないかもしれない

講師記入欄

氏名 [illegible]井 洸樹


「１階平面兼配置プラン」を記入してください。（縮尺1／100）

(注)不正確な内容では、皆さんのプランを正しく評価できません。敷地、屋外施設、室名、柱、開口部、寸法等を正確に記入してください。

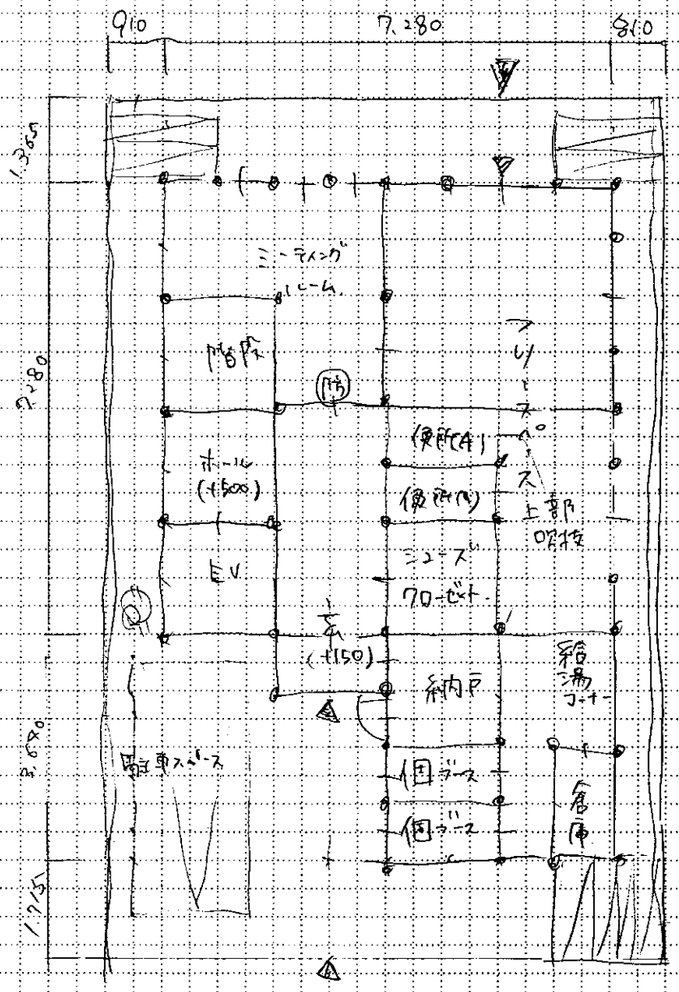

「２階平面プラン」を記入してください。（縮尺1／100）

(注)不正確な内容では、皆さんのプランを正しく評価できません。屋根、庇、室名、柱、開口部、寸法等を正確に記入してください。

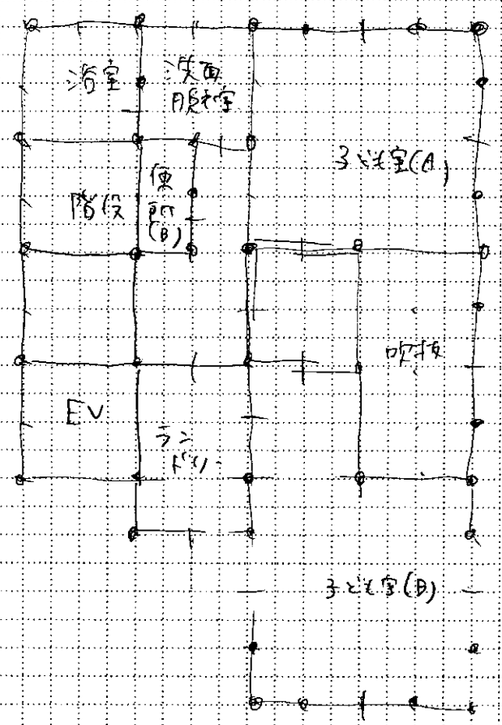


校名		学生番号	－	－	受験番号	－	氏名	木川理奈		(1)

２０２６年度 ２級建築士 プラン復元用紙 〔2/2〕（本試験プランを丁寧に記入しましょう。）

日建学院

「３階平面プラン」を記入してください。（縮尺1／100）

(注)不正確な内容では、皆さんのプランを正しく評価できません。屋根、庇、室名、柱、開口部、寸法等を正確に記入してください。

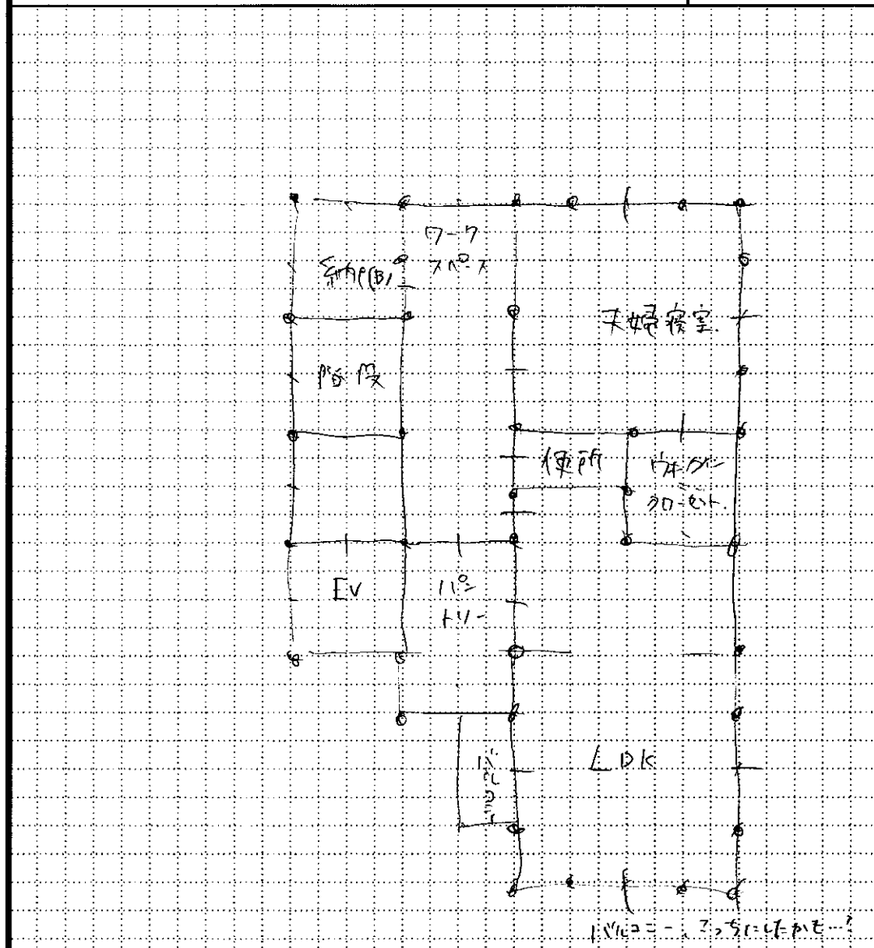

氏名 大川 理来

「計画の要点等の回答」を記入してください。

設問①：北側に窓を多く設け、視認性、集客性、収益を得られるようにした。セキュリティーカギを設け、コーキングスペースは北側、住戸部分は南、アプローチ分け、プライバシー確保した

設問②：子ども室、2室とも道路側に面し置し、採光、通風、住環境に配慮した。将来、1室としても使用できるよう、間仕切りとし、子ども室の間に吹抜けを設けたことで、室同士の距離を取ることで、プライバシーに配慮した。

設問③：木造3階建、準耐火構造として、延焼のおそれのある部分は、防火設備を設け、また、耐火性能のある材料を使用した。

「面積表」を記入してください。（※印は出題された場合に記入してください）

敷地面積		126 m²	
建築面積	(計算式) (7.28×7.28)+(3.64×3.64)+(1.82×0.91)	67.88 m²	
床面積	1階	(計算式) (7.28×7.28)+(3.64×3.64)+(1.82×0.91)	67.88 m²
	2階	(計算式) (7.28×7.28)+(3.64×3.64)+(1.82×0.91)−(1.82×3.64)	61.26 m²
	3階	(計算式) (7.28×7.28)+(3.64×3.64)+(1.82×0.91)	67.88 m²
延べ面積		195.92 m²	
※建蔽率	建築面積 67.88 ／ 敷地面積 126 m²	53 %	
※容積率	延べ面積 195.92 ／ 敷地面積 126 m²	1.55 %	

「作業時間・見直しの有無など」を記入してください。

プランニング	90 分	プラン完成後の見直し ☑した □していない
記述・面積表	10 分	作業に要した時間は普段と比べてどうでしたか？ ☑短い □同じ □長い
平面図	分	作業に要した時間は普段と比べてどうでしたか？ ☑短い □同じ □長い
立面図	分	作業に要した時間は普段と比べてどうでしたか？ ☑短い □同じ □長い
伏図	分	作業に要した時間は普段と比べてどうでしたか？ ☑短い □同じ □長い
部分詳細図	分	作業に要した時間は普段と比べてどうでしたか？ ☑短い □同じ □長い
見直し・仕上げ	分	答案完成後の見直し ☑した □していない

「本試験を受験して気になる事」を記入してください。（例：○○の意味が分からなかった。）


・納戸(A)、作図中に、外からも使用できるようにすることに気づき、玄関をつけ加えました。面積表も書きなおしました。

・子ども室(A)(B)、道路側、道路側…採光を取らなきゃと考えすぎてしまい、吹抜をはさんでしまいました。隣接させている。とみなされると良いのですが……。

講師記入欄


「１階平面兼配置プラン」を記入してください。（縮尺1／100）

(注)不正確な内容では、皆さんのプランを正しく評価できません。敷地、屋外施設、室名、柱、開口部、寸法等を正確に記入してください。

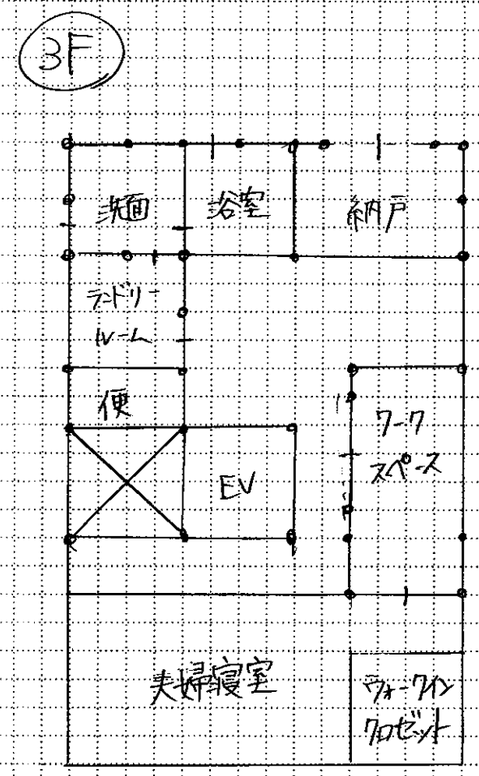

「２階平面プラン」を記入してください。（縮尺1／100）

(注)不正確な内容では、皆さんのプランを正しく評価できません。屋根、庇、室名、柱、開口部、寸法等を正確に記入してください。

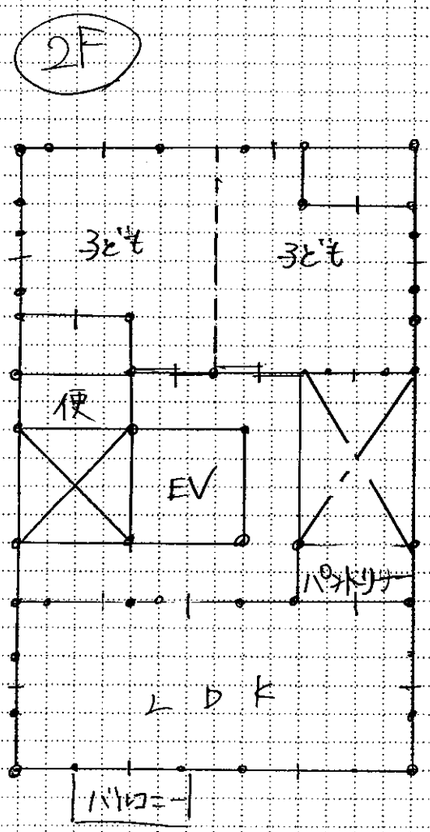


校名		学生番号	—	—	受験番号	—	氏名	矢野 夏海	

２０２６年度 ２級建築士 プラン復元用紙 〔2/2〕（本試験プランを丁寧に記入しましょう。）

日建学院

「３階平面プラン」を記入してください。（縮尺1／100）

（注）不正確な内容では、皆さんのプランを正しく評価できません。屋根、庇、室名、柱、開口部、寸法等を正確に記入してください。

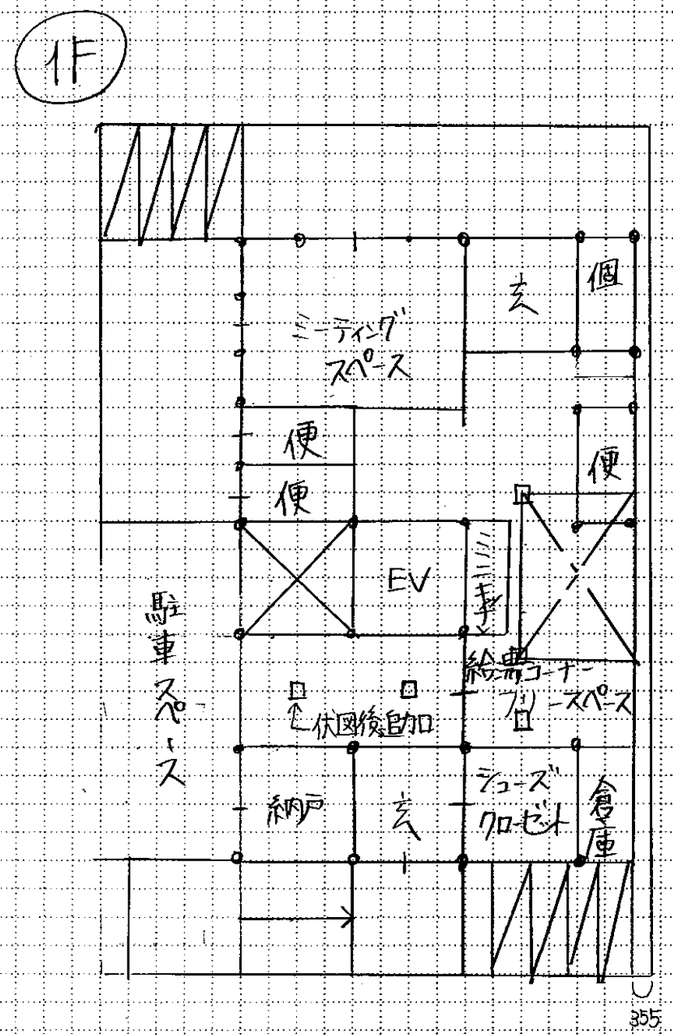

「計画の要点等の回答」を記入してください。

設問①：気軽に立ち寄れるよう、道路側に入口を設けた。またセキュリティーに配慮して間の通路に植栽や駐輪場を設けた。

設問②：将来的にコワーキングスペースになったときに四方向から通風が取れる位置に水抜けを設けた。

設問③：

主要構造物を耐火仕様とした。また、住宅部分が200㎡以下なので、コワーキングスペースと住宅部分の間に防火扉を設け、防火区画した。

「面積表」を記入してください。（※印は出題された場合に記入してください）

敷地面積		126 ㎡	
建築面積	(計算式) 6.37×10.01	63.76 ㎡	
床面積	1階 (計算式) 6.37×10.01	63.76 ㎡	
	2階 (計算式) (6.37×10.01)-(1.82×2.73)	58.8 ㎡	
	3階 (計算式) 6.37×10.01	63.76 ㎡	
延べ面積		186.32 ㎡	
※建蔽率	建築面積 ／ 敷地面積 ㎡	50.6 %	
※容積率	延べ面積 ／ 敷地面積 ㎡	147 %	

「作業時間・見直しの有無など」を記入してください。

プランニング	分	プラン完成後の見直し ☑した □していない
記述・面積表	10 分	作業に要した時間は普段と比べてどうでしたか？ □短い ☑同じ □長い
平面図	90 分	作業に要した時間は普段と比べてどうでしたか？ □短い ☑同じ □長い
立面図	10 分	作業に要した時間は普段と比べてどうでしたか？ □短い ☑同じ □長い
伏　図	20 分	作業に要した時間は普段と比べてどうでしたか？ □短い ☑同じ □長い
部分詳細図	20 分	作業に要した時間は普段と比べてどうでしたか？ □短い □同じ □長い
見直し・仕上げ	10 分	答案完成後の見直し ☑した □していない

「本試験を受験して気になる事」を記入してください。（例：○○の意味が分からなかった。）

土間下地の意味とは違えベタ基礎の通常の部分詳細図を描いた。
通し柱を○しわすれた。
非常用進入口を忘れた。（立面）
敷地図をずらした。


講師記入欄

氏名 片野 夏海

日建学院


「１階平面兼配置プラン」を記入してください。（縮尺1／100）

(注)不正確な内容では、皆さんのプランを正しく評価できません。敷地、屋外施設、室名、柱、開口部、寸法等を正確に記入してください。

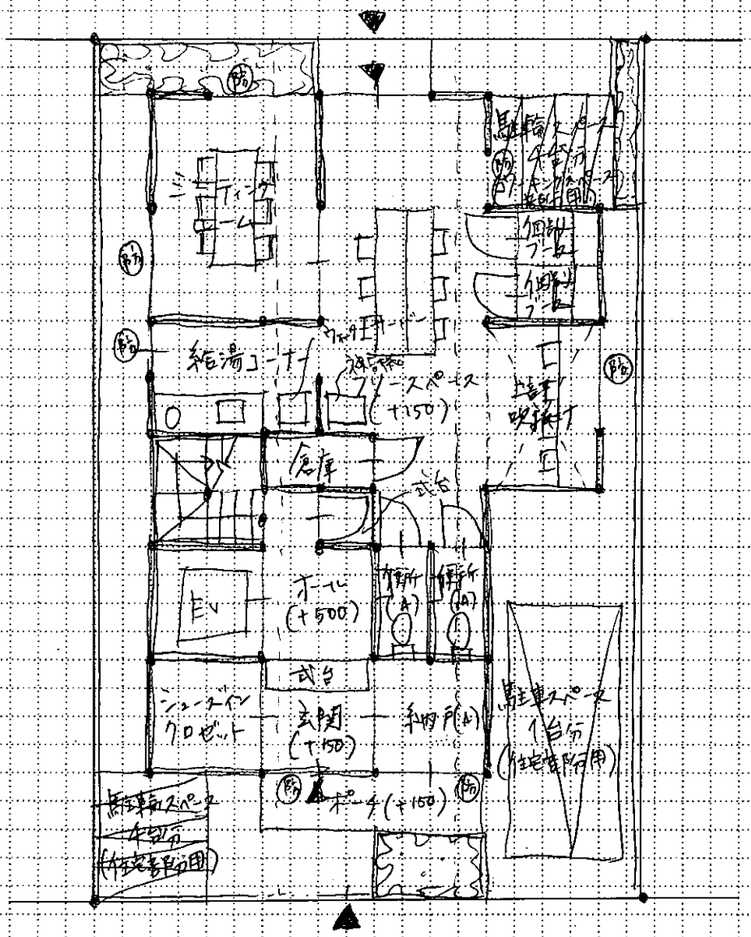

「２階平面プラン」を記入してください。（縮尺1／100）

(注)不正確な内容では、皆さんのプランを正しく評価できません。屋根、庇、室名、柱、開口部、寸法等を正確に記入してください。

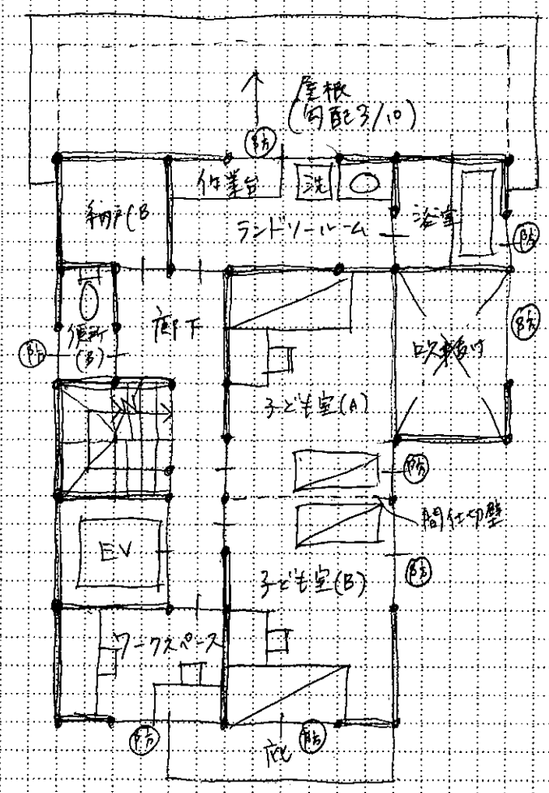


校名	池袋本校	学生番号	－	－	受験番号	－	氏名	佐藤 日花	

２０２６年度 ２級建築士 プラン復元用紙 〔2/2〕（本試験プランを丁寧に記入しましょう。）

日建学院

「３階平面プラン」を記入してください。（縮尺1／100）

(注)不正確な内容では、皆さんのプランを正しく評価できません。屋根、庇、室名、柱、開口部、寸法等を正確に記入してください。

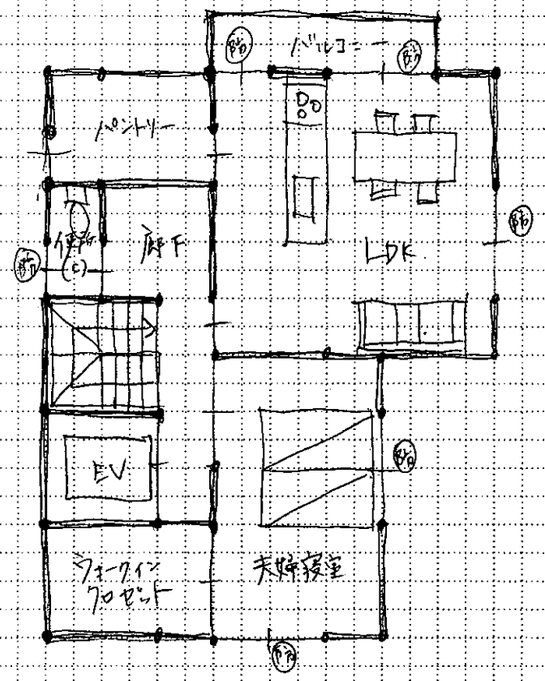

「計画の要点等の回答」を記入してください。

設問①：コワーキングスペース部分を気軽に利用できるよう、道路境界線から入口をできるだけ近くに配置した。住宅部分は、道路境界線から2170mm離して建物を配置し、セキュリティーやプライバシーの確保に配慮した。

設問②：子ども室として使う際、子ども室(A)は南面していないが吹抜けと隣接することで明るい空間になるようにした。将来対応のため、子ども室(A)と子ども室(B)を隣接させた。

設問③：準耐火構造とするため、外壁は、ガルバリウム鋼板を採用した。また、内装は、天井を3層が石コウボード15mmとすることで、準耐火構造となるよう配慮した。

「面積表」を記入してください。（※印は出題された場合に記入してください）

敷地面積		126.00 ㎡	
建築面積	(計算式) (10.92×5.46)+(4.55×1.82)	67.90 ㎡	
床面積 1階	(計算式) (10.92×5.46)+(4.55×1.82)	67.90 ㎡	
床面積 2階	(計算式) (9.10×5.46)+(4.55×1.82)-(2.73×1.82)	52.99 ㎡	
床面積 3階	(計算式) (9.10×5.46)+(4.55×1.82)	57.96 ㎡	
延べ面積		178.85 ㎡	
※建蔽率	建築面積 67.90 ／ 敷地面積 126 ㎡	53 %	
※容積率	延べ面積 178.85 ／ 敷地面積 126 ㎡	141 %	

「作業時間・見直しの有無など」を記入してください。

プランニング	1時間55分	プラン完成後の見直し ☑した □していない
記述・面積表	分	作業に要した時間は普段と比べてどうでしたか？ □短い ☑同じ □長い
平面図	1時間23分	作業に要した時間は普段と比べてどうでしたか？ ☑短い □同じ □長い
立面図	18分	作業に要した時間は普段と比べてどうでしたか？ □短い □同じ □長い
伏図	(8/5間違えた) +22分	作業に要した時間は普段と比べてどうでしたか？ □短い □同じ □長い
部分詳細図	23分	作業に要した時間は普段と比べてどうでしたか？ □短い □同じ □長い
見直し・仕上げ	20分	答案完成後の見直し □した □していない

「本試験を受験して気になる事」を記入してください。（例：○○の意味が分からなかった。）


- 1大間を描く場所がいつもと違って最初立面図の場所に描いてしまった。(8/5のロス)
- 子ども室(A)と吹抜けの間を腰壁のような薄い線で描いてしまった。
- 計画の要点②がすっこう抜けたことを書いている。
- 図面を消す回数が多くて図面が汚なくなってしまった。
- バルコニーの下に柱を描いたが不安

講師記入欄

氏名	佐藤 日花


「１階平面兼配置プラン」を記入してください。（縮尺1／100）

(注) 不正確な内容では、皆さんのプランを正しく評価できません。敷地、屋外施設、室名、柱、開口部、寸法等を正確に記入してください。

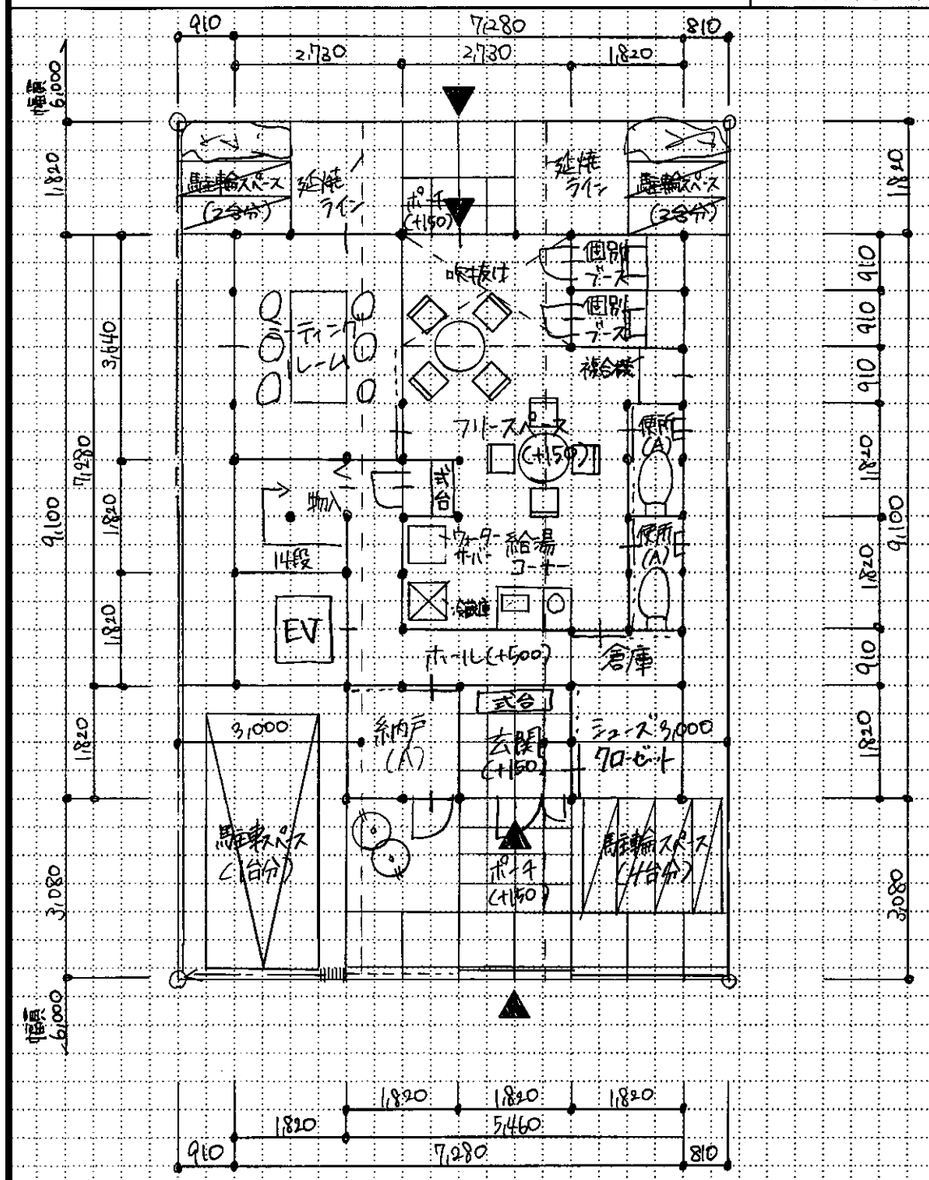

「２階平面プラン」を記入してください。（縮尺1／100）

(注) 不正確な内容では、皆さんのプランを正しく評価できません。屋根、庇、室名、柱、開口部、寸法等を正確に記入してください。

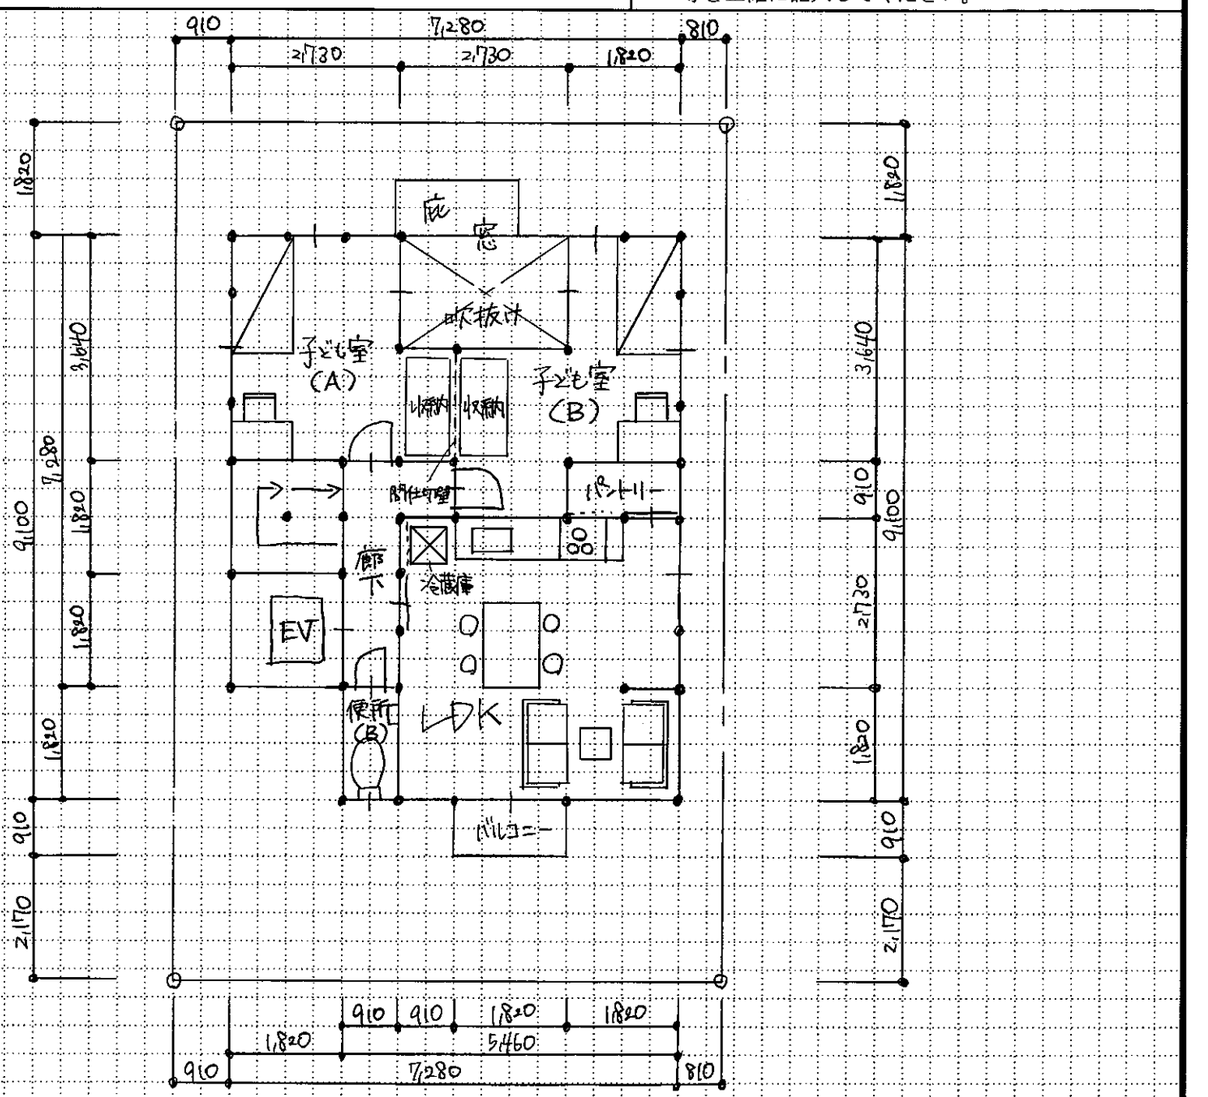

※2階及び3階は全域延焼ライン


校名	池袋	学生番号	02800 - 1724 - 0120	受験番号	2F - 21725K	氏名	門田 汐梨	①

2026年度 2級建築士 プラン復元用紙 〔2/2〕（本試験プランを丁寧に記入しましょう。）

日建学院

「3階平面プラン」を記入してください。（縮尺1／100）

（注）不正確な内容では、皆さんのプランを正しく評価できません。屋根、庇、室名、柱、開口部、寸法等を正確に記入してください。

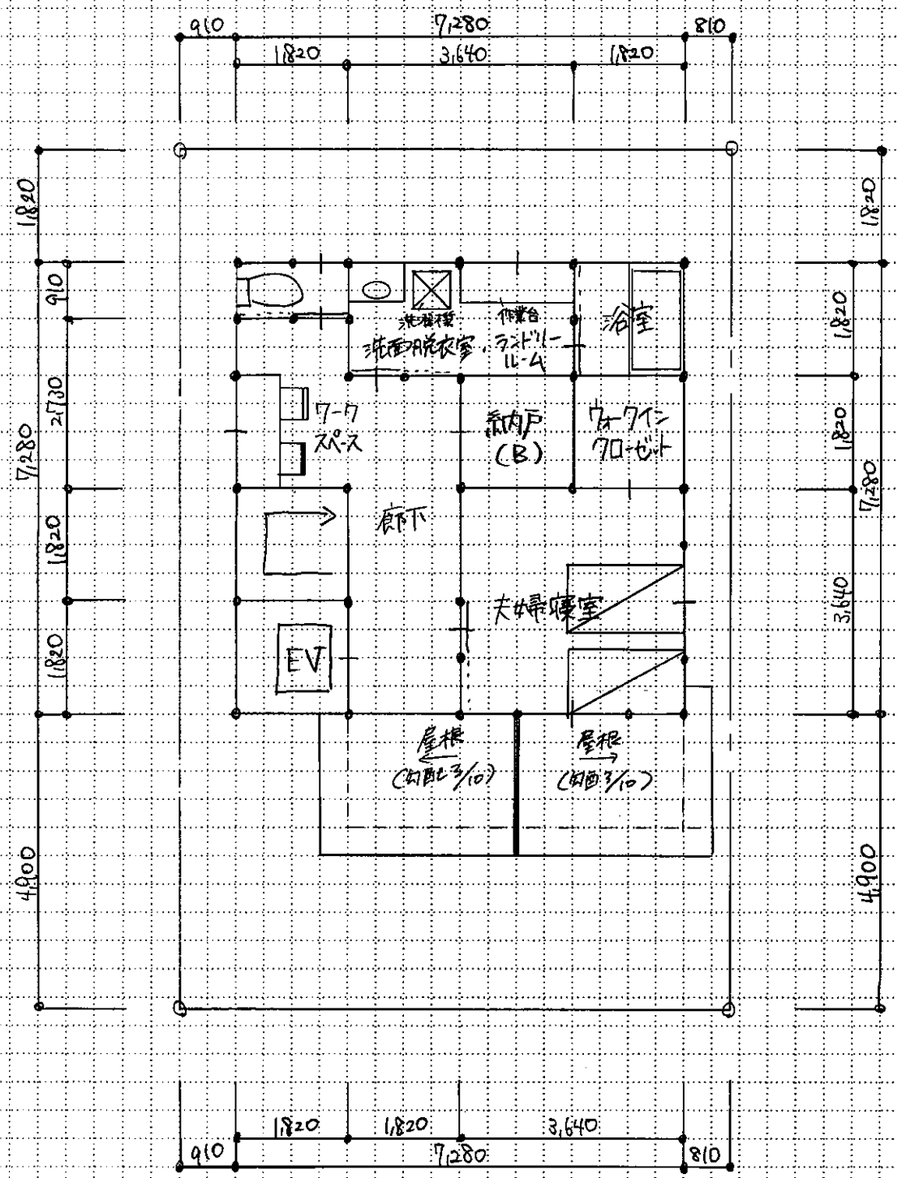

「計画の要点等の回答」を記入してください。

設問①：商店街がある北側の離隔をできるだけ小さくし、視認性を高め、立ち寄りやすくした。住宅部分の居室やバルコニーは、できるだけ南面させ、商店街からの視線等に配慮した。

設問②：子ども室(A)と子ども室(B)の間に吹抜けを設けることで、将来2階のどの位置でも上下階のつながりを感じられるようにした。

設問③：外壁をガルバリウム鋼板小波とし、天井を強化石コウボードとすることで、準耐火構造について、配慮した。

「面積表」を記入してください。（※印は出題された場合に記入してください）

敷地面積			126.00 m²
建築面積		(計算式) (7.28×7.28)+(1.82×5.46)	62.93 m²
床面積	1階	(計算式) (7.28×7.28)+(1.82×5.46)	62.93 m²
	2階	(計算式) (7.28×7.28)+(1.82×5.46)-(2.73×1.82)	57.96 m²
	3階	(計算式) 7.28×7.28	52.99 m²
延べ面積			173.88 m²
※建蔽率		建築面積 ／ 敷地面積 m²	%
※容積率		延べ面積 ／ 敷地面積 m²	%

「作業時間・見直しの有無など」を記入してください。

プランニング	75 分	プラン完成後の見直し	☑した ☐していない
記述・面積表	分	作業に要した時間は普段と比べてどうでしたか？	☑短い ☐同じ ☐長い
平面図	分	作業に要した時間は普段と比べてどうでしたか？	☐短い ☑同じ ☐長い
立面図	分	作業に要した時間は普段と比べてどうでしたか？	☑短い ☐同じ ☐長い
伏図	分	作業に要した時間は普段と比べてどうでしたか？	☐短い ☑同じ ☐長い
部分詳細図	分	作業に要した時間は普段と比べてどうでしたか？	☐短い ☐同じ ☑長い
見直し・仕上げ	15 分	答案完成後の見直し	☑した ☐していない

「本試験を受験して気になる事」を記入してください。（例：○○の意味が分からなかった。）

平面図
- 2階のLDK内の家具の配置が上手くまとまらなかった。バルコニーに出づらいプランになった。
- 〃 子ども室の「移動可能な収納」の表現がわからなかった。
- 3階の夫婦寝室の採光が足りているか。（2階の屋根のことを考えていなかった。）
- 部分詳細図 ケント紙をかいてしまった。
- 〃 寸法について、屋根の寸法をかいていない。
- 計画の要点 ②が1行余った。③は2行余った。（欄は4行）③が何を書けばよいかわからなかった。


講師記入欄

氏名 門田 汐梨

日建学院


「１階平面兼配置プラン」を記入してください。（縮尺1／100）

(注) 不正確な内容では、皆さんのプランを正しく評価できません。敷地、屋外施設、室名、柱、開口部、寸法等を正確に記入してください。

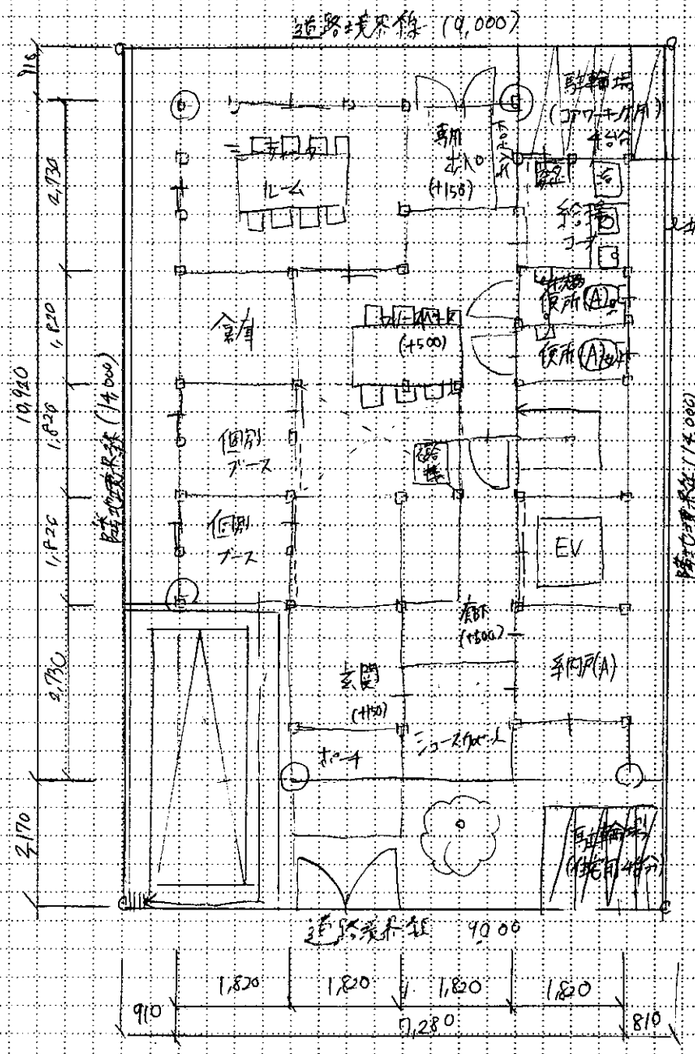

「２階平面プラン」を記入してください。（縮尺1／100）

(注) 不正確な内容では、皆さんのプランを正しく評価できません。屋根、庇、室名、柱、開口部、寸法等を正確に記入してください。

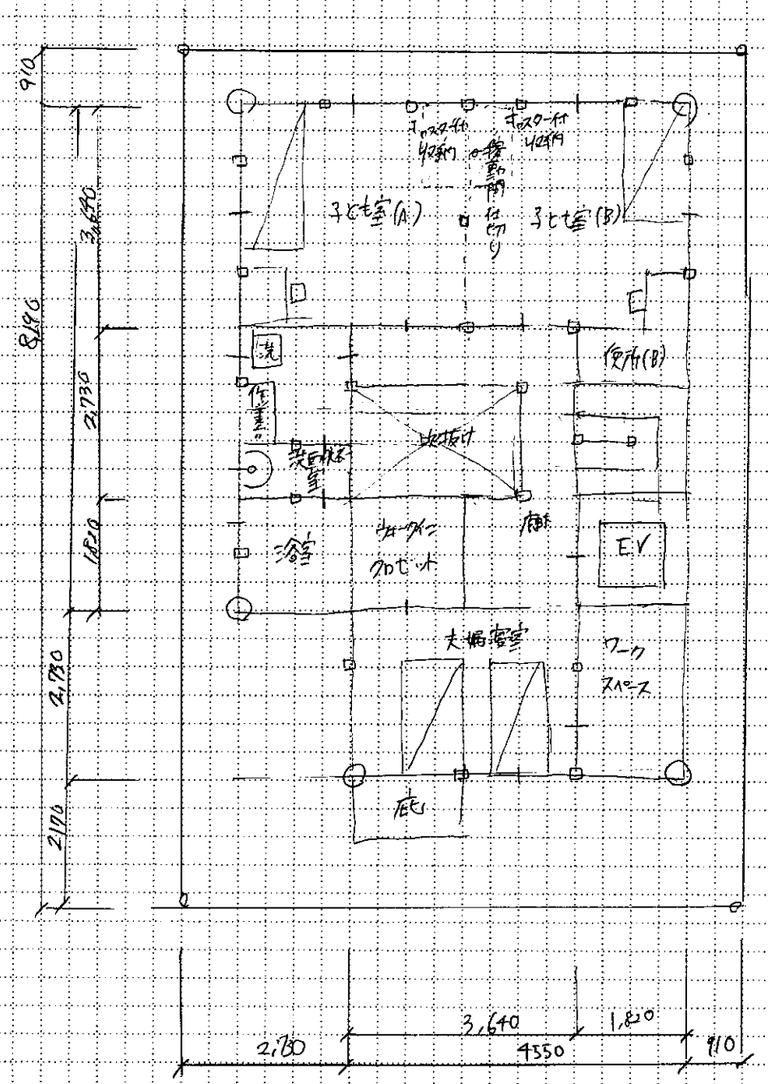


校名		学生番号	－	－	受験番号	－	氏名	金子	

２０２６年度 ２級建築士 プラン復元用紙 〔2/2〕（本試験プランを丁寧に記入しましょう。）

日建学院

「３階平面プラン」を記入してください。（縮尺1／100）

(注)不正確な内容では、皆さんのプランを正しく評価できません。屋根、庇、室名、柱、開口部、寸法等を正確に記入してください。

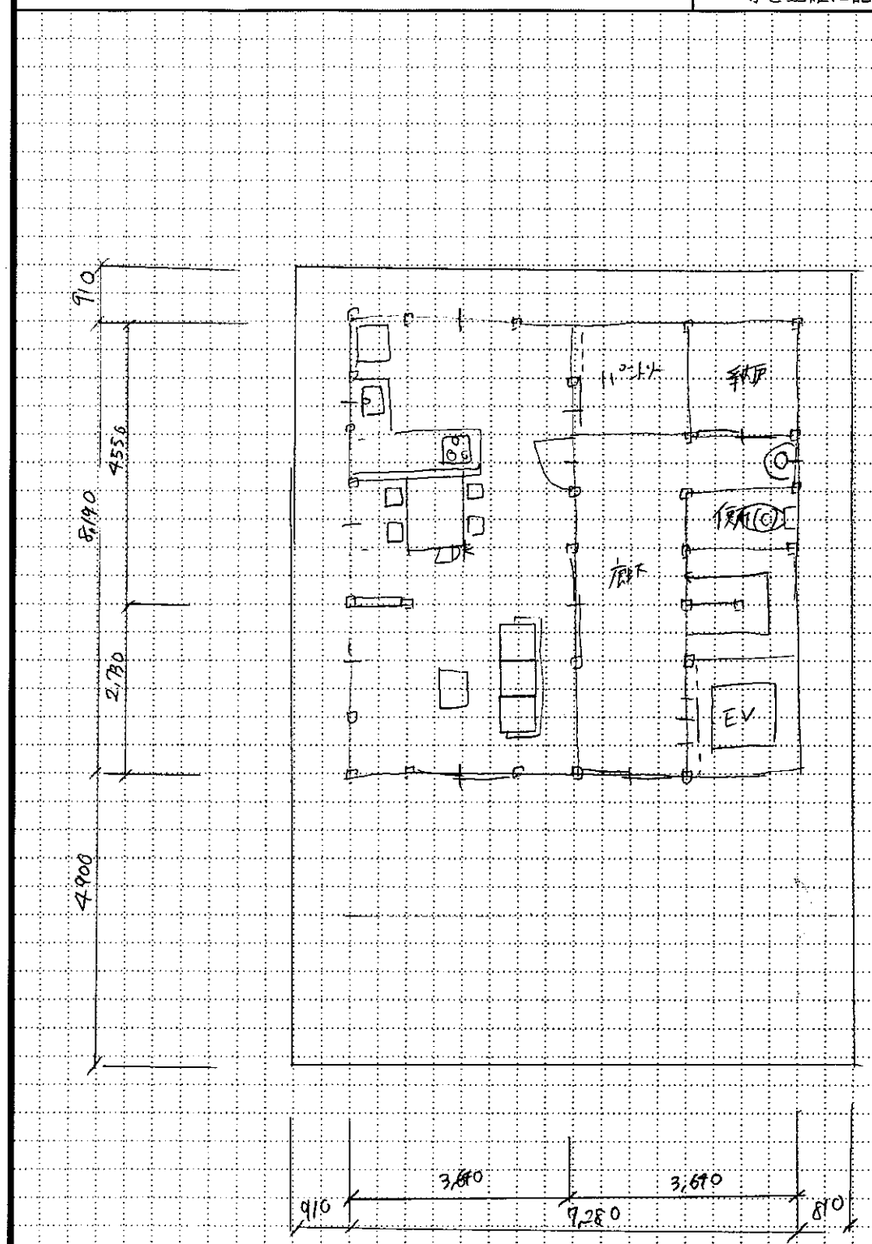

「計画の要点等の回答」を記入してください。

設問①：

北側道路に沿って、コワーキングスペース部分の建物を設けた。視認性を高め、気軽に立ち寄りやすいようエスプ

設問②：

子ども室を将来コアワーキング部分として使用する為、稼事の間仕切を用いた。間仕切りて区切ることで、どんな用途でも変形できるような広々な空間とした。

設問③：

開口部には防火設備を用いた。

「面積表」を記入してください。（※印は出題された場合に記入してください）

敷地面積		126,00 m²	
建築面積	(計算式) 10,92×7,28+(5,46×2,73)		94,40 m²
床面積 1階	(計算式) 10,92×7,28+(5,46×2,73)-2(1,82×0,91)		91,09 m²
床面積 2階	(計算式) 10,92×7,28-(2,73×0,91)		77,01 m²
床面積 3階	(計算式) 7,28×8,19		59,62 m²
延べ面積			227,72 m²
※建蔽率	建築面積 94,40 ／ 敷地面積 126,00 m²		74 %
※容積率	延べ面積 227,72 ／ 敷地面積 126,00 m²		180 %

「作業時間・見直しの有無など」を記入してください。

プランニング	140 分	プラン完成後の見直し □した ☑していない
記述・面積表	5 分	作業に要した時間は普段と比べてどうでしたか？ ☑短い □同じ □長い
平面図	70 分	作業に要した時間は普段と比べてどうでしたか？ ☑短い □同じ □長い
立面図	20 分	作業に要した時間は普段と比べてどうでしたか？ □短い ☑同じ □長い
伏図	20 分	作業に要した時間は普段と比べてどうでしたか？ □短い ☑同じ □長い
部分詳細図	15 分	作業に要した時間は普段と比べてどうでしたか？ ☑短い □同じ □長い
見直し・仕上げ	0 分	答案完成後の見直し □した ☑していない

「本試験を受験して気になる事」を記入してください。（例：○○の意味が分からなかった。）


講師記入欄

氏名 金子.

(C)


「１階平面兼配置プラン」を記入してください。（縮尺1／100）

(注)不正確な内容では、皆さんのプランを正しく評価できません。敷地、屋外施設、室名、柱、開口部、寸法等を正確に記入してください。

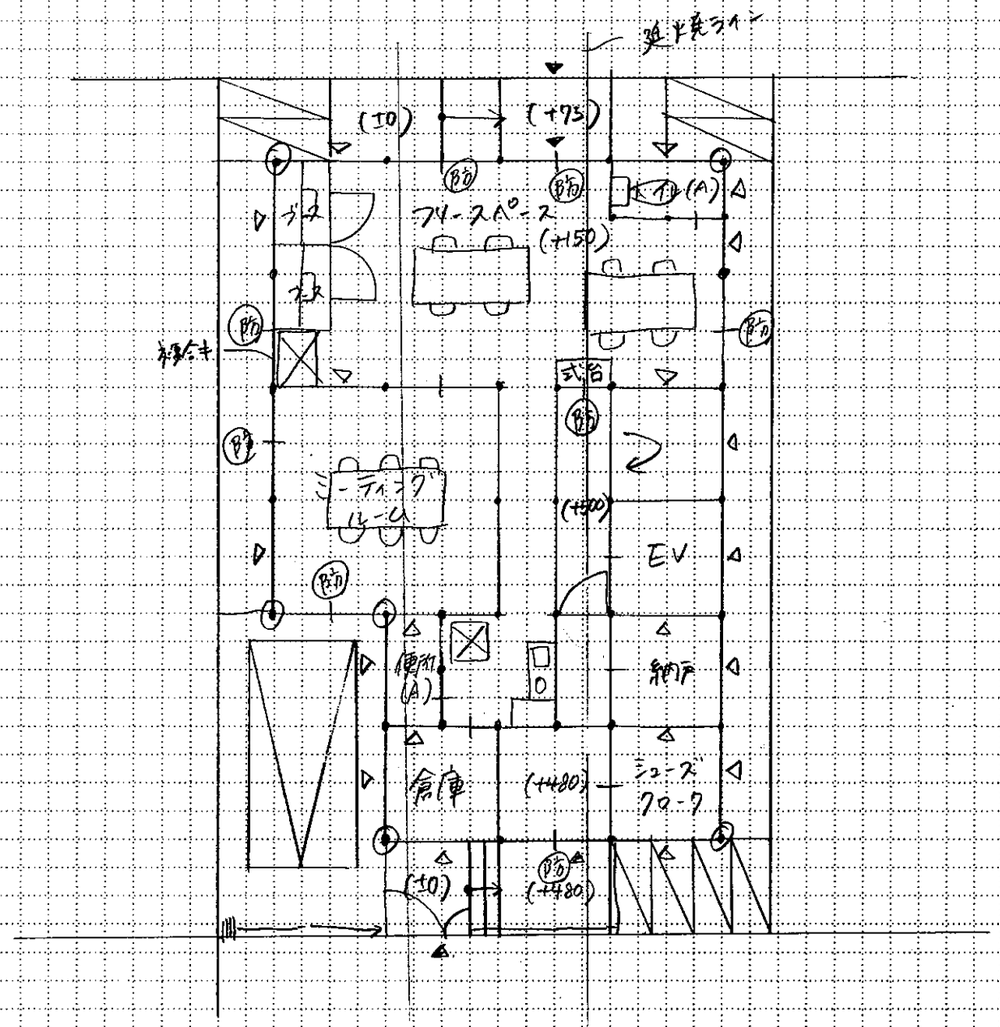

「２階平面プラン」を記入してください。（縮尺1／100）

(注)不正確な内容では、皆さんのプランを正しく評価できません。屋根、庇、室名、柱、開口部、寸法等を正確に記入してください。

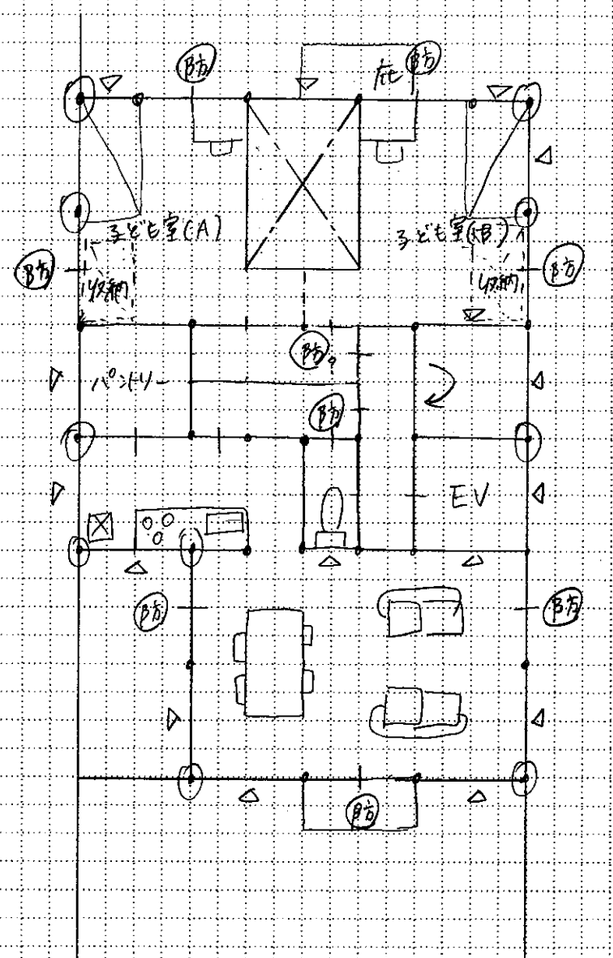

※全て延焼のおそれのある範囲


校名	池袋校	学生番号	－ －	受験番号	2F － 21595N	氏名	橋本 文恵

2026年度 2級建築士 プラン復元用紙 〔2/2〕（本試験プランを丁寧に記入しましょう。）

日建学院

「3階平面プラン」を記入してください。（縮尺1／100）

(注)不正確な内容では、皆さんのプランを正しく評価できません。屋根、庇、室名、柱、開口部、寸法等を正確に記入してください。

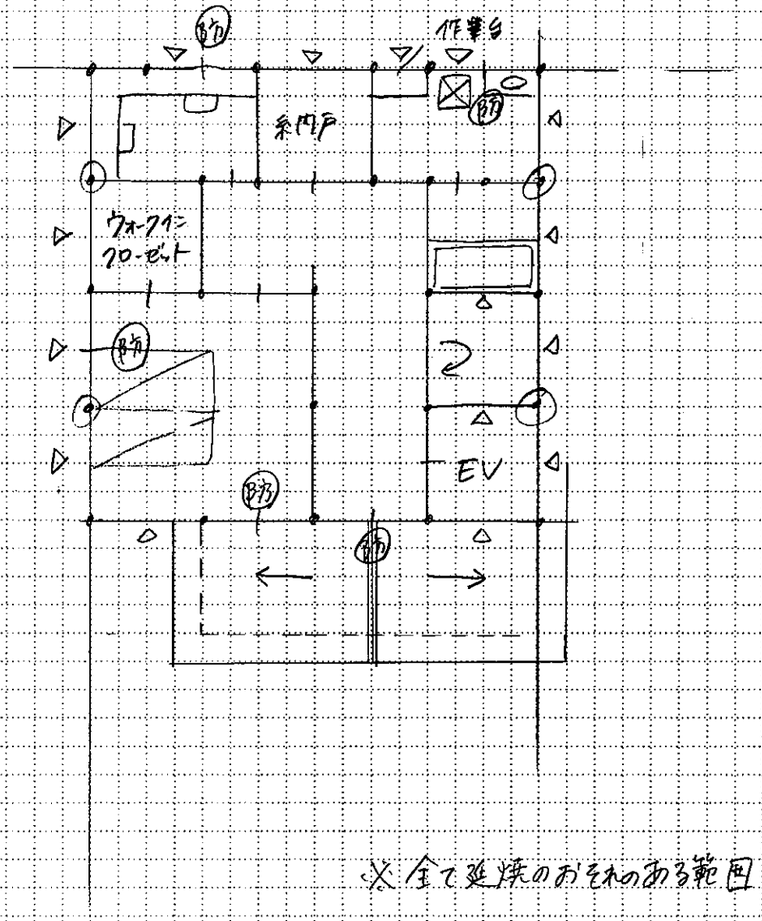

※全て延焼のおそれのある範囲

氏名 池袋校 梅本文恵

「計画の要点等の回答」を記入してください。

設問①：コワーキングスペース部分で一番気軽に利用できるフリースペースの部分を広く道路に面して配置した。また、住宅部分は出入口を設けて仕切ることでプライバシーを確保した。

設問②：吹抜を子ども室の中央に配置し、下の様子を見られるようにした。また、子ども室をコワーキングスペース部分のある北側に配置し、将来コワーキングスペース部分としても使用できるようにした。

設問③：主要構造物に必要な防火性能の有するものとし、延焼のおそれのある範囲の開口部、軒裏は、防火設備・防火性能の有するものとした。

「面積表」を記入してください。（※印は出題された場合に記入してください）

敷地面積			126.00 ㎡	
建築面積		(計算式) (7.28×7.28)+(5.46×3.64)	72.87 ㎡	
床面積	1階	(計算式) (7.28×7.28)+(5.46×3.64)	72.87 ㎡	
	2階	(計算式) (7.28×7.28)+(5.46×3.64)−(1.82×2.73)	67.90 ㎡	
	3階	(計算式) 7.28×7.28	52.99 ㎡	
延べ面積			193.76 ㎡	
※建蔽率		建築面積 72.87 ／ 敷地面積 126 ㎡	57 %	
※容積率		延べ面積 193.76 ／ 敷地面積 126 ㎡	153 %	

「作業時間・見直しの有無など」を記入してください。

プランニング	80 分	プラン完成後の見直し ☑した □していない
記述・面積表	15 分	作業に要した時間は普段と比べてどうでしたか？ □短い ☑同じ □長い
平面図	100 分	作業に要した時間は普段と比べてどうでしたか？ □短い ☑同じ □長い
立面図	25 分	作業に要した時間は普段と比べてどうでしたか？ □短い □同じ ☑長い
伏図	35 分	作業に要した時間は普段と比べてどうでしたか？ □短い ☑同じ □長い
部分詳細図	25 分	作業に要した時間は普段と比べてどうでしたか？ □短い ☑同じ □長い
見直し・仕上げ	20 分	答案完成後の見直し ☑した □していない


「本試験を受験して気になる事」を記入してください。（例：○○の意味が分からなかった。）

子ども室の将来利用がよく分からなかった。（第3者がB階段とEV使用？）
建具の避難方向を考慮しなかった。
ほとんど入れてると思うが、柱の1,820ピッチを確認しなかったと思う。
住宅用の駐輪場の計画があまり良くなかった。
去年よりも比較的簡単だと思うので、書き上げてる人は多いと思う。

講師記入欄


「１階平面兼配置プラン」を記入してください。（縮尺1／100）

(注)不正確な内容では、皆さんのプランを正しく評価できません。敷地、屋外施設、室名、柱、開口部、寸法等を正確に記入してください。

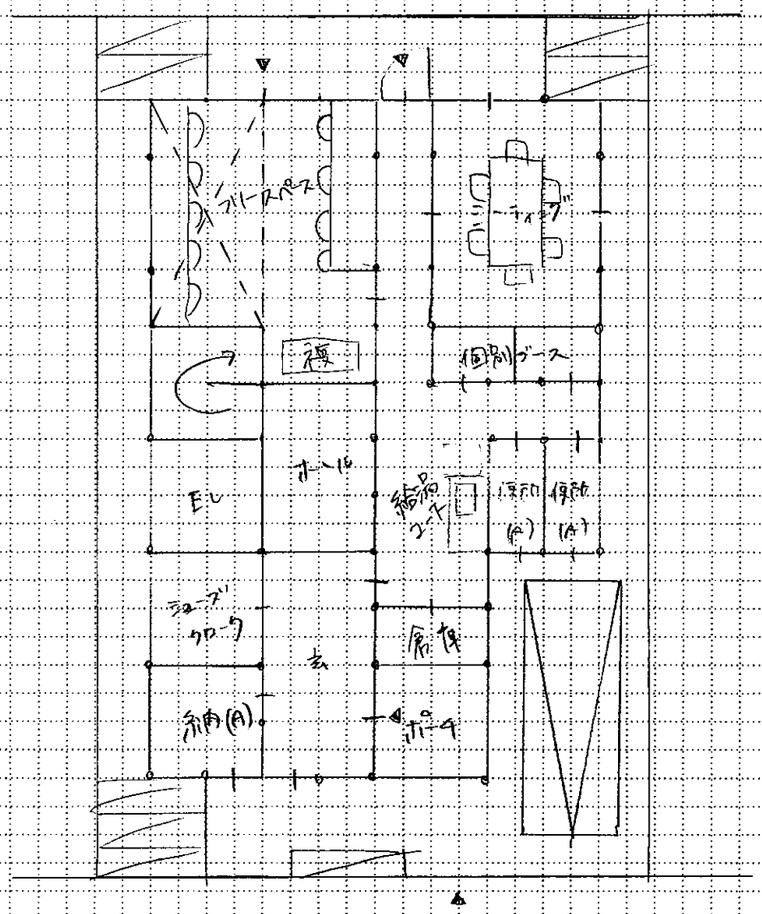

「２階平面プラン」を記入してください。（縮尺1／100）


(注)不正確な内容では、皆さんのプランを正しく評価できません。屋根、庇、室名、柱、開口部、寸法等を正確に記入してください。

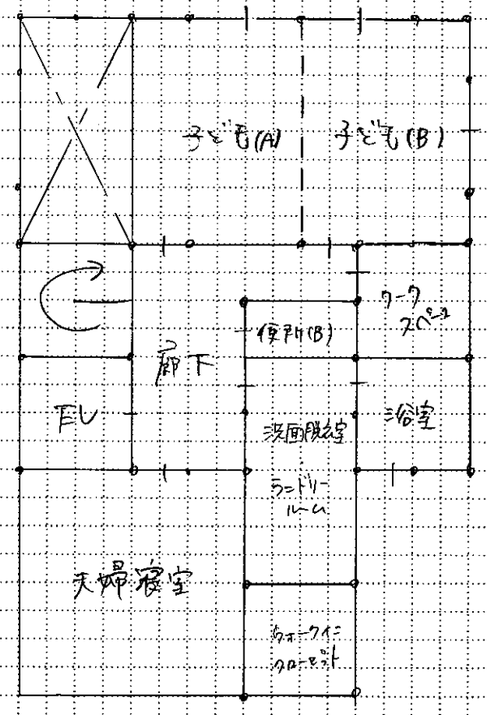

校名	二セ 姿	学生番号	－	－ 0123	受験番号	－	氏名	雨宮 玲彦

「３階平面プラン」を記入してください。（縮尺1／100）

(注)不正確な内容では、皆さんのプランを正しく評価できません。屋根、庇、室名、柱、開口部、寸法等を正確に記入してください。

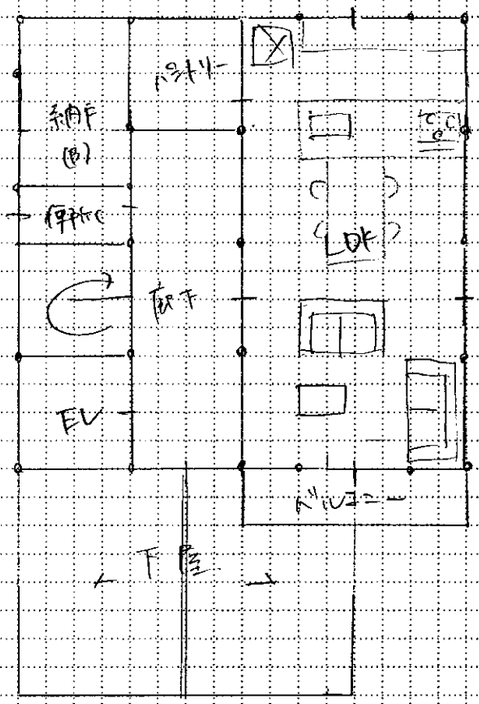

氏名　雨森 琥珀

「計画の要点等の回答」を記入してください。

設問①：

フリースペースにも出入口を設け、利用者が入りやすくなるよう工夫した。また、住宅と行き来する扉は利用者の少ない倉庫に近くとした。

設問②：

吹き抜けを端に配置することで子ども室をコワーキングスペースとしたときに、階段を設置できるように将来、住宅部分と完全に切り離せるよう工夫した。

設問③：

天井には強化石こうボード15㎜厚、壁には石こうボード15㎜厚、外壁にはガルバリウム鋼板を採用することで主要構造部が準耐火構造となるよう配慮した。

「面積表」を記入してください。（※印は出題された場合に記入してください）

敷地面積			126,00 ㎡
建築面積		(計算式) (7.28×7.28)+(5.86×3.64)	72,87 ㎡
床面積	1階	(計算式) (7.28×7.28)+(5.46×3.19)-(1.82×1.82)	69,56 ㎡
	2階	(計算式) (7.28×7.28)+(5.46×3.64)-(1.82×3.64)	66,24 ㎡
	3階	(計算式) 7.28×7.28	52,99 ㎡
延べ面積			188,79 ㎡
※建蔽率		建築面積 52,87 ／ 敷地面積 126 ㎡	57,8 %
※容積率		延べ面積 188,79 ／ 敷地面積 126,00 ㎡	149,8 %

「作業時間・見直しの有無など」を記入してください。

プランニング	60 分	プラン完成後の見直し ☑した □していない
記述・面積表	15 分	作業に要した時間は普段と比べてどうでしたか？ □短い ☑同じ □長い
平面図	140 分	作業に要した時間は普段と比べてどうでしたか？ □短い ☑同じ □長い
立面図	20 分	作業に要した時間は普段と比べてどうでしたか？ □短い □同じ □長い
伏　図	25 分	作業に要した時間は普段と比べてどうでしたか？ ☑短い □同じ □長い
部分詳細図	? 分	作業に要した時間は普段と比べてどうでしたか？ □短い □同じ ☑長い
見直し・仕上げ	60 分	答案完成後の見直し ☑した □していない


「本試験を受験して気になる事」を記入してください。（例：○○の意味が分からなかった。）

部分詳細図（土間仕上げとか、窓以外でも切った場合のおてほん）

講師記入欄


「１階平面兼配置プラン」を記入してください。（縮尺1／100）

(注) 不正確な内容では、皆さんのプランを正しく評価できません。敷地、屋外施設、室名、柱、開口部、寸法等を正確に記入してください。

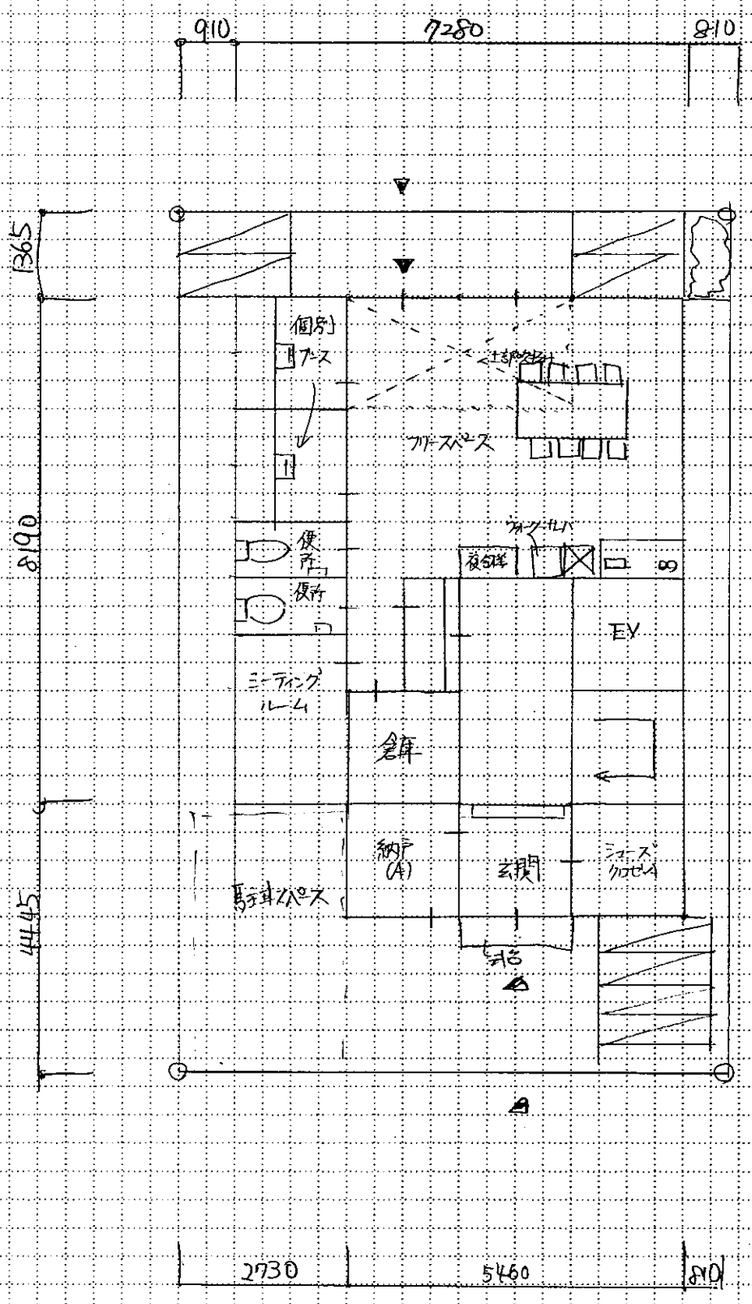

「２階平面プラン」を記入してください。（縮尺1／100）


(注) 不正確な内容では、皆さんのプランを正しく評価できません。屋根、庇、室名、柱、開口部、寸法等を正確に記入してください。

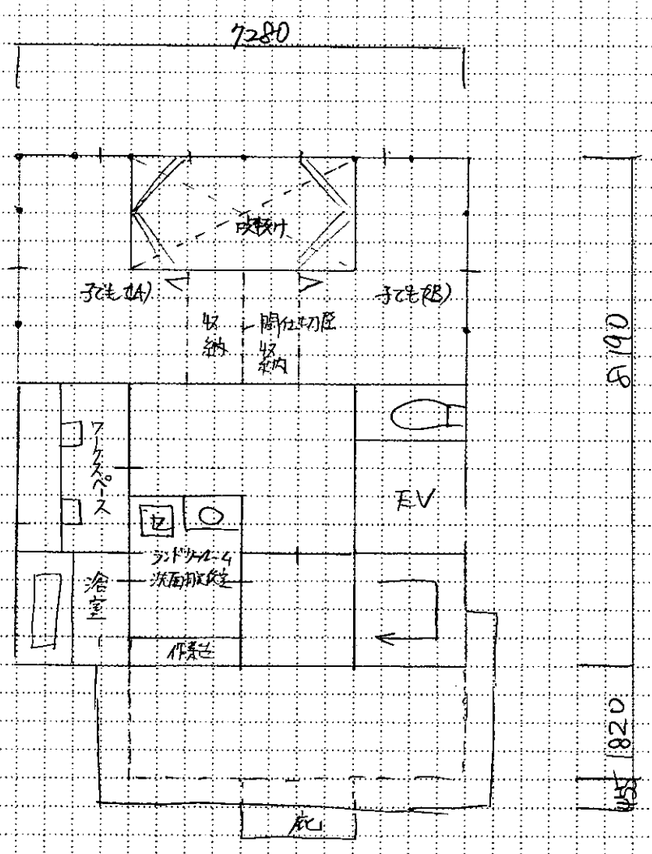

校名		学生番号	—	—	受験番号	—	氏名	松本 亮助

「３階平面プラン」を記入してください。（縮尺1／100）

(注)不正確な内容では、皆さんのプランを正しく評価できません。屋根、庇、室名、柱、開口部、寸法等を正確に記入してください。

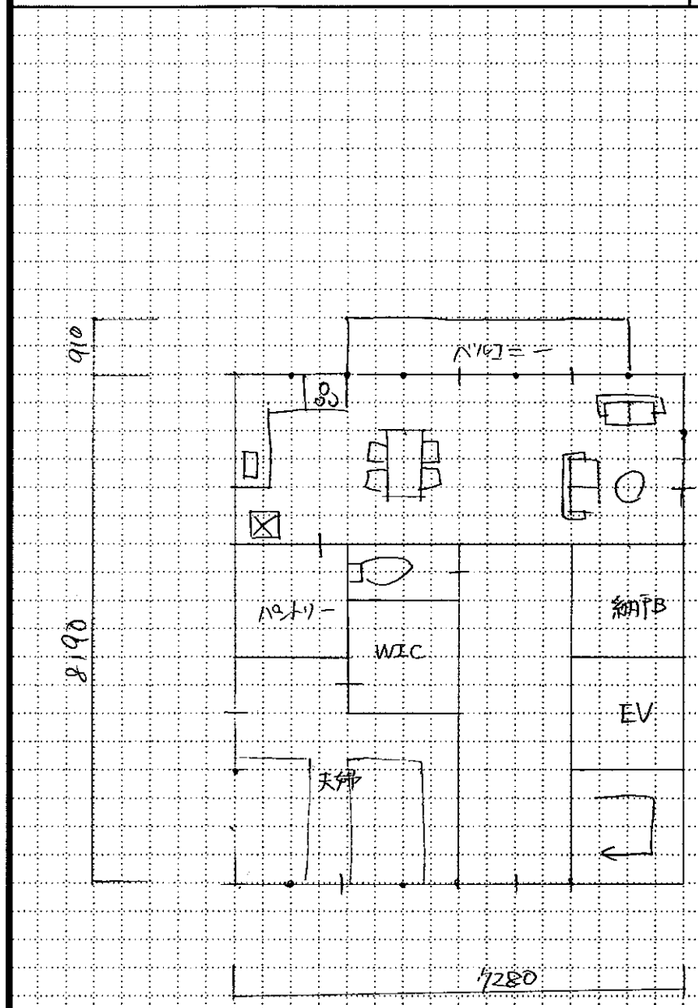

「計画の要点等の回答」を記入してください。

設問①：

コワーキングスペースは可能なかぎり北道路に寄せ、開口部を多く設けることで視認性を高め、わかりやすいよう工夫した。住宅部分の扉はカギ付とし、セキュリティを高めた。また扉をつ設けることで、より高めた。

設問②：

吹抜けは建物中央に計画することで、採光と通風が均等に得られるよう工夫した。また将来、コワーキングスペースとして活用する際に、隣の声が気にならないよう配慮した。

設問③：延焼のおそれのある開口部には防火設備を設けた。また、屋・柱・床・はり・屋根・階段は準耐火性能に対応する仕様とした。

「面積表」を記入してください。（※印は出題された場合に記入してください）

敷地面積		126.00 ㎡	
建築面積	(計算式) 7.28×8.19+5.46×1.82		69.56 ㎡
床面積 1階	(計算式) 7.28×8.19+5.46×1.82		69.56 ㎡
床面積 2階	(計算式) 7.28×8.19−1.82×3.64		52.99 ㎡
床面積 3階	(計算式) 7.28×8.19		59.62 ㎡
延べ面積			182.17 ㎡
※建蔽率	建築面積 69.56 ／ 敷地面積 126 ㎡		55.2 %
※容積率	延べ面積 182.17 ／ 敷地面積 126 ㎡		144.5%

「作業時間・見直しの有無など」を記入してください。

プランニング	90 分	プラン完成後の見直し ☑した □していない
記述・面積表	10 分	作業に要した時間は普段と比べてどうでしたか？ □短い ☑同じ □長い
平面図	90 分	作業に要した時間は普段と比べてどうでしたか？ □短い ☑同じ □長い
立面図	30 分	作業に要した時間は普段と比べてどうでしたか？ □短い ☑同じ □長い
伏　図	30 分	作業に要した時間は普段と比べてどうでしたか？ □短い ☑同じ □長い
部分詳細図	30 分	作業に要した時間は普段と比べてどうでしたか？ □短い □同じ ☑長い
見直し・仕上げ	20 分	答案完成後の見直し ☑した □していない

「本試験を受験して気になる事」を記入してください。（例：○○の意味が分からなかった。）

・移動可能な相月がよくイメージできなかった。


・

講師記入欄

氏名 松本 尚助


「１階平面兼配置プラン」を記入してください。（縮尺1／100）

(注)不正確な内容では、皆さんのプランを正しく評価できません。敷地、屋外施設、室名、柱、開口部、寸法等を正確に記入してください。

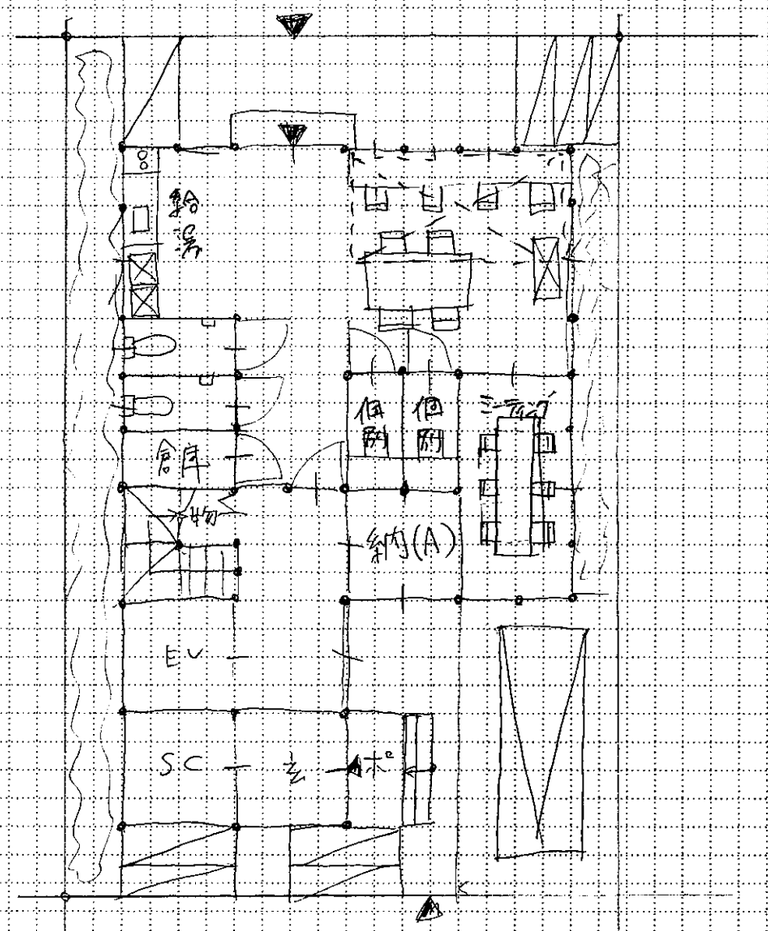

「２階平面プラン」を記入してください。（縮尺1／100）


(注)不正確な内容では、皆さんのプランを正しく評価できません。屋根、庇、室名、柱、開口部、寸法等を正確に記入してください。

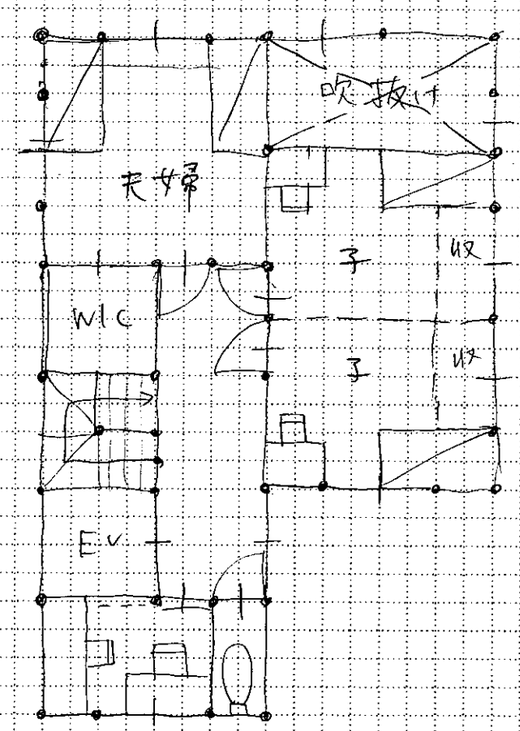

校名	池袋	学生番号	—	—	受験番号	—	氏名	田:愛 有馬

「３階平面プラン」を記入してください。（縮尺1／100）

（注）不正確な内容では、皆さんのプランを正しく評価できません。屋根、庇、室名、柱、開口部、寸法等を正確に記入してください。

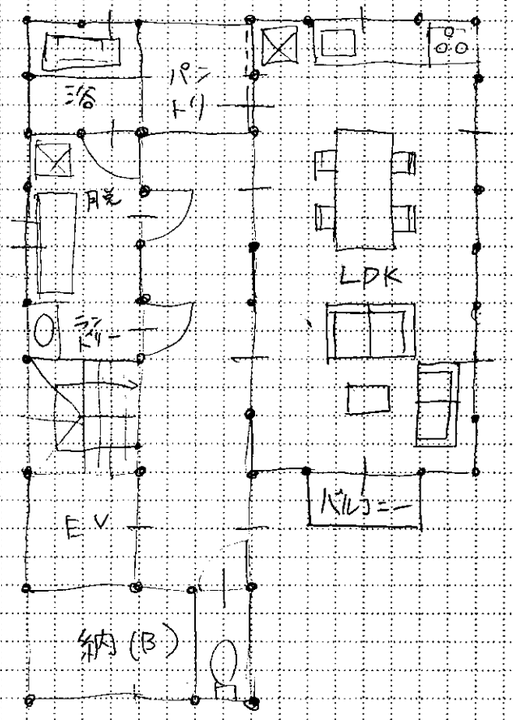

氏名　田辺　有哉

「計画の要点等の回答」を記入してください。

設問①：ユワーキングスペース部を商店が並ぶ北側道路、住宅部分を宅地が並ぶ南側道路に配置することで、プライバシーに配慮した。

設問②：子ども室Aと子ども室Bを隣接して計画し、将来1室で利用ができるよう間仕切壁にて仕切った。また、子ども室Aに吹抜けを隣接させ、吹抜けから2方向窓を設けることで、採光にも配慮した。

設問③：近隣商業地域に計画する建物のため、1階では道路中心線及び隣地境界線から3m、2・3階では3mの延焼ラインを超える開口部は防火仕様とした。また、建築物の主要構造部を準耐火仕様の材料を採用した。

「面積表」を記入してください。（※印は出題された場合に記入してください）

敷地面積			126.00	㎡
建築面積		（計算式）7.28×7.28+3.64+3.64	66.24	㎡
床面積	1階	（計算式）7.28×7.28+3.64×3.64	66.24	㎡
	2階	（計算式）7.28×7.28+3.64×3.64−3.64×1.82	59.62	㎡
	3階	（計算式）7.28×7.28+3.64×3.64	66.24	㎡
延べ面積			192.11	㎡
※建蔽率		建築面積 66.24 ／ 敷地面積 126 ㎡	52.57	%
※容積率		延べ面積 192.11 ／ 敷地面積 126 ㎡	152.46	%

「作業時間・見直しの有無など」を記入してください。


プランニング	40 分	プラン完成後の見直し ☑した ☐していない	
記述・面積表	20 分	作業に要した時間は普段と比べてどうでしたか？ ☐短い ☑同じ ☐長い	
平面図	90 分	作業に要した時間は普段と比べてどうでしたか？ ☑短い ☐同じ ☐長い	
立面図	20 分	作業に要した時間は普段と比べてどうでしたか？ ☐短い ☑同じ ☐長い	
伏　図	30 分	作業に要した時間は普段と比べてどうでしたか？ ☐短い ☑同じ ☐長い	
部分詳細図	40 分	作業に要した時間は普段と比べてどうでしたか？ ☐短い ☐同じ ☑長い	
見直し・仕上げ	60 分	答案完成後の見直し ☑した ☐していない	

「本試験を受験して気になる事」を記入してください。（例：○○の意味が分からなかった。）

講師記入欄


「１階平面兼配置プラン」を記入してください。（縮尺1／100）

(注)不正確な内容では、皆さんのプランを正しく評価できません。敷地、屋外施設、室名、柱、開口部、寸法等を正確に記入してください。

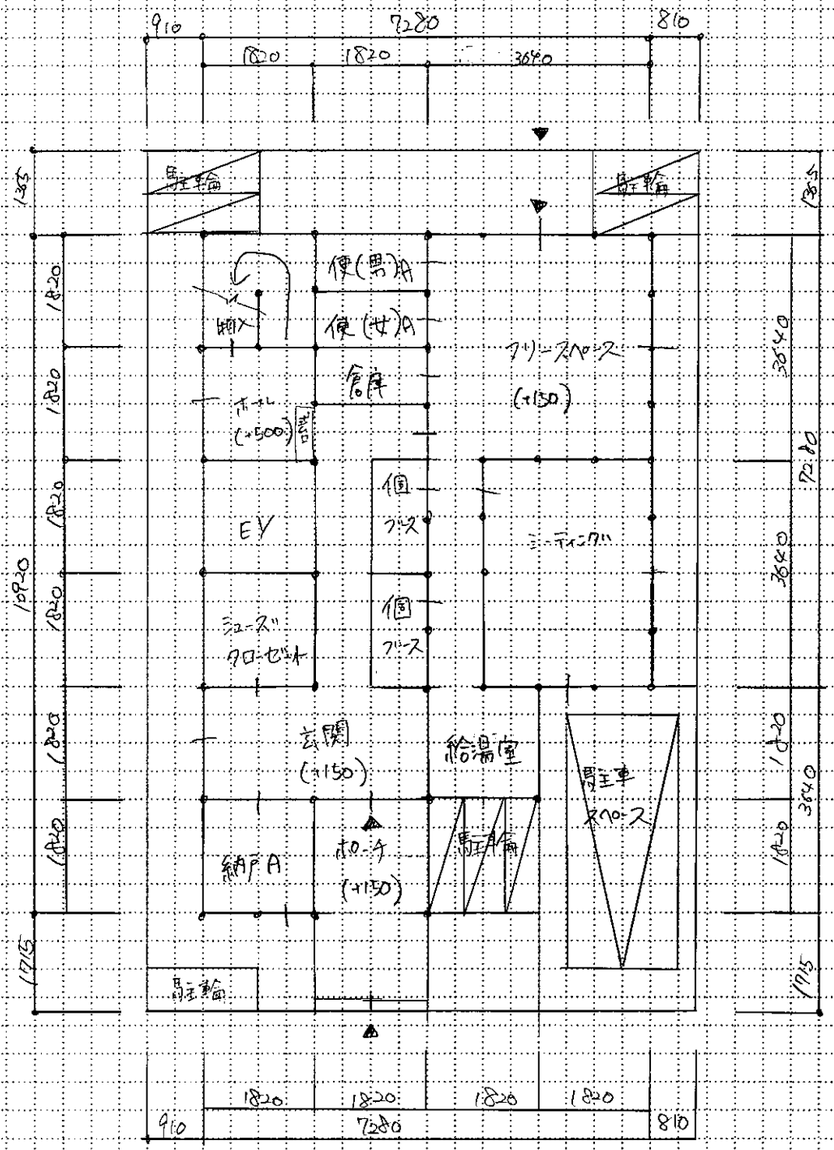

「２階平面プラン」を記入してください。（縮尺1／100）

(注)不正確な内容では、皆さんのプランを正しく評価できません。屋根、庇、室名、柱、開口部、寸法等を正確に記入してください。

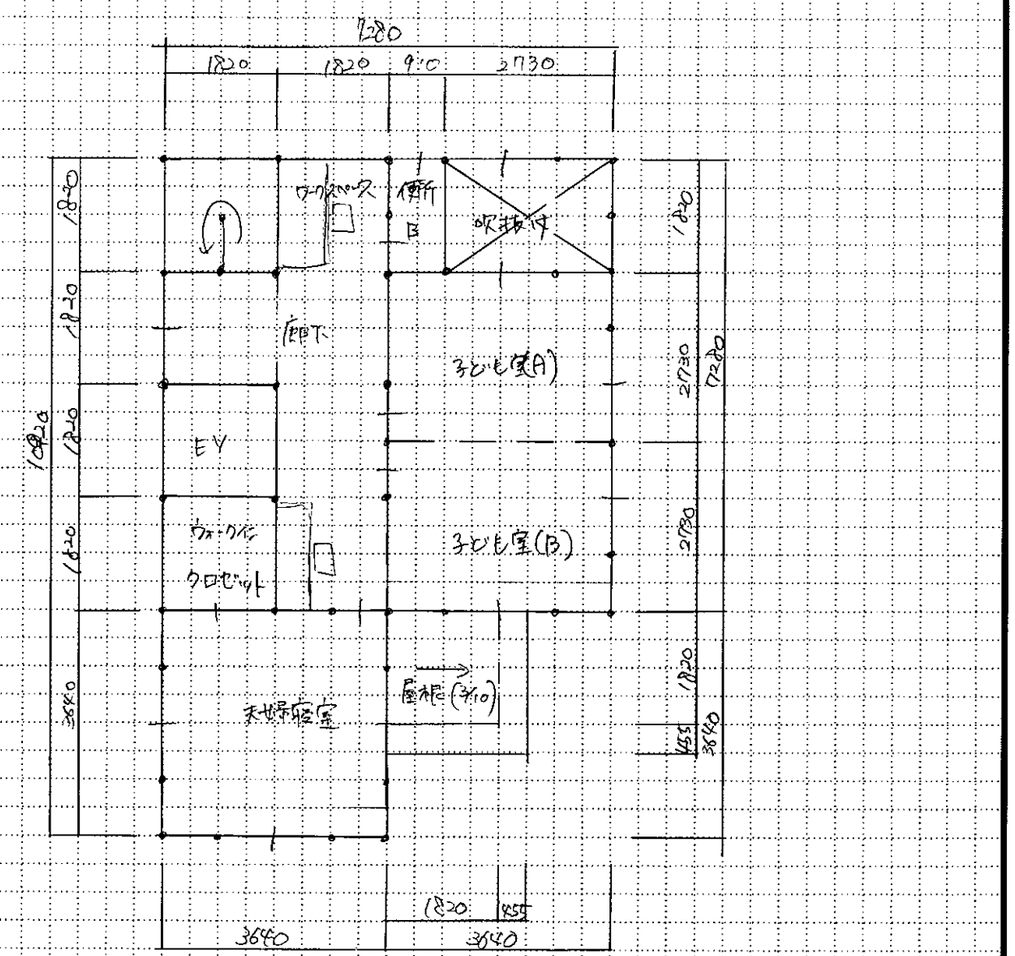


校名		学生番号	—	—	受験番号	—	氏名	石井 遥	①

２０２６年度 ２級建築士 プラン復元用紙 〔2/2〕（本試験プランを丁寧に記入しましょう。）

日建学院

「３階平面プラン」を記入してください。（縮尺1／100）

（注）不正確な内容では、皆さんのプランを正しく評価できません。屋根、庇、室名、柱、開口部、寸法等を正確に記入してください。

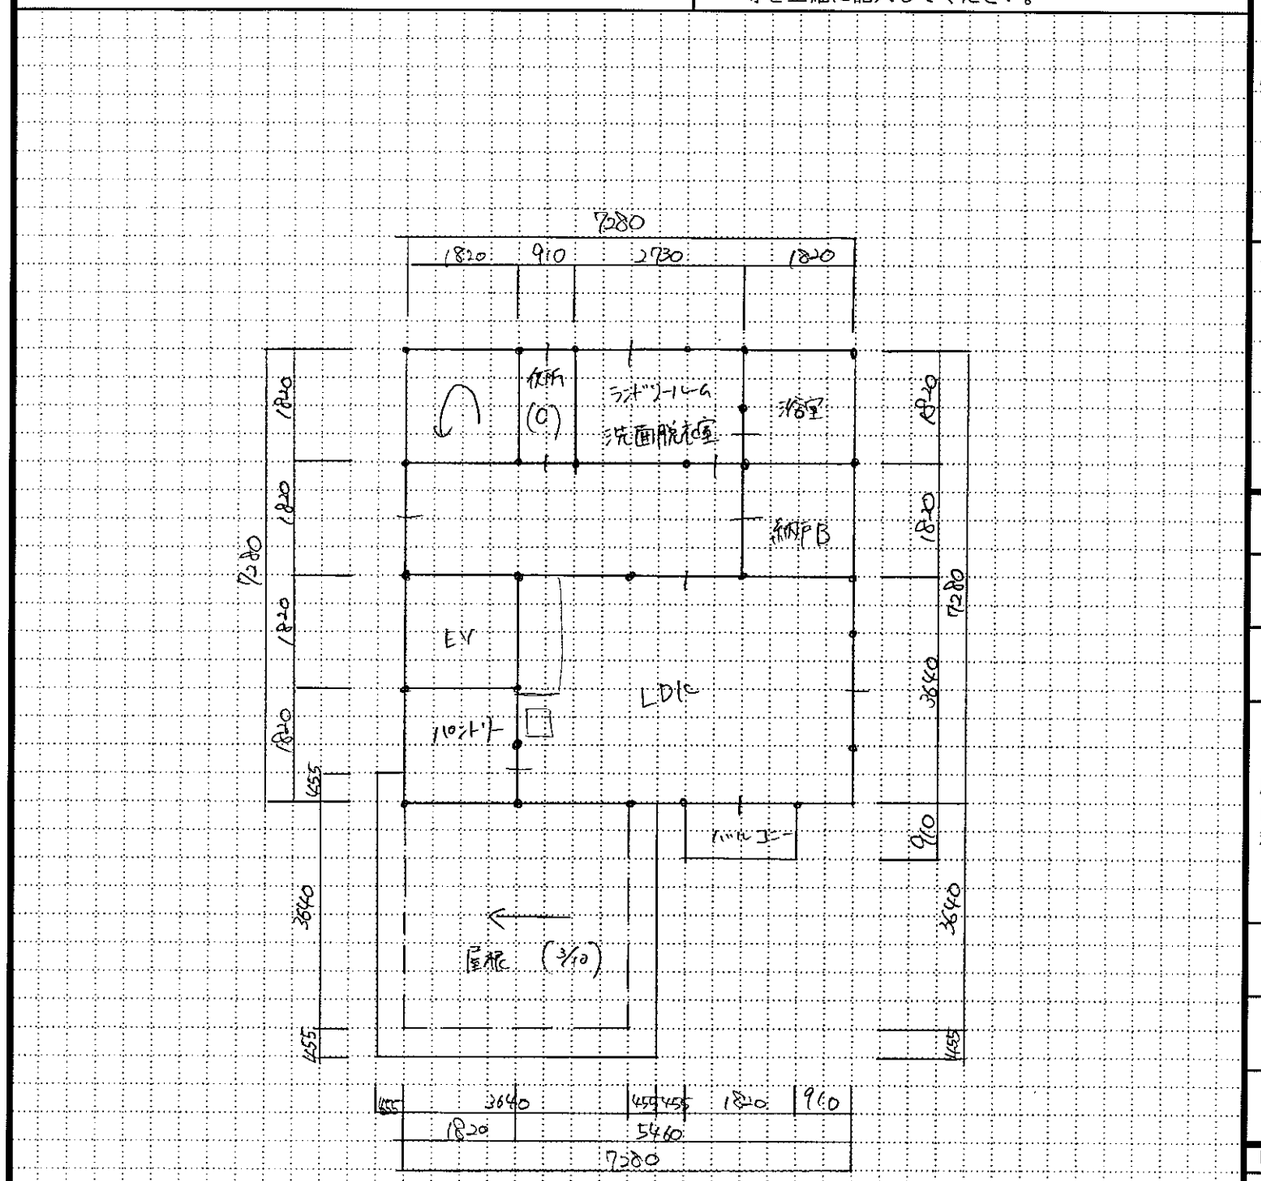

「計画の要点等の回答」を記入してください。

設問①：コワーキングスペース部分の出入口を北側に設け、住宅部分の出入口を南側に設けることで動線が交わらないようにした。建物と隣地境界線の間を植栽で埋めることで住宅部分のプライバシーに配慮した。

設問②：子ども室(A)と子ども室(B)の間の壁を間仕切壁とすることで将来のコワーキングスペースに対応できるよう工夫した。吹抜けを北東に設け窓を付けることで、子ども室(A)の採光を確保した。

設問③：壁、利用にくいスペースが不然とし、――

「面積表」を記入してください。（※印は出題された場合に記入してください）

敷地面積		126 ・ m²	
建築面積		(計算式) (7.28×7.28)+(3.64×3.64)+(1.82×1.80)	69.56 m²
床面積	1階	(計算式) (7.28×7.28)-(3.64×3.64)-(1.82×1.82)-(1.1×1.82)	61.27 m²
	2階	(計算式) (7.28×7.28)+(3.64×3.64)	61.27 m²
	3階	(計算式) 7.28×7.28	52.99 m²
延べ面積		180.5 m²	
※建蔽率		建築面積 69.56 ／ 敷地面積 126 m²	55 %
※容積率		延べ面積 180.5 ／ 敷地面積 126 m²	143.25 %

「作業時間・見直しの有無など」を記入してください。

プランニング	100 分	プラン完成後の見直し ☑した ☐していない
記述・面積表	10 分	作業に要した時間は普段と比べてどうでしたか？ ☐短い ☐同じ ☑長い
平面図	分	作業に要した時間は普段と比べてどうでしたか？ ☐短い ☐同じ ☐長い
立面図	分	作業に要した時間は普段と比べてどうでしたか？ ☐短い ☑同じ ☐長い
伏図	分	作業に要した時間は普段と比べてどうでしたか？ ☑短い ☐同じ ☐長い
部分詳細図	↓ 15:30 分	作業に要した時間は普段と比べてどうでしたか？ ☐短い ☐同じ ☑長い
見直し・仕上げ	25 分	答案完成後の見直し ☑した ☐していない


「本試験を受験して気になる事」を記入してください。（例：○○の意味が分からなかった。）

講師記入欄

氏名 石井 遥


「１階平面兼配置プラン」を記入してください。（縮尺1／100）

(注)不正確な内容では、皆さんのプランを正しく評価できません。敷地、屋外施設、室名、柱、開口部、寸法等を正確に記入してください。

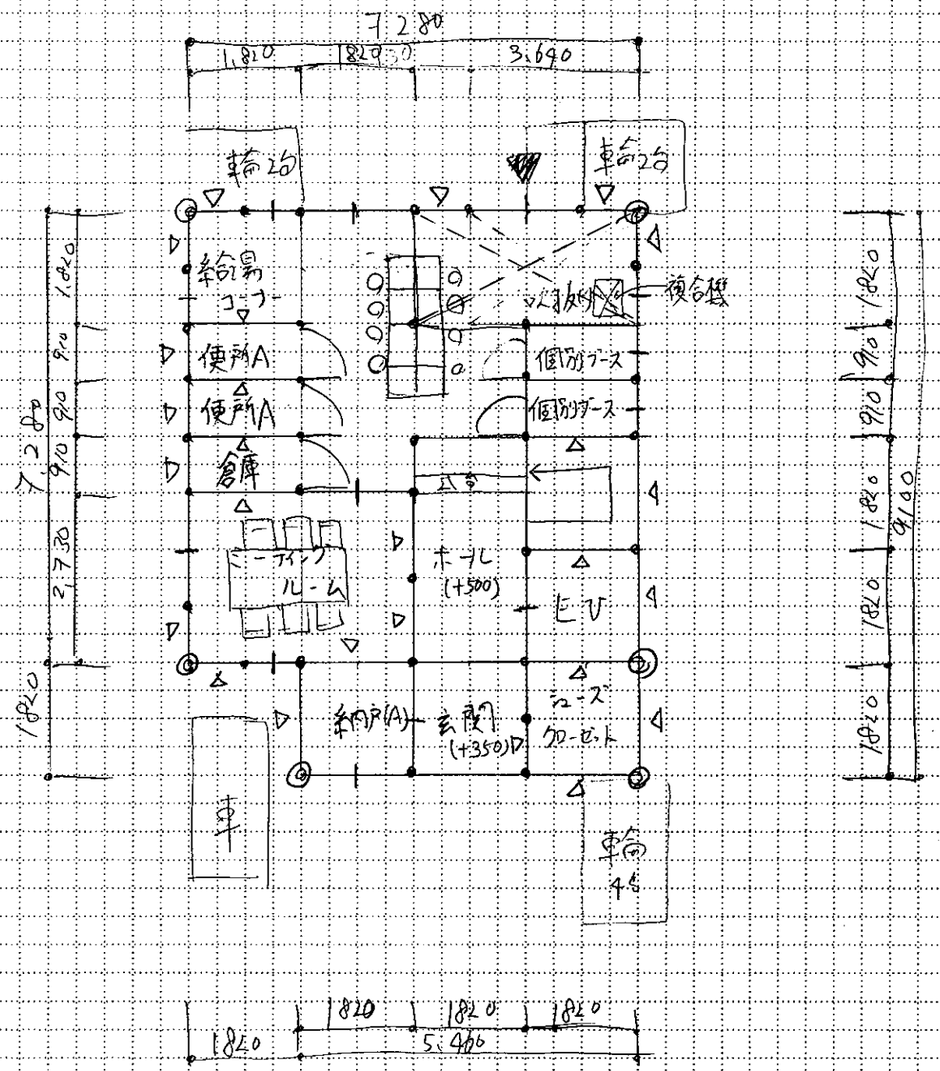

「２階平面プラン」を記入してください。（縮尺1／100）


(注)不正確な内容では、皆さんのプランを正しく評価できません。屋根、庇、室名、柱、開口部、寸法等を正確に記入してください。

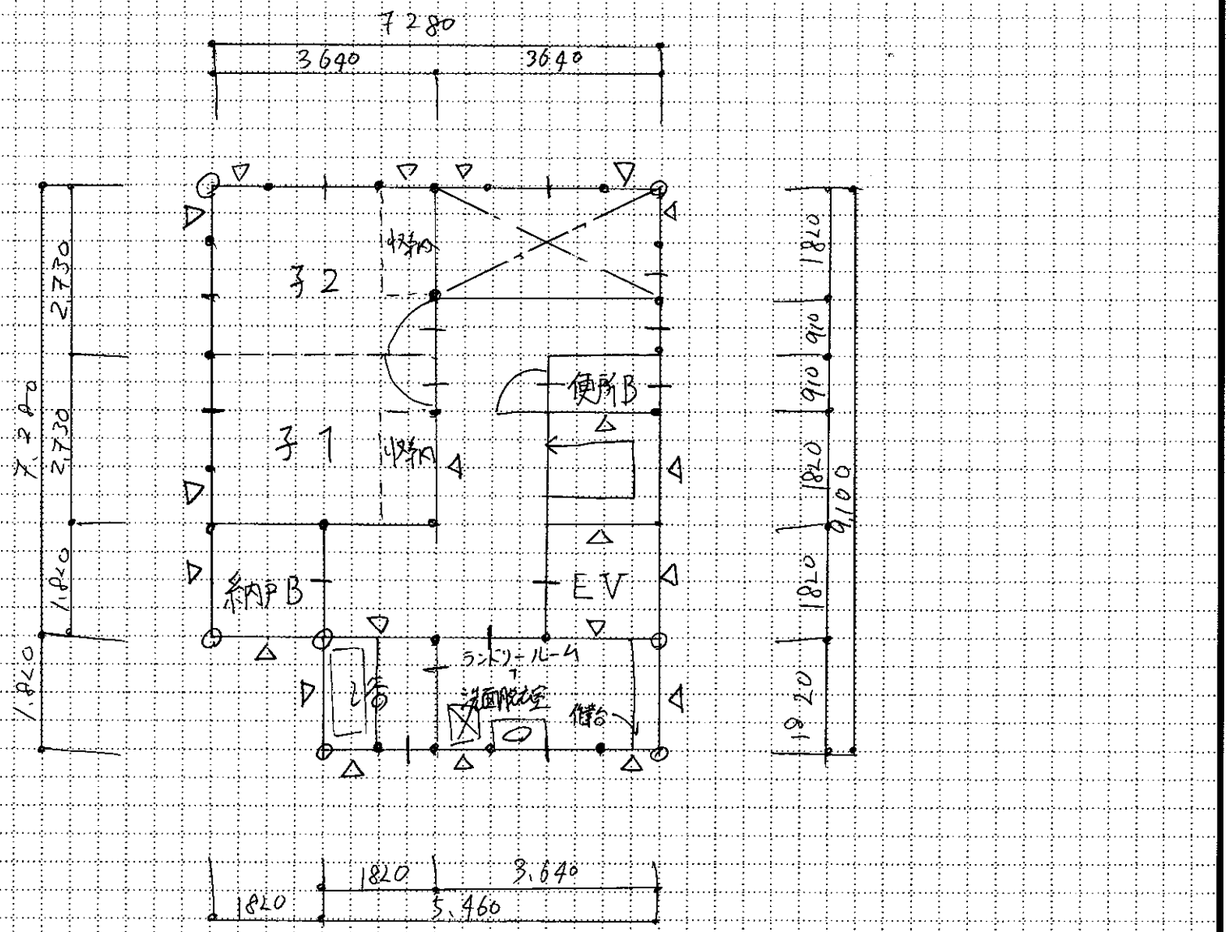

校名		学生番号	－	－	受験番号	2F － 20072Y	氏名	永島 友樹	①

「３階平面プラン」を記入してください。（縮尺1／100）

(注)不正確な内容では、皆さんのプランを正しく評価できません。屋根、庇、室名、柱、開口部、寸法等を正確に記入してください。

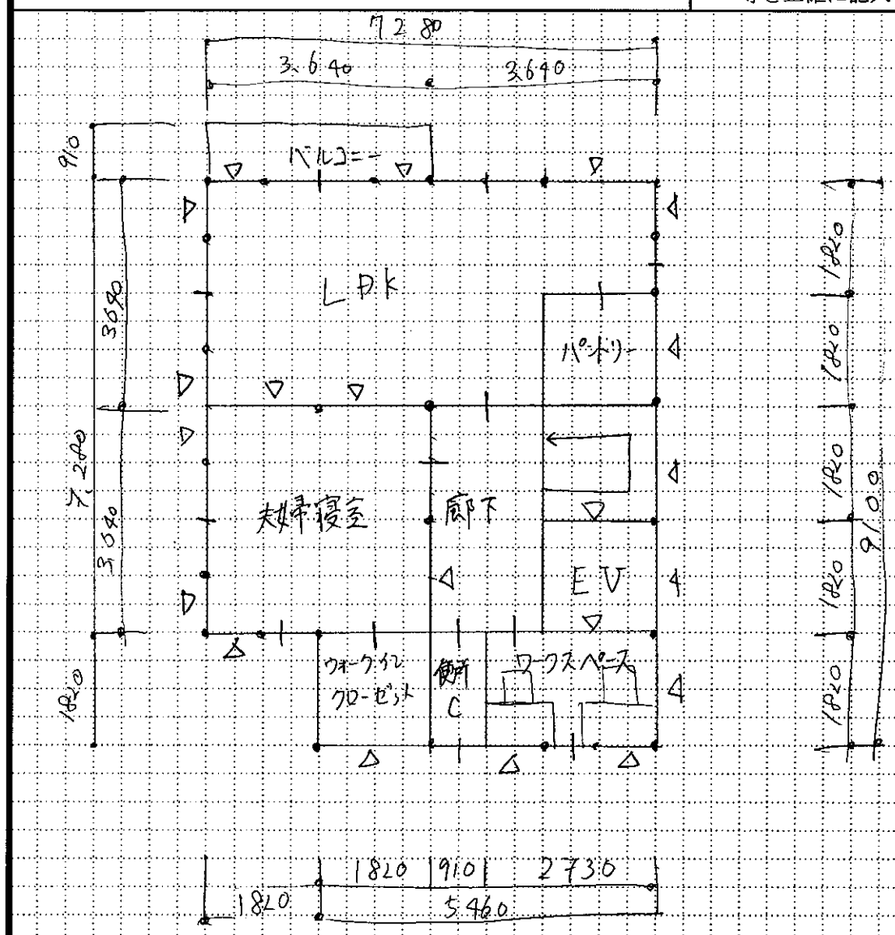

「計画の要点等の回答」を記入してください。

設問①：北面にコワーキングスペースのアプローチを設け、かつなるべく開口を大きくし集客性を考慮した。また生涯使うであろうLDKと夫婦寝室を3階に設置することでセキュリティとプライバシーの確保を図った。

設問②：日照をとりにくい北側に配置することで、フリースペースや2階の採光を十分確保できるようにした。またうども室(A)と吹抜けを分ける壁には耐力壁を設けず壁を無くしても問題ないようにした。

設問③：天井には、強化石コウボードの厚さ15mmのものを用い、壁の石コウボードは、上階の軒高まで延ばすようにして準耐火構造に配慮した

「面積表」を記入してください。（※印は出題された場合に記入してください）

敷地面積			126	m²
建築面積		(計算式) (7.28×7.28)+(5.46×1.82)	62.93	m²
床面積	1階	(計算式) (7.28×7.28)+(5.46×1.82)	62.93	m²
	2階	(計算式) (7.28×7.28)+(5.46×1.82)-(3.64×1.82)	56.31	m²
	3階	(計算式) (7.28×7.28)+(5.46×1.82)	62.93	m²
延べ面積			182.17	m²
※建蔽率		建築面積 62.93 ／ 敷地面積 126 m²	49.94	%
※容積率		延べ面積 182.17 ／ 敷地面積 126 m²	144.57	%

「作業時間・見直しの有無など」を記入してください。

プランニング	60 分	プラン完成後の見直し ☑した ☐していない
記述・面積表	15 分	作業に要した時間は普段と比べてどうでしたか？ ☐短い ☑同じ ☐長い
平面図	120 分	作業に要した時間は普段と比べてどうでしたか？ ☐短い ☑同じ ☐長い
立面図	20 分	作業に要した時間は普段と比べてどうでしたか？ ☑短い ☐同じ ☐長い
伏　図	20 分	作業に要した時間は普段と比べてどうでしたか？ ☐短い ☑同じ ☐長い
部分詳細図	30 分	作業に要した時間は普段と比べてどうでしたか？ ☐短い ☐同じ ☑長い
見直し・仕上げ	45 分	答案完成後の見直し ☐した ☐していない

「本試験を受験して気になる事」を記入してください。（例：○○の意味が分からなかった。）


講師記入欄

氏名 永島 友樹

日建学院


「１階平面兼配置プラン」を記入してください。（縮尺1／100）

(注)不正確な内容では、皆さんのプランを正しく評価できません。敷地、屋外施設、室名、柱、開口部、寸法等を正確に記入してください。

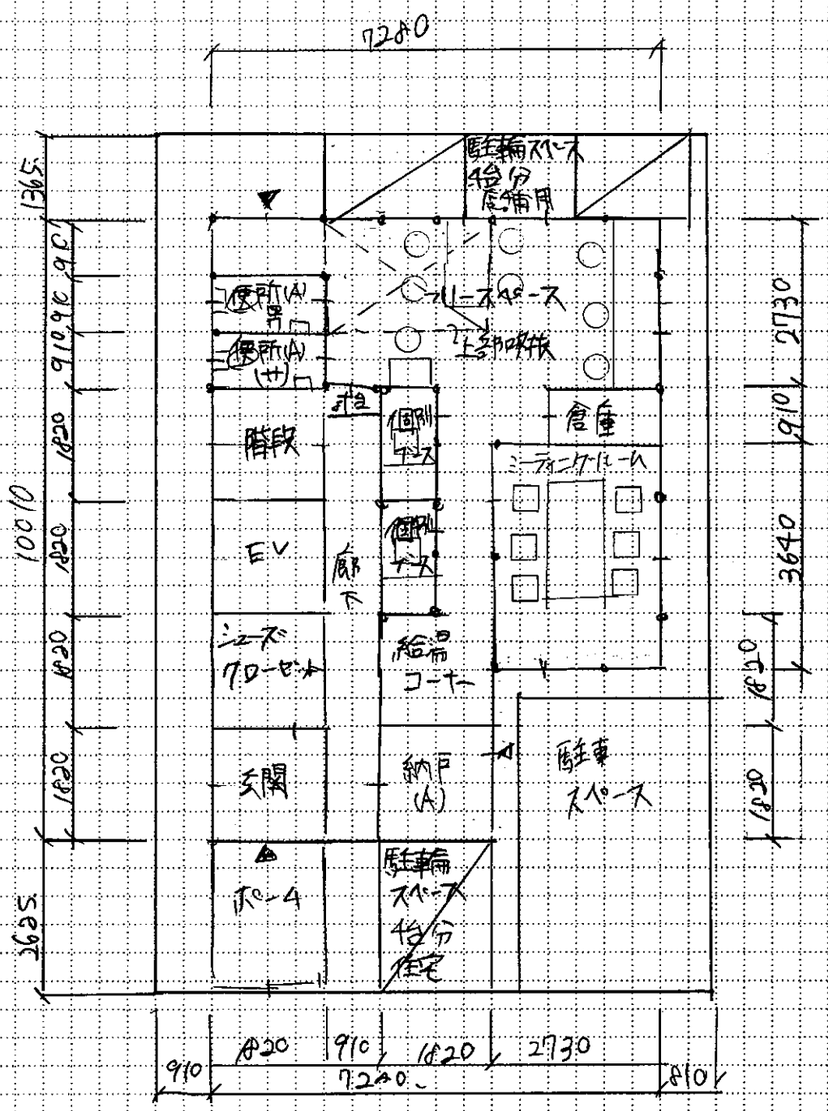

「２階平面プラン」を記入してください。（縮尺1／100）

(注)不正確な内容では、皆さんのプランを正しく評価できません。屋根、庇、室名、柱、開口部、寸法等を正確に記入してください。

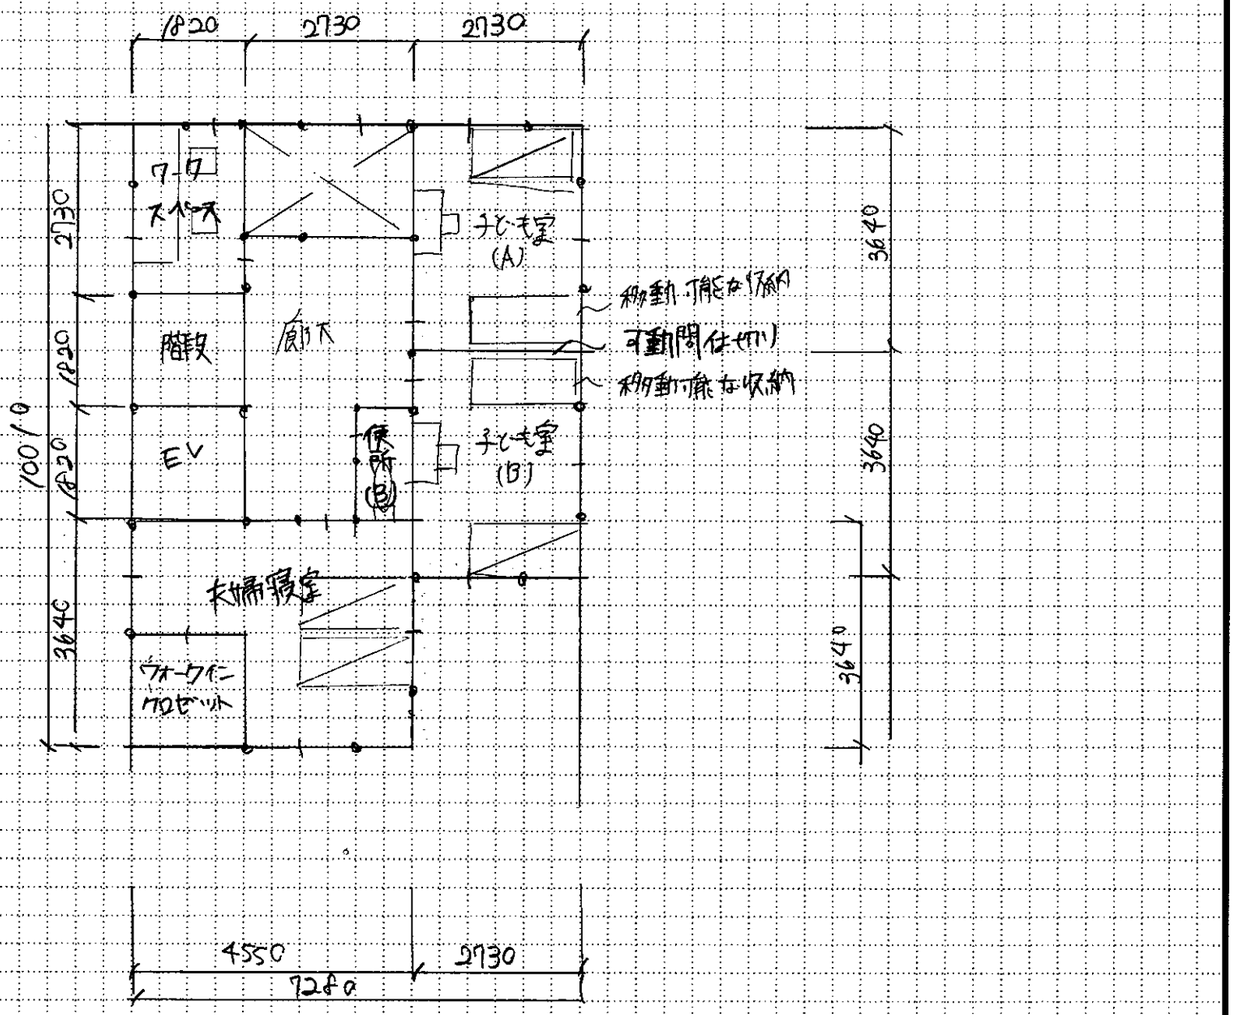


校名	池袋	学生番号	－ － ①	受験番号	－	氏名	板倉 史穂

２０２６年度 ２級建築士 プラン復元用紙 〔2/2〕（本試験プランを丁寧に記入しましょう。）

日建学院

「３階平面プラン」を記入してください。（縮尺1／100）

(注)不正確な内容では、皆さんのプランを正しく評価できません。屋根、庇、室名、柱、開口部、寸法等を正確に記入してください。

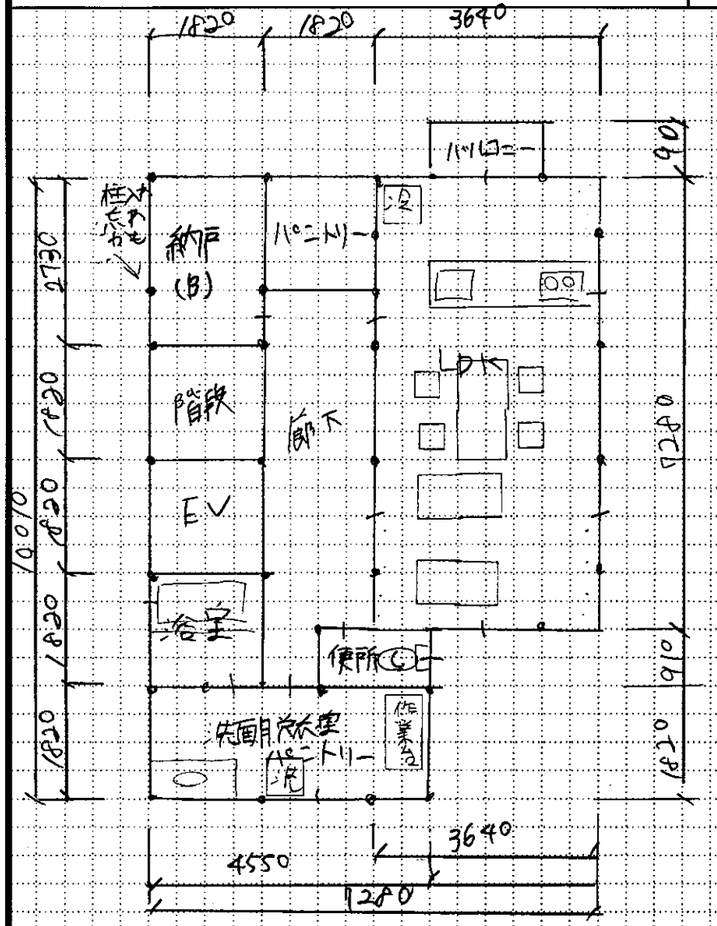

氏名 板倉 史緒

「計画の要点等の回答」を記入してください。

設問①：窓を大きく計画し、道路からの視認性を高めた。コワーキングスペースの出入口を南、住宅の出入口を南に明確にわけることでプライバシーに配慮。

設問②：将来、子どもの室をコワーキングスペースとして使用できるよう、北側のコワーキングスペースに寄せて計画した。

設問③：防水設備を計画し、避難できるように出入口、玄関を道路側に面して計画した。

「面積表」を記入してください。（※印は出題された場合に記入してください）

敷地面積		126.0 ㎡	
建築面積	(計算式) (9.28×7.28)+(4.55×2.73)	65.41 ㎡	
床面積	1階	(計算式) (9.28×7.28)+(4.55×2.73)	65.41 ㎡
	2階	(計算式) (9.28×7.28)+(4.55×2.73)−(2.73×1.82)	60.45 ㎡
	3階	(計算式) (9.28×7.28)+(4.55×2.73)	65.41 ㎡
延べ面積		191.27 ㎡	
※建蔽率	建築面積 65.41 ／ 敷地面積 126.0 ㎡	51.91 %	
※容積率	延べ面積 191.27 ／ 敷地面積 126.0 ㎡	151.80 %	

「作業時間・見直しの有無など」を記入してください。

プランニング	90 分	プラン完成後の見直し ☑した ☐していない
記述・面積表	15 分	作業に要した時間は普段と比べてどうでしたか？ ☐短い ☐同じ ☐長い
平面図	90 分	作業に要した時間は普段と比べてどうでしたか？ ☐短い ☑同じ ☐長い
立面図	20 分	作業に要した時間は普段と比べてどうでしたか？ ☐短い ☐同じ ☐長い
伏図	20 分	作業に要した時間は普段と比べてどうでしたか？ ☐短い ☐同じ ☐長い
部分詳細図	15 分	作業に要した時間は普段と比べてどうでしたか？ ☐短い ☐同じ ☐長い
見直し・仕上げ	50 分	答案完成後の見直し ☑した ☐していない

「本試験を受験して気になる事」を記入してください。（例：○○の意味が分からなかった。）


移動機能を収納、バルコニーの位置。
子ども室とエレベーター、階段の位置。
専用出入口はフリースペースと一体として計画してよかったのか
ウォーターサーバーの大きさ

講師記入欄

©


「１階平面兼配置プラン」を記入してください。（縮尺1／100）

(注)不正確な内容では、皆さんのプランを正しく評価できません。敷地、屋外施設、室名、柱、開口部、寸法等を正確に記入してください。

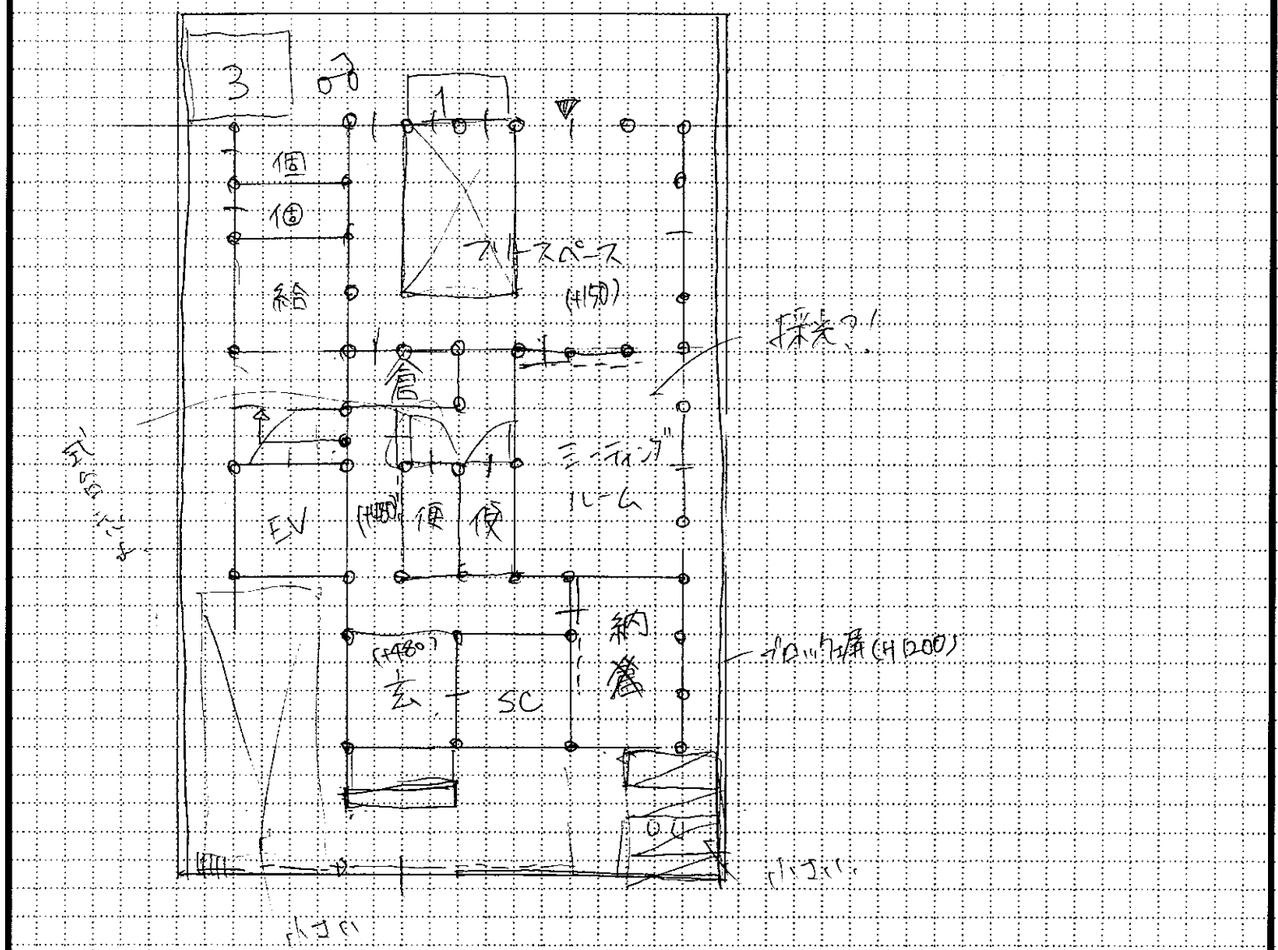

「２階平面プラン」を記入してください。（縮尺1／100）

(注)不正確な内容では、皆さんのプランを正しく評価できません。屋根、庇、室名、柱、開口部、寸法等を正確に記入してください。

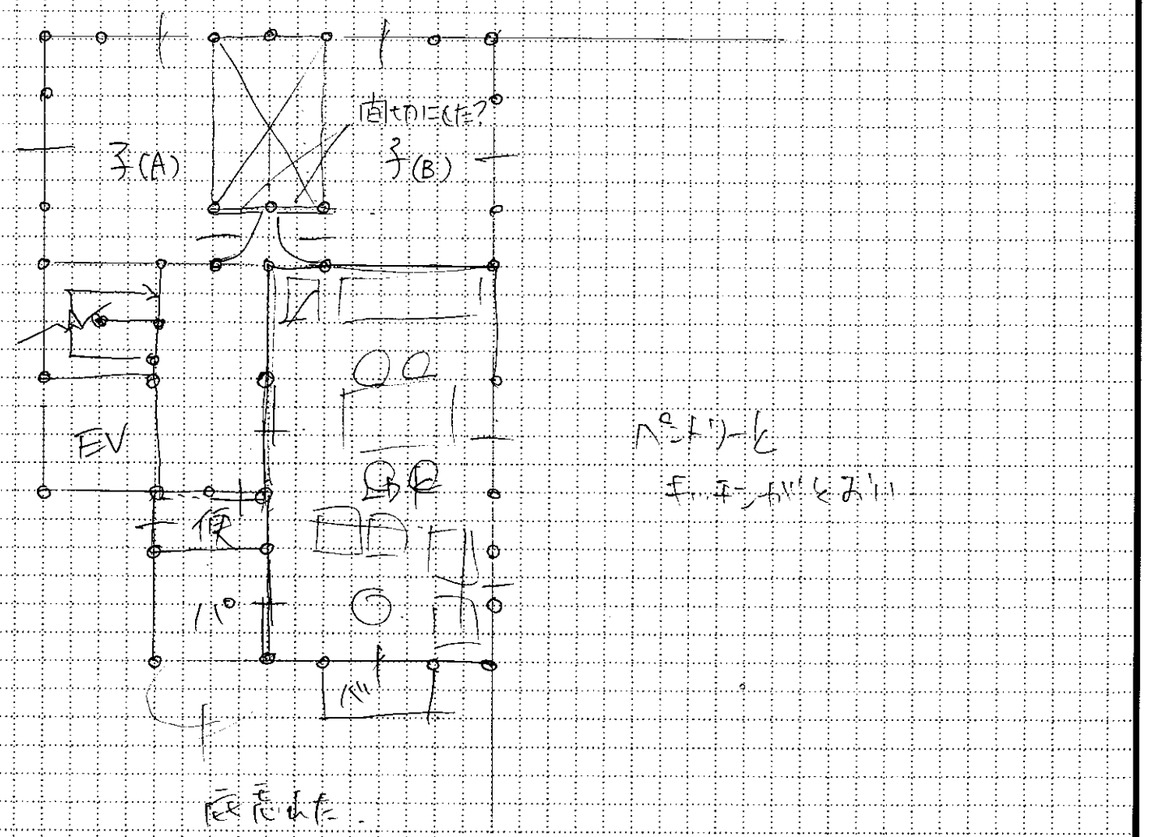


校名		学生番号		受験番号		氏名	酒井あずさ	①

２０２６年度 ２級建築士 プラン復元用紙 〔2/2〕（本試験プランを丁寧に記入しましょう。）

日建学院

「３階平面プラン」を記入してください。（縮尺1／100）

(注)不正確な内容では、皆さんのプランを正しく評価できません。屋根、庇、室名、柱、開口部、寸法等を正確に記入してください。

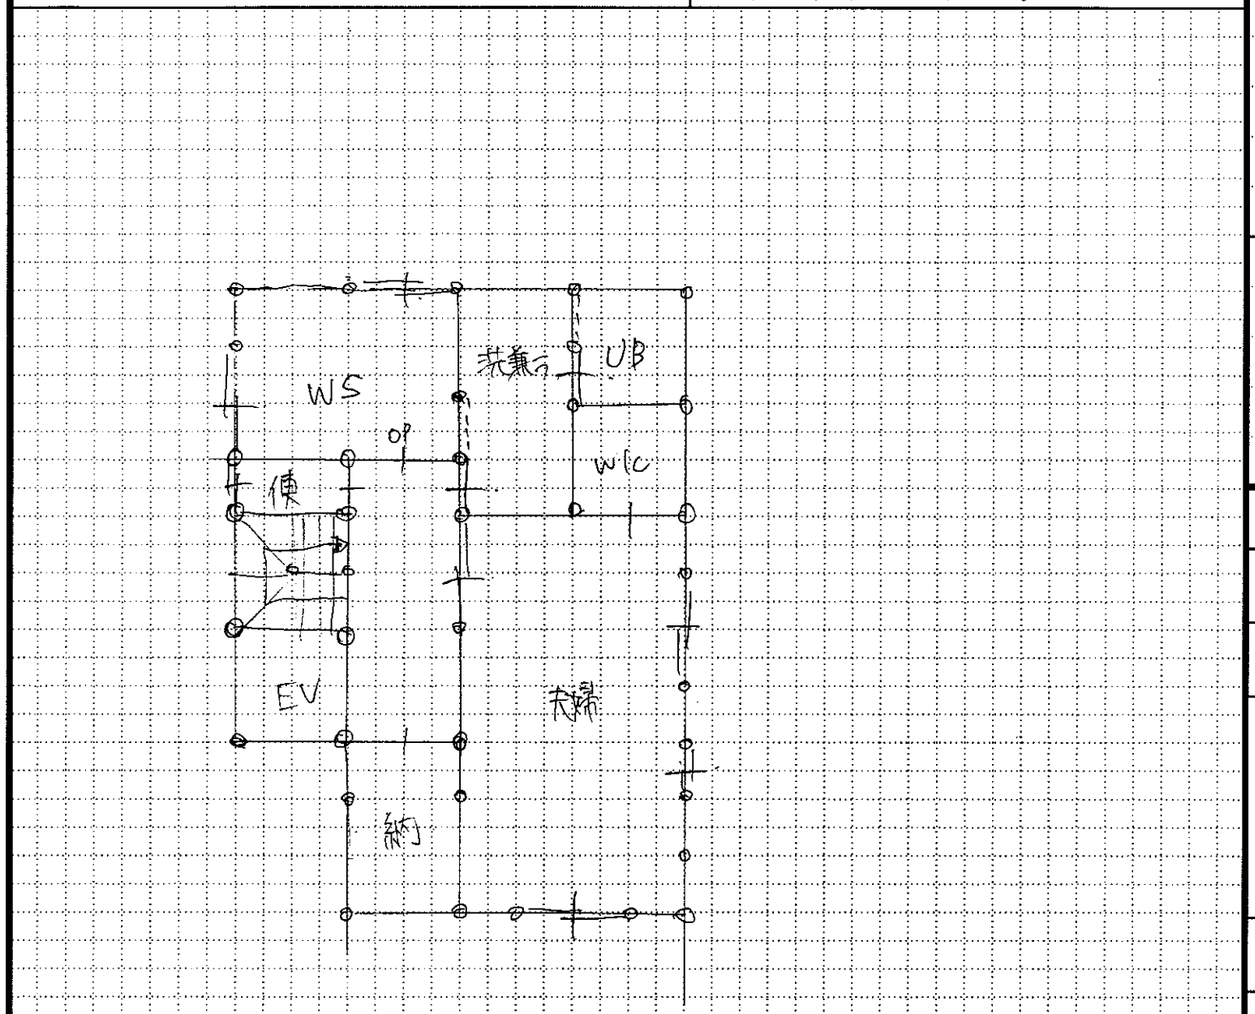

氏名 西井あずさ

「計画の要点等の回答」を記入してください。

設問①：北側にコワーキングスペースをもうけて開口を大きくとって中が見わすようにし、住宅とコワーキングスペースの宙のとびらにおさをつけた。

設問②：（最初の方覚えてないけど）（不正合かも）
将来階段として吹き抜けがつながることに配慮した。

設問③：延焼のおそれのあるところに防火設備をもうけた。住と住のあいだの扉は国金がちがうから防火設備にした。

「面積表」を記入してください。（※印は出題された場合に記入してください）

敷地面積		126.00 ㎡	
建築面積	(計算式) (7.28×7.28)+(2.73×5.46)	67.90 ㎡	
床面積	1F 2階 3F (計算式) (7.28×7.28)+(2.73×5.46)-(1.8×2.73)	54.174 ㎡	
	2階 1F (計算式) (7.28×7.28)+(2.73×5.46)	67.90 ㎡	
	3階 (計算式)	㎡	
延べ面積	なんか142.??って書いた… →	176.54 ㎡	
※建蔽率	建築面積 679／敷地面積 126 ㎡	53 %	
※容積率	延べ面積 1765.4／敷地面積 126 ㎡	140 %	

「作業時間・見直しの有無など」を記入してください。

プランニング	90 分	プラン完成後の見直し □した □していない
記述・面積表	20 分	作業に要した時間は普段と比べてどうでしたか？ □短い □同じ □長い
平面図	7 1 分	作業に要した時間は普段と比べてどうでしたか？ □短い □同じ □長い
立面図	10 分	作業に要した時間は普段と比べてどうでしたか？ □短い □同じ □長い
伏図	15 分	作業に要した時間は普段と比べてどうでしたか？ □短い □同じ □長い
部分詳細図	25 分	作業に要した時間は普段と比べてどうでしたか？ □短い □同じ □長い
見直し・仕上げ	? 分	答案完成後の見直し □した □していない

！ なんか時間わからん！

「本試験を受験して気になる事」を記入してください。（例：○○の意味が分からなかった。）

部分詳細がわからなかった（書いてはある）


見直しのとき（ラスト20分）で吹き抜けが階段と気がついた。

ガビーン。書きまってはいるけど。

講師記入欄


「１階平面兼配置プラン」を記入してください。（縮尺1／100）

(注)不正確な内容では、皆さんのプランを正しく評価できません。敷地、屋外施設、室名、柱、開口部、寸法等を正確に記入してください。

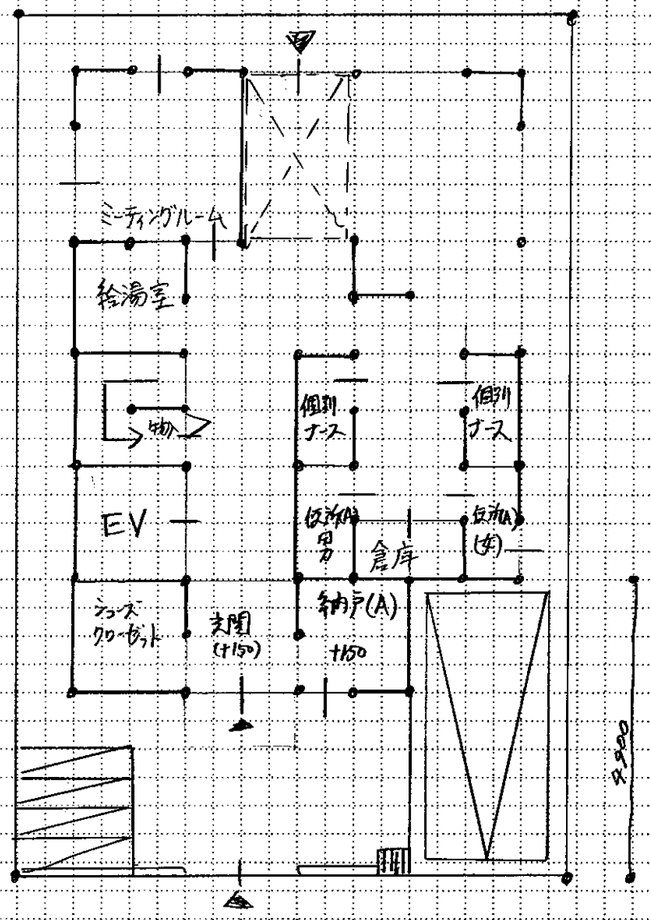

「２階平面プラン」を記入してください。（縮尺1／100）

(注)不正確な内容では、皆さんのプランを正しく評価できません。屋根、庇、室名、柱、開口部、寸法等を正確に記入してください。

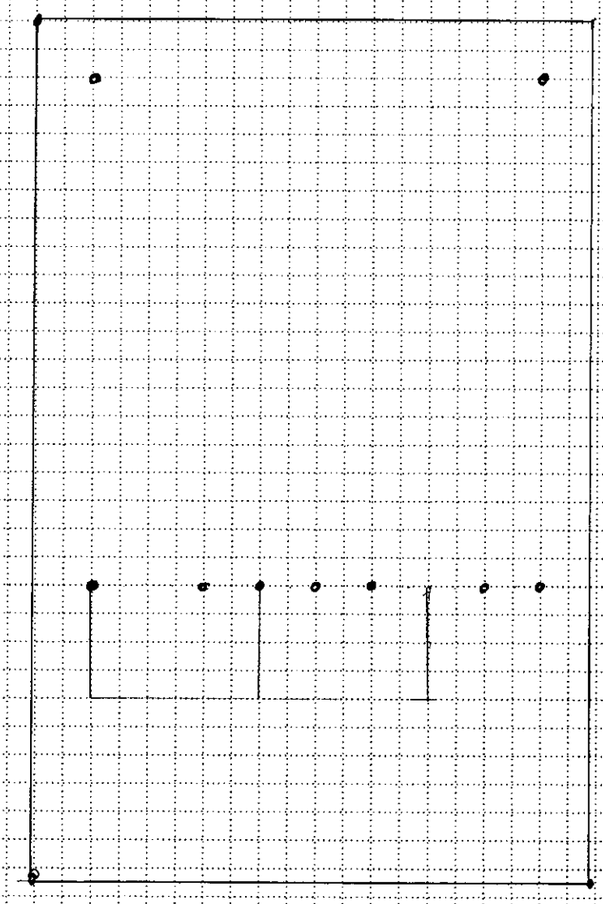


校名		学生番号		受験番号		氏名	池内 和生

日建学院

「３階平面プラン」を記入してください。（縮尺1／100）

(注)不正確な内容では、皆さんのプランを正しく評価できません。屋根、庇、室名、柱、開口部、寸法等を正確に記入してください。

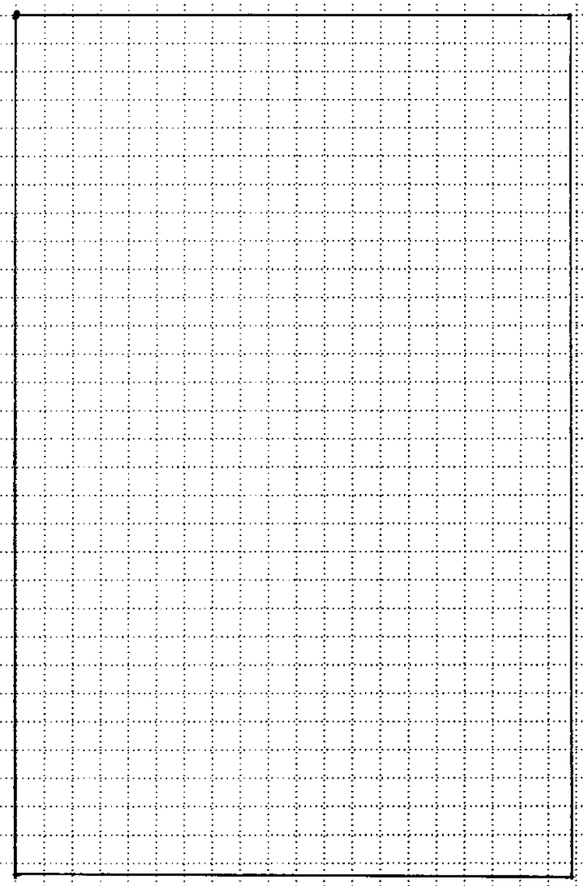

氏名 池内 和生

「計画の要点等の回答」を記入してください。

設問①：	設問②：
設問③：	

「面積表」を記入してください。（※印は出題された場合に記入してください）

敷地面積			㎡	
建築面積		(計算式)	㎡	
床面積	1階	(計算式)	㎡	
	2階	(計算式)	㎡	
	3階	(計算式)	㎡	
延べ面積			㎡	
※建蔽率		建築面積 ／ 敷地面積 ㎡	%	
※容積率		延べ面積 ／ 敷地面積 ㎡	%	

「作業時間・見直しの有無など」を記入してください。

プランニング	分	プラン完成後の見直し □した □していない
記述・面積表	分	作業に要した時間は 普段と比べてどうでしたか？ □ 短い □ 同じ □ 長い
平面図	分	作業に要した時間は 普段と比べてどうでしたか？ □ 短い □ 同じ □ 長い
立面図	分	作業に要した時間は 普段と比べてどうでしたか？ □ 短い □ 同じ □ 長い
伏 図	分	作業に要した時間は 普段と比べてどうでしたか？ □ 短い □ 同じ □ 長い
部分詳細図	分	作業に要した時間は 普段と比べてどうでしたか？ □ 短い □ 同じ □ 長い
見直し・仕上げ	分	答案完成後の見直し □した □していない

「本試験を受験して気になる事」を記入してください。（例：○○の意味が分からなかった。）

講師記入欄