設 計 課 題　「ホ テ ル」

Ⅰ. 設 計 条 件

高原のリゾート地域にあり、緑豊かで景観に優れた公園に隣接した敷地に、チャペルを併設したホテルを計画。

計画に当たっては、敷地内に建つ既存の２階建てチャペル(「既存部」)を残し、新しくホテル(「増築部」)を増築するほか、増築部と既存部とを接続し、一の建築物とするとともに、次のことが求められている。

(1) ホテル利用者(宿泊客、チャペル利用者、レストラン利用者)、従業員等の円滑な動線計画及びセキュリティの確保
(2) 増築部と既存部との接続部の安全性(エキスパンションジョイント、バリアフリー等)の確保
(3) 敷地内外の環境への配慮

1. 敷地及び周辺条件

(1) 敷地の形状、接道条件、周辺状況等は、「敷地図」のとおり。
(2) 敷地は平坦で、敷地と、道路の路面の中心、隣地及び道路の反対側の敷地には、高低差はない。また、歩道の切り開きは、２か所(１か所当たり６m)まで可能。
(3) 敷地及びその周辺は、近隣商業地域(道路高さ制限における斜線勾配は1.5、隣地高さ制限における斜線勾配は2.5。)及び準防火地域に指定。また、建蔽率の限度は80%(所定の加算を含む。)、容積率の限度は200%。これら以外に、地域、地区等及び特定行政庁による指定、許可等並びに日影による中高層の建築物の高さの制限はない。
(4) 電気、ガス及び上下水道は完備。
(5) 地盤は良好、杭打ちの必要はない。
(6) 気候は温暖、積雪について配慮はしなくてよい。また、水害の危険がない地域。

2. 建 築 物

(1) 増築部及び既存部は、１階及び２階の屋内で接続させて直接行き来できるように計画。なお、増築部と既存部が接続可能な位置は下書用紙にある「既存部平面図、屋根伏図、断面図」に示す位置とし、増築部及び既存部の条件は次のとおり。

項　目	増　築　部	既　存　部
構造・階数	・構造種別は自由、地上３階建ての耐火建築物。	・耐震スリットを用いた純ラーメン構造による鉄筋コンクリート造、地上２階建ての耐火建築物。
規模等	・既存部と合わせた建築面積及び床面積が、建蔽率及び容積率の限度を超えないものとする。	・建築面積は、166.25㎡。 ・床面積の合計は、218.25㎡(１階は157.50㎡、２階は60.75㎡)。 ・１階床高は、GL＋200㎜、２階床高は、GL＋4,500㎜。
その他	－	・建築設備は建築基準法の現行基準に適合し、空調設備及び電気設備は改修する必要はない。 ・構造は耐震改修が既に行われており、建築基準法の現行基準に適合し、柱と梁は、撤去してはならない。

(2) 増築部及び既存部は、「高齢者、障害者等の移動等の円滑化の促進に関する法律」に規定する「建築物移動等円滑化基準」に適合するものとする。ただし、主たる階段は「建築物移動等円滑化誘導基準」に適合するものとする。
(3) 要求室等は、右表のとおり。

3. その他の施設等


(1) 駐車場は、次のとおり計画。
　① 車椅子使用者用１台分、サービス用１台分のスペースを設ける。なお、建築物内に設けてもよい。
　② ホテルの利用者用、従業員用の駐車場は、敷地東側にある写真館が所有するローズガーデンの隣にあるホテル専用駐車場を利用。なお、歩行者はホテル専用駐車場からローズガーデン内の通路を通って自由にホテルの敷地にアクセスすることが可能。
(2) ホテルの利用者用の車寄せを設ける。雨天時の乗降に配慮し、車寄せには、屋根、庇等を設ける。
(3) 既存部の前庭での記念撮影や屋外イベントなどの利用に配慮し、外構(植栽、通路等)の計画を行う。

4. 留 意 事 項

(1) 既存部と増築部とは接続し、一の建築物とする。
(2) 耐震性や経済性に配慮し、架構を計画。
(3) 設備機器等の搬出入、更新、メンテナンス性及び景観に配慮。
(4) 延焼ライン(建築物の外壁の開口部で延焼のおそれのある部分の位置)を記入。必要に応じて、延焼ライン及び防火区画(面積区画、竪穴区画等)に要求される所定の防火設備を適切に計画。ただし、増築部と既存部の隣棟間には、延焼ラインが発生しないものとする。
(5) 地上に通じる２以上の直通階段を適切に計画。必要に応じて、「敷地内の避難上必要な通路」を適切に計画。
(6) 計画に際し、「天空率」、「避難上の安全の検証」等の規定を適用する場合には、「答案用紙Ⅱ」の裏面にその計算過程及び結果を記入。

要求室等(下表の室等は、全て計画。)

部門	室　名　等	特　記　事　項	床面積
宿泊部門	客室Ａ	・計12室以上計画し、そのうち２室をコネクティングルーム(隣り合う２つの客室をつなぎ、扉を介して直接、自由に行き来できる客室)に割り当て。 ・洋室(定員２名)、ベッド２台。 ・浴室、洗面所、トイレ。 ・バルコニー・ベランダ。	１室当たり25㎡以上
	客室Ｂ	・計２室以上計画。 ・洋室(定員２名)の車椅子使用者用客室、ベッド２台。 ・浴室、洗面所、トイレ。 ・バルコニー・ベランダ。	適　宜
	客室Ｃ	・計２室以上計画。 ・洋室(定員２名)のスイートルーム、ベッド２台。 ・ベッドルームとは別にリビングルーム。 ・浴室、洗面所、トイレ。 ・バルコニー・ベランダ。	適　宜
	リネン室	・客室のある全ての階に設ける。	適　宜
	・その他、宿泊部門に必要な室等は、適切に設ける。		
式場部門	チャペル	・既存部の１階に位置する。(答案用紙Ⅰ及び下書用紙の図を参照) ・定員60人程度の挙式を行うほか、イベントなどに使用。	－
	ウエディングサロン	・既存部の２階に位置する。(答案用紙Ⅰ及び下書用紙の図を参照) ・挙式に関する相談や申込みを受け付ける場所。 ・挙式中はスタッフの控室等に使用。	－
	控室	・新郎控室、新婦控室、牧師等控室のほか、親族控室(10人程度利用)を２室。 ・チャペルとの動線に配慮。	適　宜
	・その他、式場部門に必要な室等は、適切に設ける。		
管理・共用部門	ロビー		適　宜
	フロント		適　宜
	クローク	・宿泊客のほか、チャペル利用者、レストラン利用者の荷物等を預かる。	適　宜
	事務室	・執務スペース(従業員８人分)。	適　宜
	レストラン	・宿泊客、一般客が利用するほか、披露宴会場(バンケットルーム)としても使用。 ・厨房。	200㎡以上
	・その他、倉庫、ゴミ置場のほか、従業員用の更衣室、休憩室、トイレなど管理運営に必要な室等は、適切に設ける。		
設備	受水槽室	・受水槽及び給水ポンプ。	50㎡以上
	消火ポンプ室	・屋内消火栓用。	適　宜
	・電気設備(キュービクル)を屋上に設ける。 ・空調室外機、エレベーター、PS、DS、EPS等を、適切に設ける。 ・採用した設備計画に応じて、「機械室」等を適切に設ける。		
・その他必要な室等は、適切に設ける。 ・什器等を、適宜設ける。			

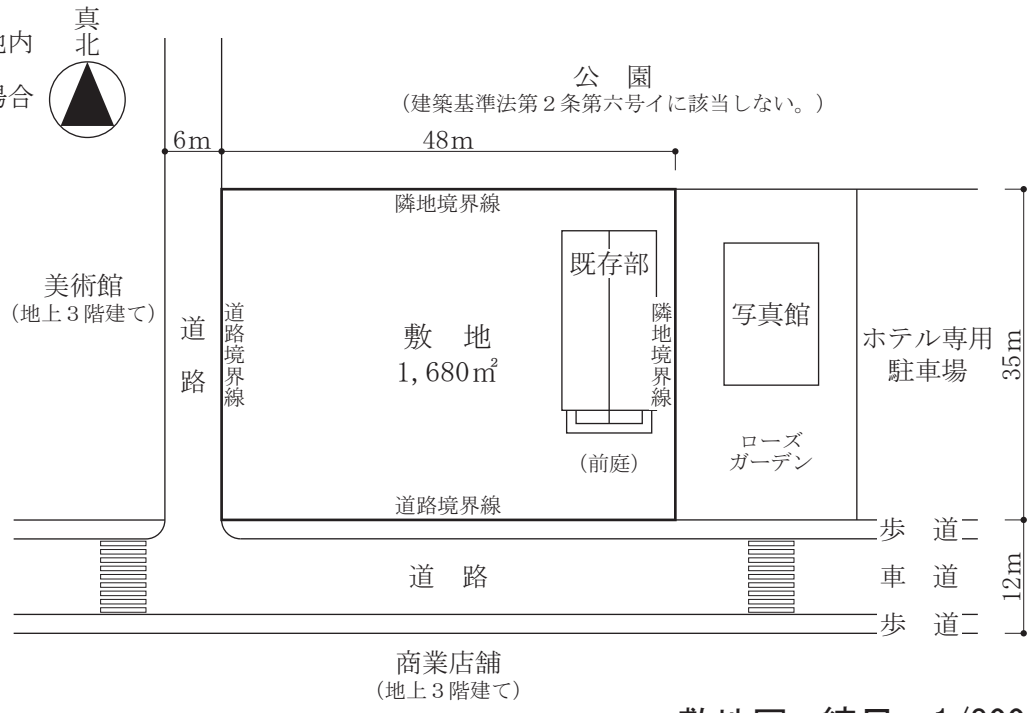

敷地図　縮尺＝1/800

Ⅱ. 要 求 図 書

答案用紙Ⅰ及び答案用紙Ⅱの定められた枠内(寸法線については枠外でもよい。)に、黒鉛筆を用いて記入。

１. 要 求 図 面(答案用紙Ⅰに記入)

「Ⅰ. 設計条件」の要求等を満足したことを明示した上で、下表に示す事項を図示又は記入し、図面を作成。(フリーハンドでもよい。)

ほかにも計画上で工夫、配慮した事項について、簡潔な文章や矢印等により補足して明示し、図面上に什器等を記入して表現。

図面及び縮尺	特記事項
(1) １階平面図・配置図 1/200 (2) ２階平面図 1/200 (3) ３階平面図 1/200	① 各平面図には、次のものを図示又は記入。 イ. 主要寸法、床面積、室名等、什器等 ロ. 延焼ライン(建築物の延焼のおそれのある部分の有無にかかわらず必ず記入。)と防火設備 ハ. 防火区画に用いる防火設備の位置及び種別 ニ. 断面図の切断位置 ホ. コネクティングルームとなる客室Ａの室内プラン(１室) ヘ. 代表的な客室Ｃの室内プラン(１室) ト. 増築部と既存部の接続部分(エキスパンションジョイントの位置を一点鎖線で明示し、Exp.Jと記入。) ② １階平面図・配置図には、次のものを図示又は記入。 イ. 駐車場及び車寄せ(それぞれ出入口を明示。) ロ. 「敷地内の避難上必要な通路」の経路と幅 ハ. 歩道の切り開き位置 ニ. 建築物から敷地境界線までの最小後退距離 ホ. 既存部の前庭等の外構計画(植栽、通路、ローズガーデンとの接続部等) ③ ２階平面図及び３階平面図には、次のものを図示又は記入。 イ. 居室の最も遠い位置から２の直通階段に至る歩行経路、その一に至る歩行距離及び重複区間の長さ ロ. 直下階の屋根、庇等
(4) 東-西断面図 1/200	① 切断位置は、東西方向とし、既存部及び客室(１か所以上)を含み、立体構成が分かる断面。なお、水平方向及び鉛直方向の省略は行わない。 ② 建築物の最高高さ、塔屋を除く建築物の高さ、階高、天井高、床高及び主要な室名等を記入。 ③ 高さ制限への適合が確認できる情報(道路・隣地斜線、最小後退距離、計算式等)を記入。(道路高さ制限及び隣地高さ制限がかからない根拠を必ず記入。) ④ 基礎(切断位置に現れない場合には、破線で図示。)、壁、梁及びスラブの断面を図示。 ⑤ 塔屋及び屋上の設備スペースを図示。(切断位置に現れない場合には、破線で図示。)

２. 面 積 表(答案用紙Ⅰに記入)

(1) 建築面積(既存部を含む。)の算定式及び合計を記入。

(2) 各階の床面積(既存部を含む。)の算定式及び合計、床面積の合計を記入。この課題の床面積の算定においては、ピロティ、塔屋、バルコニー・ベランダ(外気に有効に開放されているものに限る。)、屋外階段及び屋上設備スペースは、床面積に算入しない。ただし、ピロティ等を屋内的用途に供するもの(駐車場、設備スペース等)については、床面積に算入。

３. 計画の要点等(答案用紙Ⅱに記入)

要求図面では表せない建築物の計画上の要点等について、次の(1)～(5)を具体的に記述又は図示。(フリーハンドでもよい。)

(1) 客室Ｂについて、①～③のそれぞれに配慮した点(①～③が分かる「客室内平面図」及び「客室内断面図」をそれぞれ縮尺１/50程度で【イメージ図等記入欄】に記入し、配慮したことを図中に示す。)
  ① バリアフリー計画(寸法・仕様、使い勝手等)
  ② 水回りにおける段差の処理を踏まえた構造計画(梁の架け方等)
  ③ 客室内の快適性に配慮した空調換気設備計画

(2) ホテル利用者(宿泊客、チャペル利用者、レストラン利用者)、従業員のそれぞれに対し、動線計画及びセキュリティ・ゾーニング計画について、配慮した点

(3) エキスパンションジョイントのクリアランスと、その設定根拠(【イメージ図等記入欄】に、文章、図、イラスト等により示す。)


(4) ホテルの機能や特性を踏まえた、省エネルギー及び二酸化炭素排出量削減への配慮(ただし、太陽光パネル、LED照明、Low-Eガラスに関する記述は除く。)

(5) 外構計画について配慮した点

防火設備等の凡例

柱、壁、開口部等を明確に作図し、防火設備の表示(㊨・㊩)については、必要な箇所に**全て**記入

【延焼ライン(建築物の外壁の開口部で延焼のおそれのある部分の位置)と防火設備】

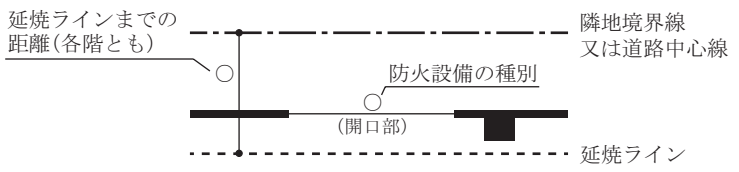

延焼ラインを破線で図示し、隣地境界線又は道路中心線から延焼ラインまでの**距離**を記入
また、建築物の外壁の開口部で、延焼のおそれのある部分の開口部に要求される所定の防火設備の**種別**を記入

【防火区画に用いる防火設備の位置及び種別】

防火区画(面積区画、竪穴区画等)に応じて、要求される所定の防火設備の**位置**及び**種別**を記入

【防火設備の表示】

特定防火設備 ㊨	建築基準法第２条第九号の二 ロ に規定する防火設備 ㊩

【建築物の計画に当たっての留意事項(課題公表(7/24)の再掲)】
- ○敷地の周辺環境や既存建築物の現状保存に配慮して計画する。
- ○バリアフリー、省エネルギー、二酸化炭素排出量削減、セキュリティ等に配慮して計画する。
- ○各要求室を適切にゾーニングし、明快な動線計画とする。
- ○建築物全体が、構造耐力上、安全であるとともに、経済性に配慮して計画する。
- ○構造種別に応じて架構形式及びスパン割りを適切に計画するとともに、適切な断面寸法の部材を計画する。
- ○空気調和設備、給排水衛生設備、電気設備、昇降機設備等を適切に計画する。

[注意事項]
「試験問題」を十分に理解したうえで、解答してください。
なお、建築基準法等の関係法令や要求図書、主要な要求室等の計画等の設計与条件に対して解答内容が不適合又は不十分な場合には、「設計条件・要求図書等に対する重大な不適合」等と判断されます。また、適用すべき法令については、令和８年１月１日現在において施行されているものとします。

※当日配布された「訂正表」については、
正しい内容等へ修正済み。

設計課題「ホテル」

★法令に関する指定を(注)で示します。

Ⅰ．設計条件

高原のリゾート地域にあり、緑豊かで景観に優れた公園に隣接した敷地に、チャペルを併設したホテルを計画。

計画に当たっては、敷地内に建つ既存の２階建てチャペル(以下「既存部」)を残し、新しくホテル(以下「増築部」)を増築するほか、増築部と既存部とを接続し、一の建築物とするとともに、次のことが求められている。

(1) ホテル利用者(宿泊客、チャペル利用者、レストラン利用者)、従業員等の円滑な動線計画及びセキュリティの確保
(2) 増築部と既存部との接続部の安全性(エキスパンションジョイント、バリアフリー等)の確保
(3) 敷地内外の環境への配慮

1．敷地及び周辺条件

(1) 敷地の形状、接道条件、周辺状況等は、「敷地図」のとおり。
(2) 敷地は平坦で、敷地と、道路の路面の中心、隣地及び道路の反対側の敷地には、高低差はない。また、歩道の切り開きは、２か所(１か所当たり６m)まで可能。
(3) 敷地及びその周辺は、近隣商業地域(道路高さ制限における斜線勾配は1.5、隣地高さ制限における斜線勾配は2.5とする。)及び準防火地域に指定。また、建蔽率の限度は80％(所定の加算を含む。)、容積率の限度は200％。これら以外に、地域、地区等及び特定行政庁による指定、許可等並びに日影による中高層の建築物の高さの制限はない。
(4) 電気、ガス及び上下水道は完備。
(5) 地盤は良好であり、杭打ちは不要。
(6) 気候は温暖であり、積雪について特別の配慮はしなくてよい。また、水害の危険がない地域。

2．建築物

(1) 増築部及び既存部は、１階及び２階の屋内で接続させて直接行き来できるように計画。なお、増築部と既存部が接続可能な位置は下書用紙にある「既存部平面図、屋根伏図、断面図」に示す位置とし、増築部及び既存部の条件は次のとおり。

項目	増築部	既存部
構造・階数	・構造種別は自由とし、地上３階建ての耐火建築物。	・耐震スリットを用いた純ラーメン構造による鉄筋コンクリート造、地上２階建ての耐火建築物。
規模等	・既存部と合わせた建築面積及び床面積が、建蔽率及び容積率の限度を超えないものとする。	・建築面積は、166.25㎡。 ・床面積の合計は、218.25㎡(１階の床面積は157.50㎡、２階の床面積は60.75㎡)。 ・１階床高は、GL＋200mm、２階床高は、GL＋4,500mm。
その他	－	・建築設備は建築基準法の現行基準に適合しているものとし、空調設備及び電気設備は改修する必要なし。 ・構造は耐震改修が既に行われており、建築基準法の現行基準に適合しているものとし、柱と梁は、撤去してはならない。

(2) 増築部及び既存部は、「高齢者、障害者等の移動等の円滑化の促進に関する法律」に規定する「建築物移動等円滑化基準」に適合するものとする。ただし、主たる階段は「建築物移動等円滑化誘導基準」に適合するものとする。
(3) 要求室等は、右表のとおり。

3．その他の施設等

(1) 駐車場は、次のとおり計画。
① 車椅子使用者用として１台分、サービス用として１台分のスペースを設ける。なお、建築物内でも可。
② ホテルの利用者用、従業員用の駐車場は、敷地東側にある写真館が所有するローズガーデンの隣にあるホテル専用駐車場を利用。なお、歩行者はホテル専用駐車場からローズガーデン内の通路を通って自由にホテルの敷地にアクセスすることが可能。
(2) ホテルの利用者用の車寄せを設ける。雨天時の乗降に配慮し、車寄せには、屋根、庇等を設ける。
(3) 既存部の前庭での記念撮影や屋外イベントなどの利用に配慮し、外構(植栽、通路等)の計画を行う。


4．留意事項

(1) 既存部と増築部とは接続し、一の建築物とする。
(2) 耐震性や経済性に配慮し、架構を計画。
(3) 設備機器等の搬出入、更新、メンテナンス性及び景観に配慮。
(4) 延焼ライン(建築物の外壁の開口部で延焼のおそれのある部分の位置)を記入。必要に応じて、延焼ライン及び防火区画(面積区画、竪穴区画等)に要求される所定の防火設備を適切に計画。ただし、増築部と既存部の隣棟間には、延焼ラインが発生しないものとする。
(5) 地上に通じる２以上の直通階段を適切に計画。必要に応じて、「敷地内の避難上必要な通路」を適切に計画。
(6) 計画に際し、「建築基準法第56条第７項(天空率)」、「建築基準法施行令第５章の３(避難上の安全の検証)」等の規定を適用する場合には、「答案用紙Ⅱ」の裏面にその計算過程及び結果を記入。

要求室等(下表の室等は、全て計画。)

部門	室名等	特記事項	床面積	1F	2F	3F
宿泊部門	客室A	・計12室以上計画し、そのうち２室をコネクティングルーム(隣り合う２つの客室をつなぎ、扉を介して直接、自由に行き来できる客室)。 ・洋室(定員２名)、ベッド２台。 ・浴室、洗面所、トイレ。 ・バルコニー・ベランダ。	１室当たり25㎡以上 (300)			
	客室B	・計２室以上計画。 ・洋室(定員２名)の車椅子使用者用客室、ベッド２台。 ・浴室、洗面所、トイレ。 ・バルコニー・ベランダ。	適宜 (60)			
	客室C	・計２室以上計画。 ・洋室(定員２名)のスイートルーム、ベッド２台。 ・ベッドルームとは別にリビングルーム。 ・浴室、洗面所、トイレ。 ・バルコニー・ベランダ。	適宜 (100)			
	リネン室	・客室のある全ての階に設ける。	適宜			
	・その他、宿泊部門に必要な室等は、適切に設ける。					
式場部門	チャペル	・既存部の１階に位置する。(答案用紙Ⅰ及び下書用紙の図を参照) ・定員60人程度の挙式を行うほか、イベントなどに使用。	－ 既存部1階			
	ウエディングサロン	・既存部の２階に位置する。(答案用紙Ⅰ及び下書用紙の図を参照) ・挙式に関する相談や申込みを受け付ける場所とする。 ・挙式中はスタッフの控室等に使用。	－ 既存部2階			
	控室	・新郎控室、新婦控室、牧師等控室のほか、親族控室(10人程度利用)２室。 ・チャペルとの動線に配慮。	適宜 (70)		○	
	・その他、式場部門に必要な室等は、適切に設ける。		(120)		○	
管理・共用部門	ロビー		(50) 適宜	○		
	フロント		(10) 適宜	○		
	クローク	・宿泊客のほか、チャペル利用者、レストラン利用者の荷物等を預かる。	(10) 適宜	○		
	事務室	・執務スペース(従業員８人分)。	7.5×8＝60 (60) 適宜	○		
	レストラン	・宿泊客、一般客が利用するほか、披露宴会場(バンケットルーム)としても使用。 ・厨房。	200㎡以上	○		
	・その他、倉庫、ゴミ置場のほか、従業員用の更衣室、休憩室、トイレなど管理運営に必要な室等は、適切に設ける。		55＋40＝95 (95)	○		
設備	受水槽室	・受水槽及び給水ポンプ。	50㎡以上	○		
	消火ポンプ室	・屋内消火栓用。	(10) 適宜	○		
	・電気設備(キュービクル)を屋上に設ける。 ・空調室外機、エレベーター、PS、DS、EPS等を、適切に設ける。 ・採用した設備計画に応じて、「機械室」等を適切に設ける。		(50)	○	○	○
	・その他必要な室等は、適切に設ける。 ・什器等を、適宜設ける。			○	○	○

真北

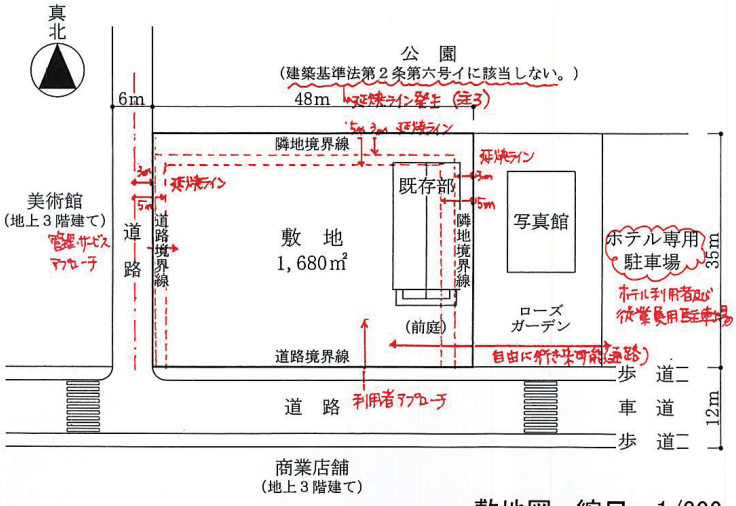

敷地図　縮尺＝1/800

Ⅱ. 要 求 図 書

答案用紙Ⅰ及び答案用紙Ⅱの定められた枠内(寸法線については枠外でもよい。)に、黒鉛筆を用いて記入。

1. 要求図面(答案用紙Ⅰに記入)

「Ⅰ. 設計条件」の要求等を満足したことを明示した上で、下表に示す事項を図示又は記入し、図面を作成。(フリーハンド可。)

ほかにも計画上で工夫、配慮した事項について、簡潔な文章や矢印等により補足して明示し、図面上に什器等を記入して表現。

図面及び縮尺	特記事項
(1) 1階平面図・配置図 1/200 (2) 2階平面図 1/200 (3) 3階平面図 1/200	① 各平面図には、次のものを図示又は記入。 イ. 主要寸法、床面積、室名等、什器等 ロ. 延焼ライン(建築物の延焼のおそれのある部分の有無にかかわらず必ず記入。)と防火設備 (注3) ハ. 防火区画に用いる防火設備の位置及び種別 (注3) ニ. 断面図の切断位置 ホ. コネクティングルームとなる客室Aの室内プラン(1室) ヘ. 代表的な客室Cの室内プラン(1室) ト. 増築部と既存部の接続部分(エキスパンションジョイントの位置を一点鎖線で明示し、Exp.Jと記入。) ② 1階平面図・配置図には、次のものを図示又は記入。 イ. 駐車場及び車寄せ(それぞれ出入口を明示。) (注4) ロ. 「敷地内の避難上必要な通路」の経路と幅 ハ. 歩道の切り開き位置 (注1) ニ. 建築物から敷地境界線までの最小後退距離 ホ. 既存部の前庭等の外構計画(植栽、通路、ローズガーデンとの接続部等) ③ 2階平面図及び3階平面図には、次のものを図示又は記入。 イ. 居室の最も遠い位置から2の直通階段に至る歩行経路、その一に至る歩行距離及び重複区間の長さ (注4) ロ. 直下階の屋根、庇等
(4) 東-西断面図 1/200	① 切断位置は、東西方向とし、既存部及び客室(1か所以上)を含み、立体構成が分かる断面。なお、水平方向及び鉛直方向の省略は不可。 ② 建築物の最高高さ、塔屋を除く建築物の高さ、階高、天井高、床高及び主要な室名等を記入。 ③ 高さ制限への適合が確認できる情報(道路・隣地斜線、最小後退距離、計算式等)を記入。(道路高さ制限及び隣地高さ制限がかからない根拠を必ず記入。) (注1) → 根拠を必ず記入 ④ 基礎(切断位置に現れない場合には、破線で図示。)、壁、梁及びスラブの断面を図示。 ⑤ 塔屋及び屋上の設備スペースを図示。(切断位置に現れない場合には、破線で図示。)

2. 面積表(答案用紙Ⅰに記入)

(1) 建築面積(既存部を含む。)の算定式及び合計を記入。

(2) 各階の床面積(既存部を含む。)の算定式及び合計、床面積の合計を記入。この課題の床面積の算定においては、ピロティ、塔屋、バルコニー・ベランダ(外気に有効に開放されているものに限る。)、屋外階段及び屋上設備スペースは、床面積に算入しない。ただし、ピロティ等を屋内的用途に供するもの(駐車場、設備スペース等)については、床面積に算入。

3. 計画の要点等(答案用紙Ⅱに記入)

要求図面では表せない建築物の計画上の要点等について、次の(1)～(5)を具体的に記述又は図示。(フリーハンド可。)

(1) 客室Bについて、次の①～③のそれぞれに配慮した点(①～③が分かる「客室内平面図」及び「客室内断面図」をそれぞれ縮尺1/50程度で【イメージ図等記入欄】に記入し、配慮したことを図中に示す。)
① バリアフリー計画(寸法・仕様、使い勝手等)
② 水回りにおける段差の処理を踏まえた構造計画(梁の架け方等)
③ 客室内の快適性に配慮した空調換気設備計画 → 換気経路(外気処理空調機の設置)

(2) ホテル利用者(宿泊客、チャペル利用者、レストラン利用者)、従業員のそれぞれに対し、動線計画及びセキュリティ・ゾーニング計画について、配慮した点 … (★1)

(3) エキスパンションジョイントのクリアランスと、その設定根拠(【イメージ図等記入欄】に、文章、図、イラスト等により示す。) … (★2)


(4) ホテルの機能や特性を踏まえた、省エネルギー及び二酸化炭素排出量削減への配慮(ただし、太陽光パネル、LED照明、Low-Eガラスに関する記述は除く。)

(5) 外構計画について配慮した点 … (★3)

〈防火設備等の凡例〉(注3)

柱、壁、開口部等を明確に作図し、防火設備の表示(特・防)については、必要な箇所に全て記入する

【延焼ライン(建築物の外壁の開口部で延焼のおそれのある部分の位置)と防火設備】

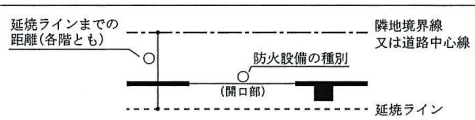

延焼ラインを破線で図示し、隣地境界線又は道路中心線から延焼ラインまでの距離を記入する
また、建築物の外壁の開口部で、延焼のおそれのある部分の開口部に要求される所定の防火設備の種別を記入する

【防火区画に用いる防火設備の位置及び種別】


防火区画(面積区画、竪穴区画等)に応じて、要求される所定の防火設備の位置及び種別を記入する

【防火設備の表示】


特定防火設備 (特)	建築基準法第2条第九号の二ロに規定する防火設備 (防)

【建築物の計画に当たっての留意事項(課題公表(7/24)の再掲)】
○敷地の周辺環境や既存建築物の現状保存に配慮して計画する。
○バリアフリー(注2)、省エネルギー、二酸化炭素排出量削減、セキュリティ(★1)等に配慮して計画する。
○各要求室を適切にゾーニングし、明快な動線計画とする。
○建築物全体が、構造耐力上、安全であるとともに、経済性に配慮して計画する。
○構造種別に応じて架構形式及びスパン割りを適切に計画するとともに、適切な断面寸法の部材を計画する。
○空気調和設備、給排水衛生設備、電気設備、昇降機設備等を適切に計画する。


設計課題「ホ　テ　ル」

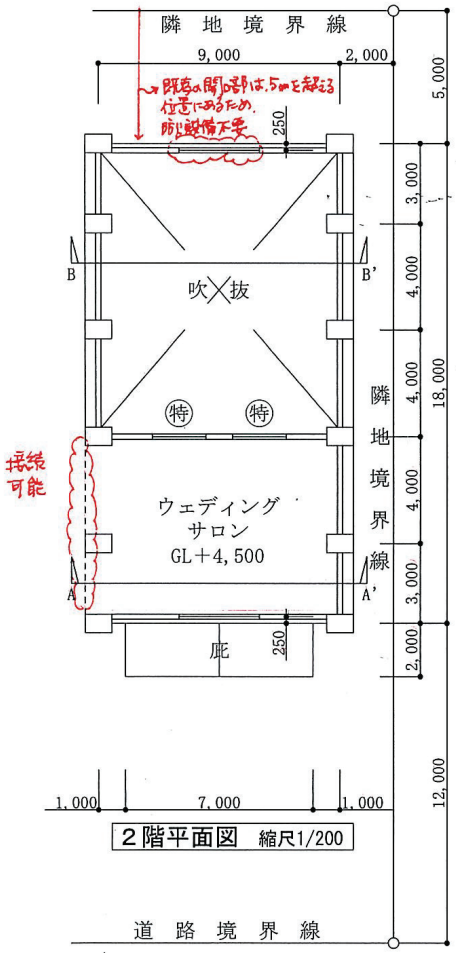


2階平面図　縮尺1/200

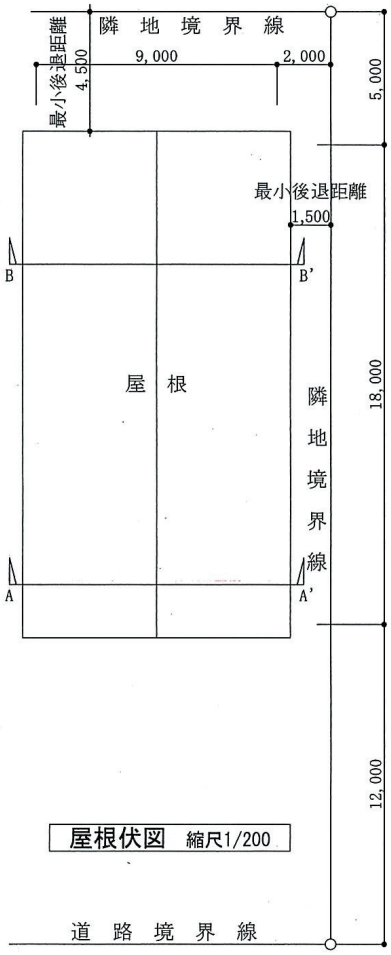

屋根伏図　縮尺1/200

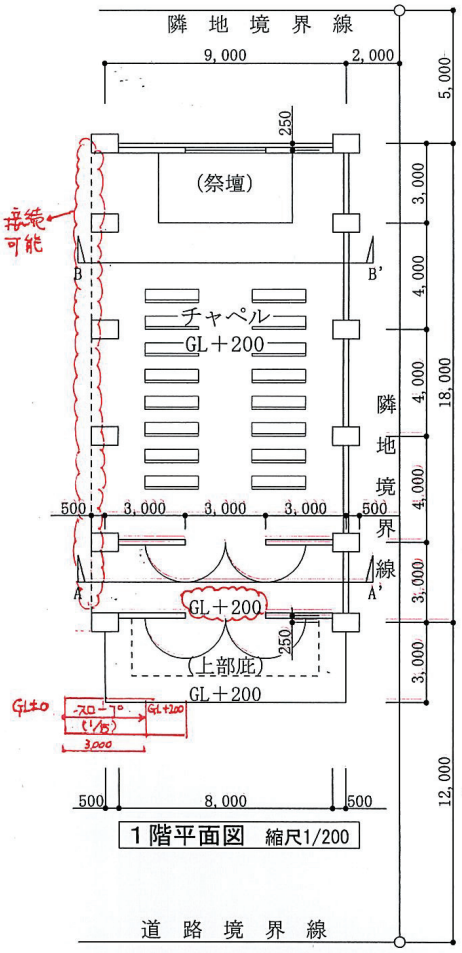

1階平面図　縮尺1/200

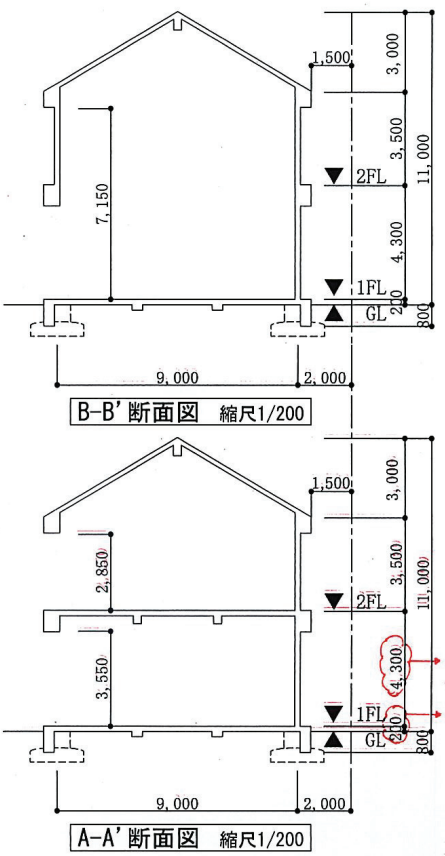

B-B'断面図　縮尺1/200

A-A'断面図　縮尺1/200

1階の階高を4,300mmとすることで2階との接続部においてもスロープを設けない。
1FL+200
増築部については、バリアフリーを考慮して、1FLを200とする。
※既存部にスロープを設けない（バリアフリー）
（注2）

（注）1階平面図及び2階平面図において点線で示す部分は、増築部と接続が可能な位置を示す。

既存部平面図、屋根伏図、断面図

令和８年　一級建築士試験「設計製図の試験」　答案用紙Ⅱ　計画の要点等　日建学院

(1)

建築面積		166.25 ＋ ㎡	
床面積	3階	㎡	㎡
	2階	60.75 ＋ ㎡	
	1階	157.50 ＋ ㎡	

【イメージ図等記入欄】

(2)

動線計画：

セキュリティ・ゾーニング計画：

(3)

【イメージ図等記入欄】

(4)

(5)

試験場		氏名	
受験番号	―　　―		


令和8年　一級建築士試験「設計製図の試験」　答案用紙Ⅰ

答案例


※禁無断複製・転売（この方眼用紙の1目盛は、5㎜です。）


日建学院


（2）２階平面図　（縮尺1/200）

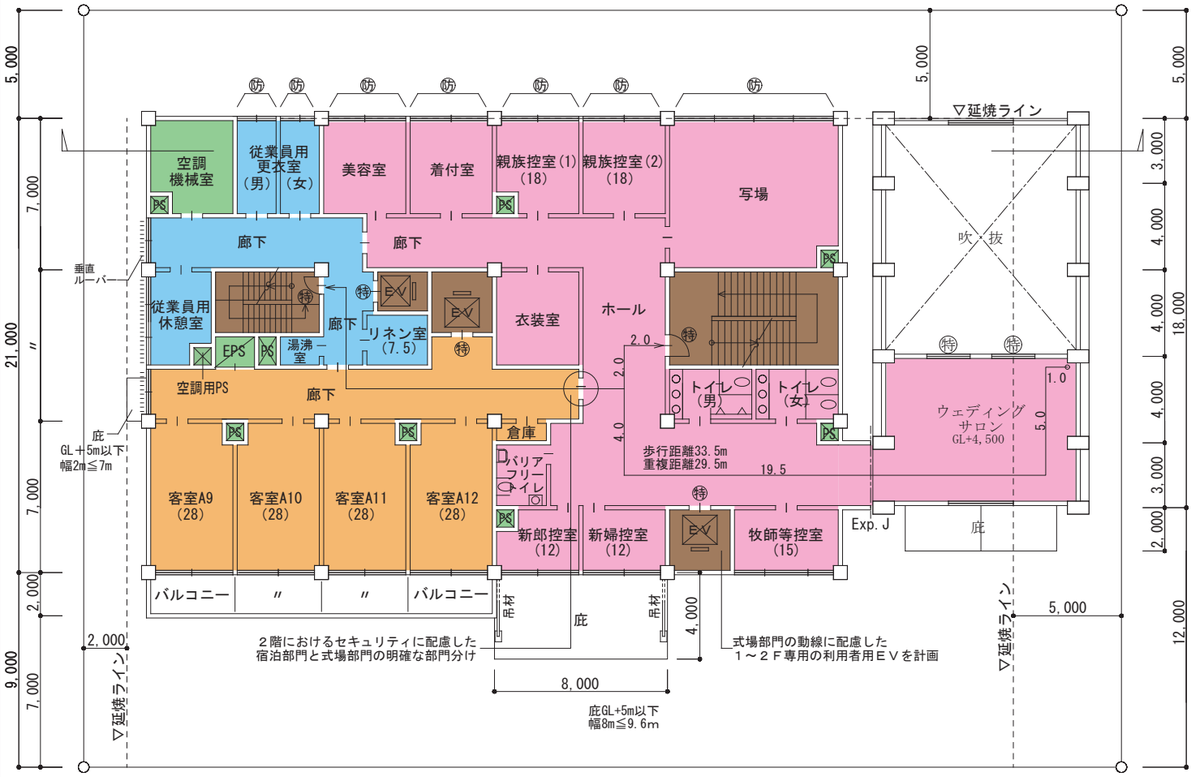

（3）３階平面図　（縮尺1/200）

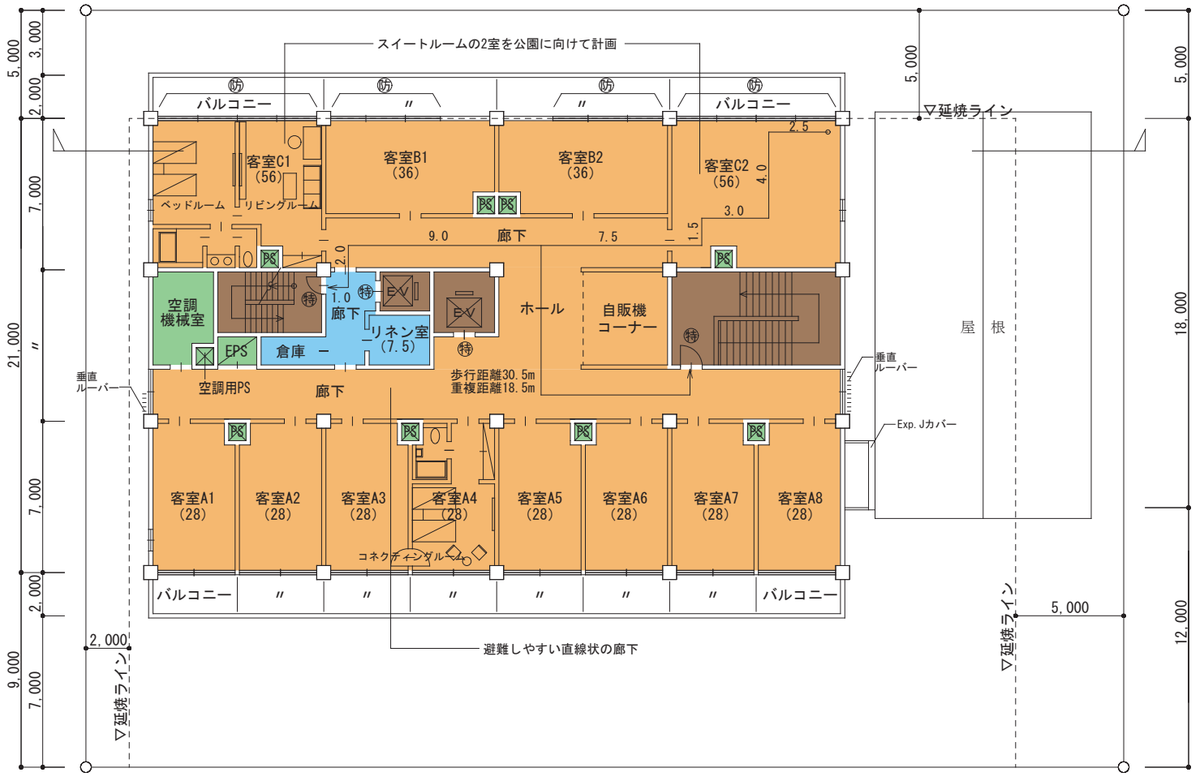

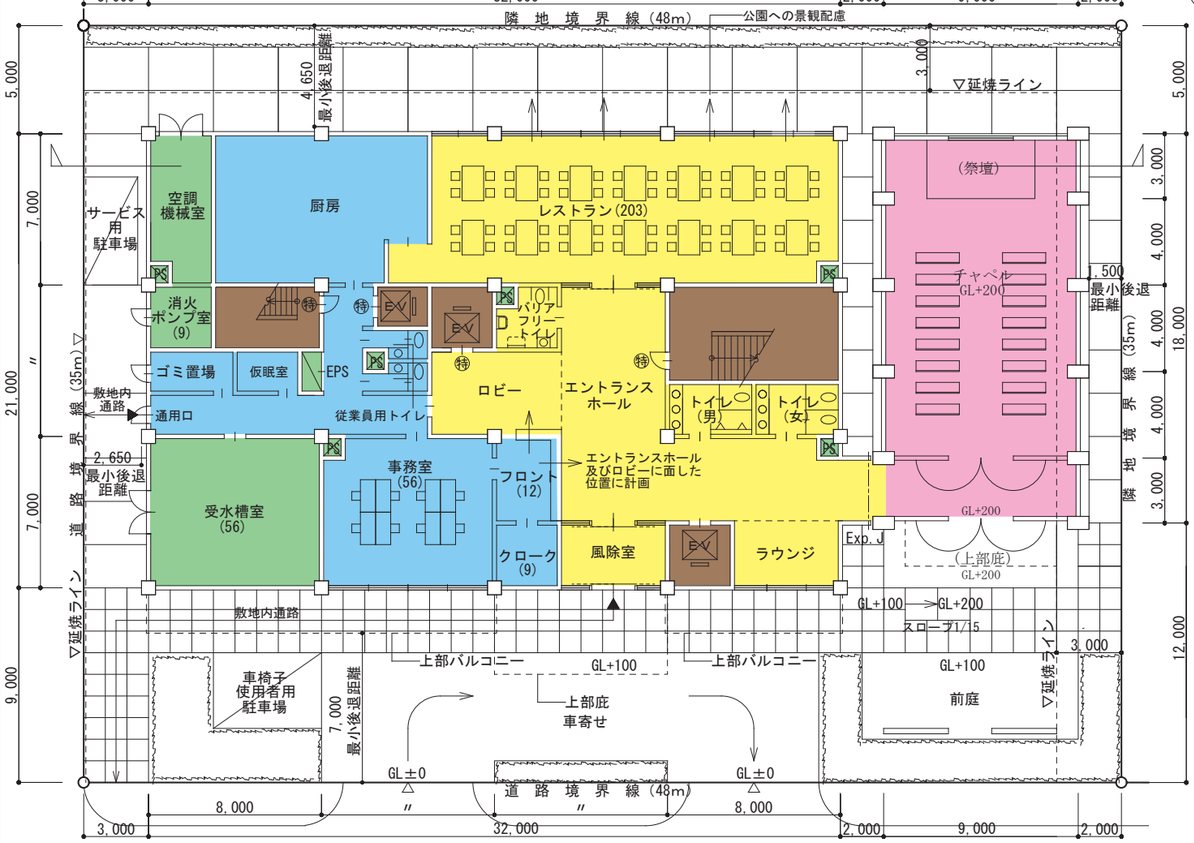

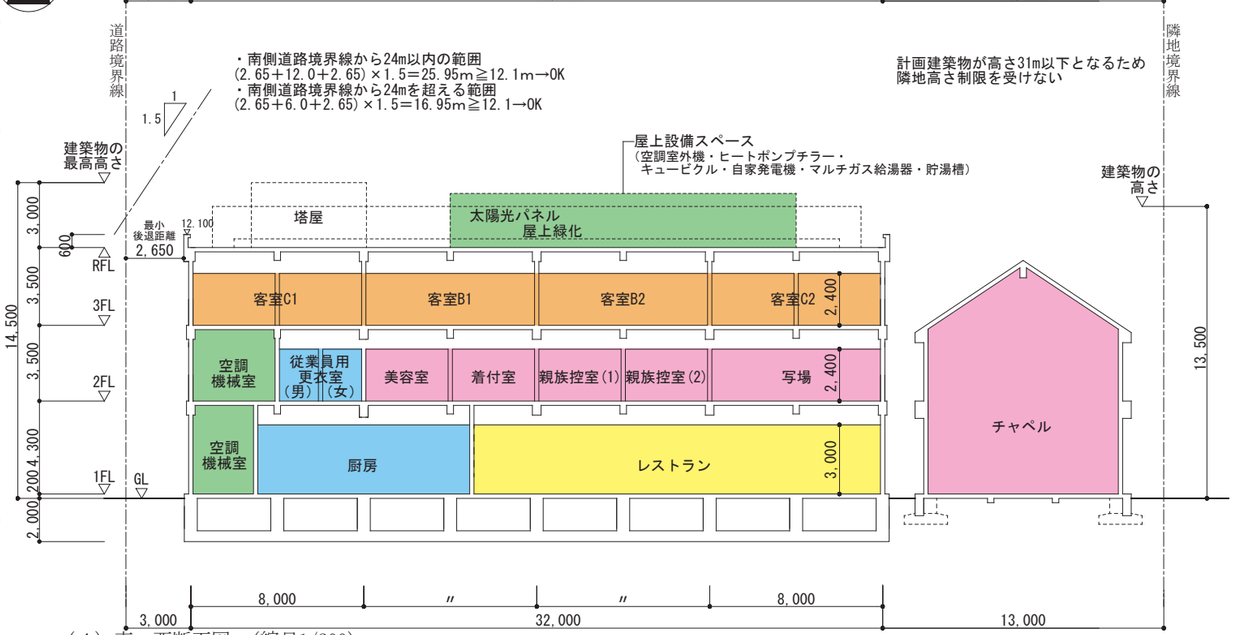

（4）東－西断面図　（縮尺1/200）

（1）１階平面図・配置図　（縮尺1/200）

面積表　（算定式は、算出過程が分かるものとする。算出結果は、少数点以下第１位までとし、第２位以下は切り捨てる。）

建築面積		（算定式及び合計） １６６．２５＋３２．０×２１．０＋３２．０×１．０ ＋１６．０×１．０＋８．０×３．０＋８．０×１．０＋２．０×３．０	９２４．２ ㎡
床面積	３　階	（算定式及び合計） ３２．０×２１．０＝	６７２．０ ㎡
	２　階	（算定式及び合計） ６０．７５＋３２．０×２１．０＋２．０×３．０＝	７３８．７ ㎡
	１　階	（算定式及び合計） １５７．５０＋３２．０×２１．０＋２．０×３．０＝	８３５．５ ㎡
	床面積の合計		２，２４６．２ ㎡