

「１階平面兼配置プラン」を記入してください。（縮尺1／100）

(注)不正確な内容では、皆さんのプランを正しく評価できません。敷地、屋外施設、室名、柱、開口部、寸法等を正確に記入してください。

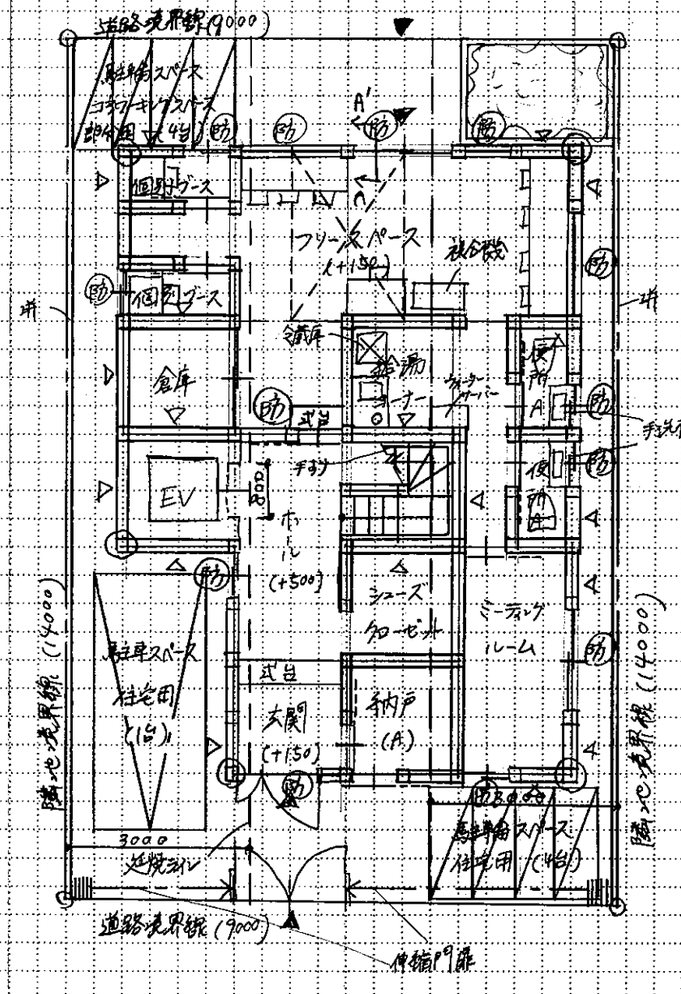

「２階平面プラン」を記入してください。（縮尺1／100）

(注)不正確な内容では、皆さんのプランを正しく評価できません。屋根、庇、室名、柱、開口部、寸法等を正確に記入してください。

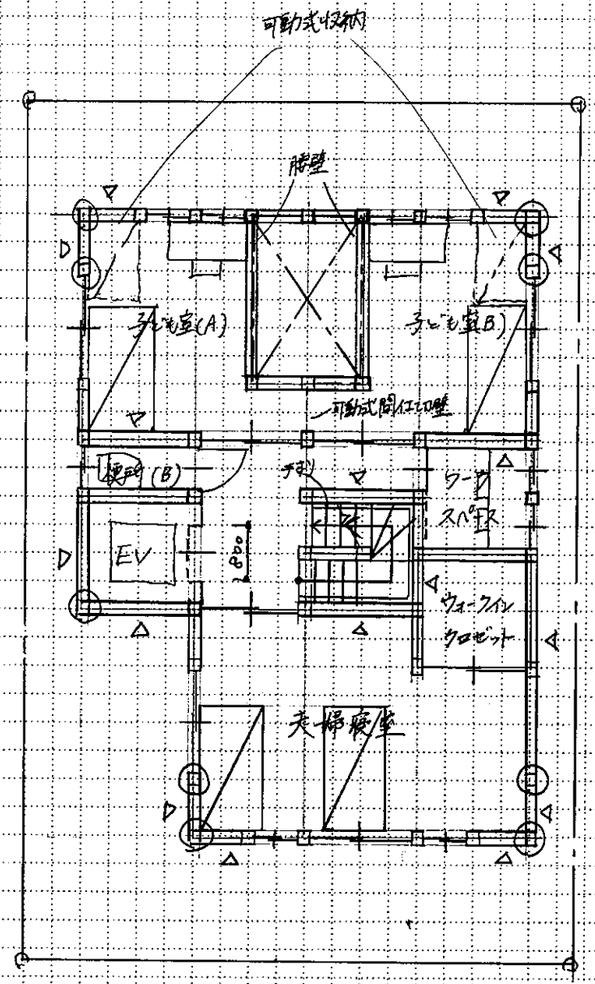

※2階数地盤面延焼ライン内


校名	池袋	学生番号	02800 - 0013 - 0209	受験番号	2F - 10173R	氏名	寺田 彩夏	

２０２６年度 ２級建築士 プラン復元用紙 〔2/2〕（本試験プランを丁寧に記入しましょう。）

日建学院

「３階平面プラン」を記入してください。（縮尺1／100）

(注)不正確な内容では、皆さんのプランを正しく評価できません。屋根、庇、室名、柱、開口部、寸法等を正確に記入してください。

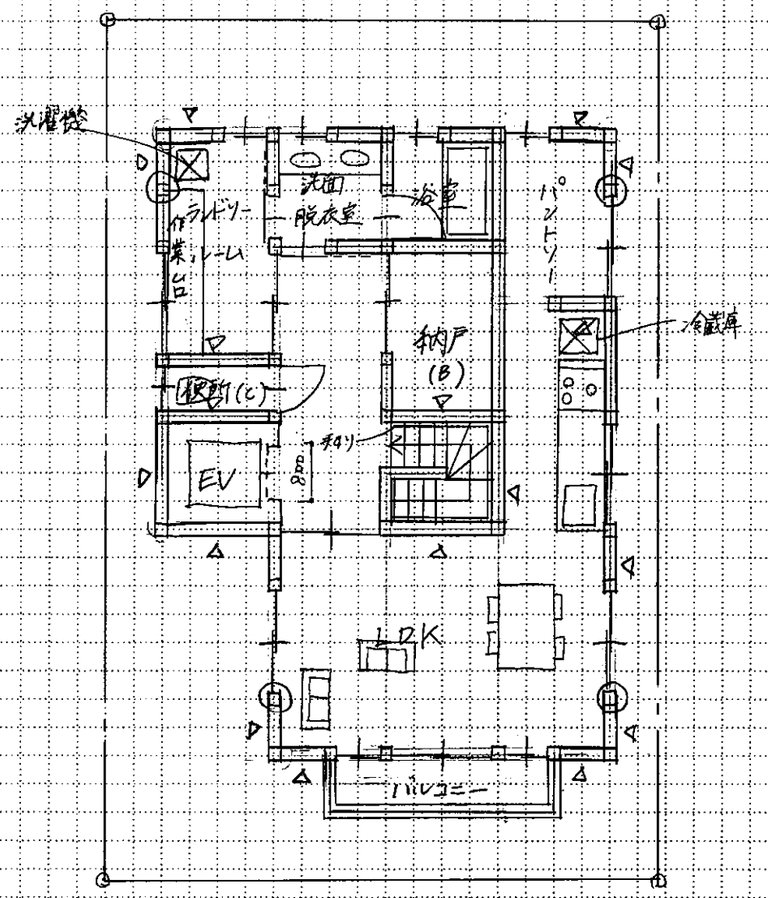

※3階敷地全域範囲ライン内

「計画の要点等の回答」を記入してください。

設問①：

コワーキングスペースは、気軽に利用できるよう、開口部やFIXを積極的に採用した。住宅部分はワーキングスペースと入口を完全に分離させ、塀などで囲うことで、セキュリティーやプライバシーにも考慮した計画とした。

設問②：

将来コワーキングスペース部分と一体に使用するために、コワーキングスペース部分のメインスペースであるフリースペースと吹抜けでつながるよう計画した。また吹抜けと出入口を部屋の中央部に配置することで、両東側部分がそれぞれ広く使える計画とした。

設問③：

窓は防火仕用のものを採用することで、準防火地域内にある住宅でも火災に対して安心できるよう配慮した。またその他構造部にも耐火仕用の材を積極的に採用した。

「面積表」を記入してください。（※印は出題された場合に記入してください）

敷地面積		126 ㎡	
建築面積		(計算式) (6.37×7.28)+(3.64×5.46)=66.248	66.24 ㎡
床面積	1階	(計算式) (6.37×7.28)+(3.64×5.46) =66.248	66.24 ㎡
	2階	(計算式) (6.37×7.28)+(3.64×5.46)-(1.82×2.73) =61.2794	61.27 ㎡
	3階	(計算式) (6.37×7.28)+(3.64×5.46) =66.248	66.24 ㎡
延べ面積		66.24+61.27+66.24	193.75 ㎡
※建蔽率		建築面積 66.24 ／ 敷地面積 126 ㎡	52.57 %
※容積率		延べ面積 193.75 ／ 敷地面積 126 ㎡	153.76 %

「作業時間・見直しの有無など」を記入してください。

プランニング	75 分	プラン完成後の見直し ☑した □していない
記述・面積表	20 分	作業に要した時間は普段と比べてどうでしたか？ ☑短い □同じ □長い
平面図	分	作業に要した時間は普段と比べてどうでしたか？ ☑短い □同じ □長い
立面図	分	作業に要した時間は普段と比べてどうでしたか？ □短い □同じ ☑長い
伏図	分	作業に要した時間は普段と比べてどうでしたか？ ☑短い □同じ □長い
部分詳細図	分	作業に要した時間は普段と比べてどうでしたか？ □短い ☑同じ □長い
見直し・仕上げ	5 分	答案完成後の見直し ☑した □していない

「本試験を受験して気になる事」を記入してください。（例：○○の意味が分からなかった。）

・ミーティングルームの家具 書き忘れた

・1F 上部吹き抜け部分の書き方 合ってる？

・2F 吹き抜け部分の囲み、文字で「勝望」と書いたほうが良い？

・△はあまり覚えていないが大体こんな感じ


・設問②にあまり対応できなかって （部分詳細 窓に「防火仕用」と書いたことくらい）

講師記入欄

氏名 寺田 彩夏


「１階平面兼配置プラン」を記入してください。（縮尺1／100）

(注)不正確な内容では、皆さんのプランを正しく評価できません。敷地、屋外施設、室名、柱、開口部、寸法等を正確に記入してください。

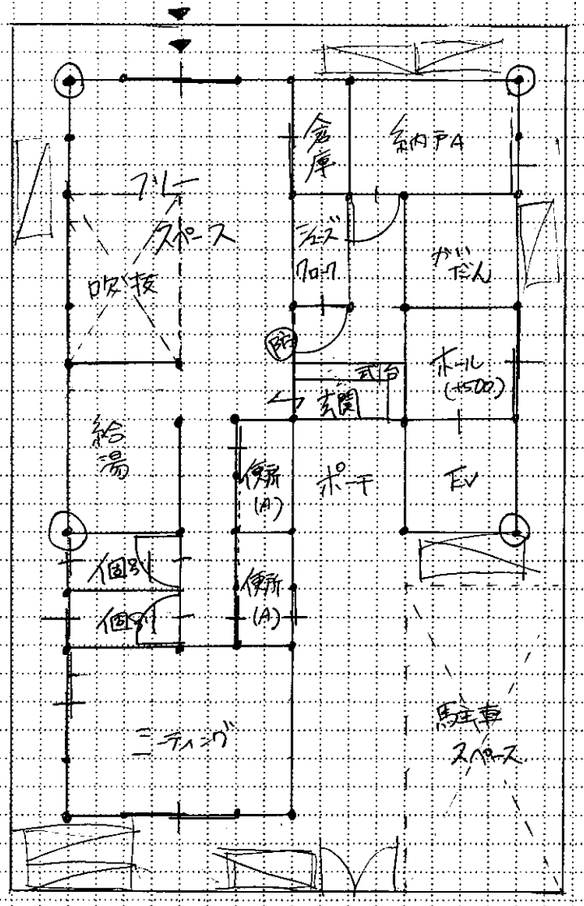

「２階平面プラン」を記入してください。（縮尺1／100）

(注)不正確な内容では、皆さんのプランを正しく評価できません。屋根、庇、室名、柱、開口部、寸法等を正確に記入してください。

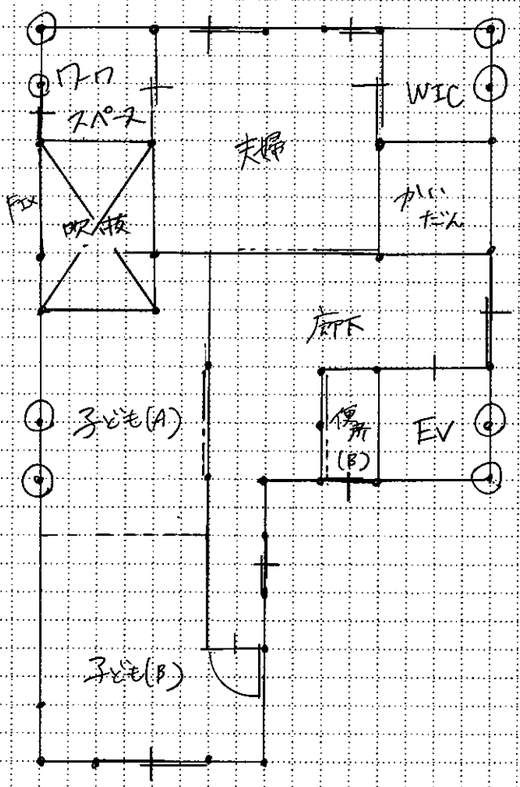


校名	池袋	学生番号	02800 － 0013 － 0217	受験番号	2D － 12801R	氏名	廣澤 里咲

２０２６年度 ２級建築士 プラン復元用紙 〔2/2〕（本試験プランを丁寧に記入しましょう。）

日建学院

「３階平面プラン」を記入してください。（縮尺1／100）

(注)不正確な内容では、皆さんのプランを正しく評価できません。屋根、庇、室名、柱、開口部、寸法等を正確に記入してください。

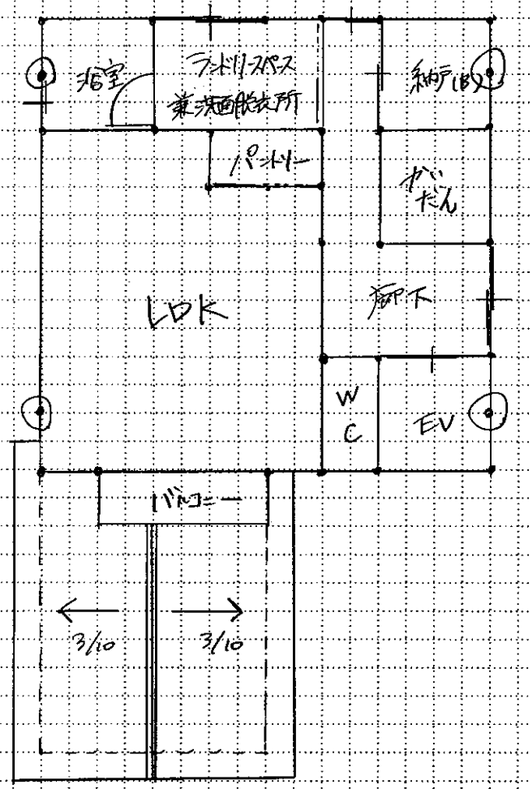

氏名 廣澤 里美

「計画の要点等の回答」を記入してください。

設問①：（気軽に利用できる要素を書きそびれました）
出入口をできる限り離した。住民と利用者の動線がまざらないようにした。

設問②：子ども室が将来ワーキングになることを見据えて、2階の子ども室以外の住居スペースを北側に寄せた。便所は相方が利用できるように玄関中設けた。

設問③：
延焼ラインを確認して窓扉 防火設備を設けた。
住宅部分とワーキングスペース部分の扉にも防火設備を設けた
建築基準法施行令第136条の2、同条2の2に順ずる。

「面積表」を記入してください。（※印は出題された場合に記入してください）

敷地面積		126 m²	
建築面積	(計算式) 7.28×7.28+3.64×4.55	69.55 m²	
床面積 1階	(計算式) 7.28×7.28+3.64×4.55−1.82×1.82	66.24 m²	
床面積 2階	(計算式) 7.28×7.28+3.64×4.55−1.82×2.93	64.59 m²	
床面積 3階	(計算式) 7.28×7.28	52.99 m²	
延べ面積		187.13 m²	
※建蔽率	建築面積 69.55 ／ 敷地面積 126 m²	55 %	
※容積率	延べ面積 187.13 ／ 敷地面積 126 m²	148 %	

「作業時間・見直しの有無など」を記入してください。

プランニング	60 分	プラン完成後の見直し ☑した ☐していない
記述・面積表	25 分	作業に要した時間は普段と比べてどうでしたか？ ☐短い ☑同じ ☐長い
平面図	185 分	作業に要した時間は普段と比べてどうでしたか？ ☑短い ☐同じ ☐長い
立面図	分	作業に要した時間は普段と比べてどうでしたか？ ☐短い ☐同じ ☐長い
伏図	分	作業に要した時間は普段と比べてどうでしたか？ ☐短い ☐同じ ☐長い
部分詳細図	分	作業に要した時間は普段と比べてどうでしたか？ ☐短い ☐同じ ☐長い
見直し・仕上げ	30 分	答案完成後の見直し ☑した ☐していない


「本試験を受験して気になる事」を記入してください。（例：○○の意味が分からなかった。）

覚えていないところが多いのであまり書けていなくてすみません。
下屋の上のバルコニーは大丈夫ですか？

講師記入欄

「~~1~~階平面兼配置プラン」を記入してください。（縮尺1／100）


(注)不正確な内容では、皆さんのプランを正しく評価できません。敷地、屋外施設、室名、柱、開口部、寸法等を正確に記入してください。

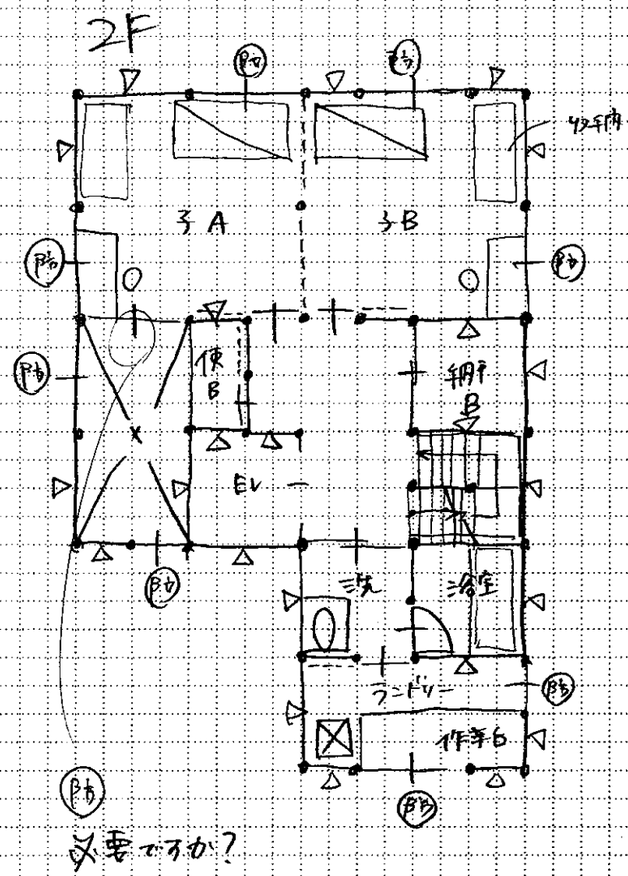

必要ですか？

「~~2~~階平面プラン」を記入してください。（縮尺1／100）


(注)不正確な内容では、皆さんのプランを正しく評価できません。屋根、庇、室名、柱、開口部、寸法等を正確に記入してください。

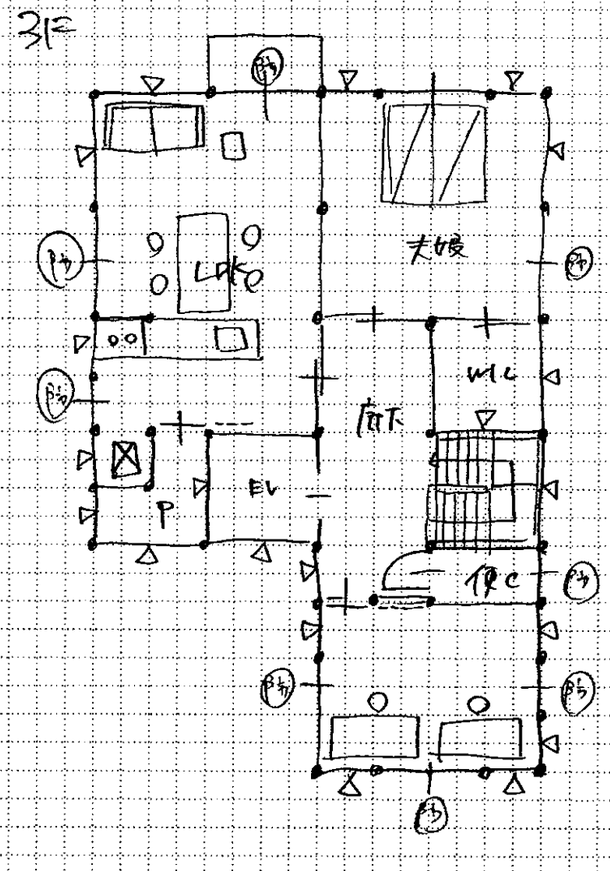

校名	池袋	学生番号	0280 - 0013 - 0222	受験番号	2F - 12636P	氏名	小栗 結衣	

「~~2~~階平面プラン」を記入してください。（縮尺1／100）

(注)不正確な内容では、皆さんのプランを正しく評価できません。屋根、庇、室名、柱、開口部、寸法等を正確に記入してください。

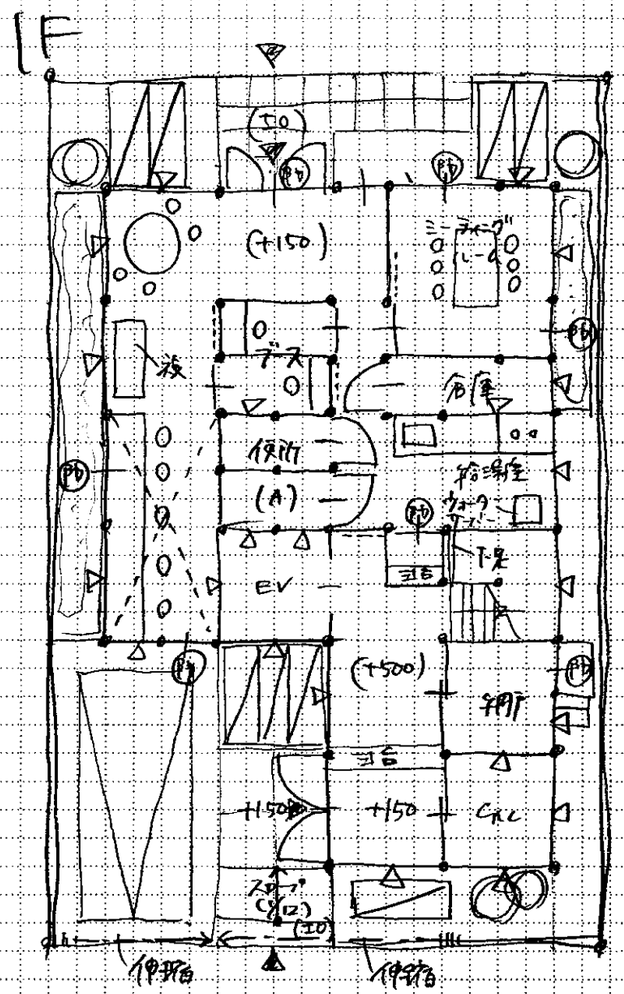

「計画の要点等の回答」を記入してください。

設問①：コワーキングスペースを北側一面に配置し、読書性を向上させた。また、3DKのバルコニーを北側に配置することでコワーキングスペースを利用する人の自保を支えさら、プライバシーに配慮した。

設問②：子ども室A・Bをそれぞれ北面、北東に配置し、間仕切壁を使用していても十分に採光を得られる計画とした。また、子ども室Aの南側に開口のある吹き抜けを設けることで、間仕切壁を介さず東面南北から採光を得られる計画とした。

設問③：建築物の主要構造部を一定の耐火性能のある準耐火構造とした。

「面積表」を記入してください。（※印は出題された場合に記入してください）

敷地面積			126.00 ㎡
建築面積	(計算式) (7.28×7.28)+(3.64×3.64)		66.24 ㎡
床面積 1階	(計算式) (7.28×7.28)+(3.64×3.64)		66.24 ㎡
床面積 2階	(計算式) (7.28×7.28)+(3.64×3.64)-(1.82×3.64)		59.62 ㎡
床面積 3階	(計算式) (7.28×7.28)+(3.64×3.64)		66.24 ㎡
延べ面積			192.1 ㎡
※建蔽率	建築面積 ／ 敷地面積	㎡	%
※容積率	延べ面積 ／ 敷地面積	㎡	%

「作業時間・見直しの有無など」を記入してください。

プランニング	50 分	プラン完成後の見直し ☑した □していない
記述・面積表	25 分	作業に要した時間は普段と比べてどうでしたか？ ☑短い □同じ □長い
平面図	1h 55 分	作業に要した時間は普段と比べてどうでしたか？ ☑短い □同じ □長い
立面図	20 分	作業に要した時間は普段と比べてどうでしたか？ ☑短い □同じ □長い
伏図	25 分	作業に要した時間は普段と比べてどうでしたか？ □短い ☑同じ □長い
部分詳細図	20 分	作業に要した時間は普段と比べてどうでしたか？ □短い □同じ ☑長い
見直し・仕上げ	25 分	答案完成後の見直し ☑した □していない

「本試験を受験して気になる事」を記入してください。（例：○○の意味が分からなかった。）


吹き抜けと子ども室Aの間の開口部は防火設備必要でしょうか？

講師記入欄

氏名	小栗 結花


「１階平面兼配置プラン」を記入してください。（縮尺1／100）

（注）不正確な内容では、皆さんのプランを正しく評価できません。敷地、屋外施設、室名、柱、開口部、寸法等を正確に記入してください。

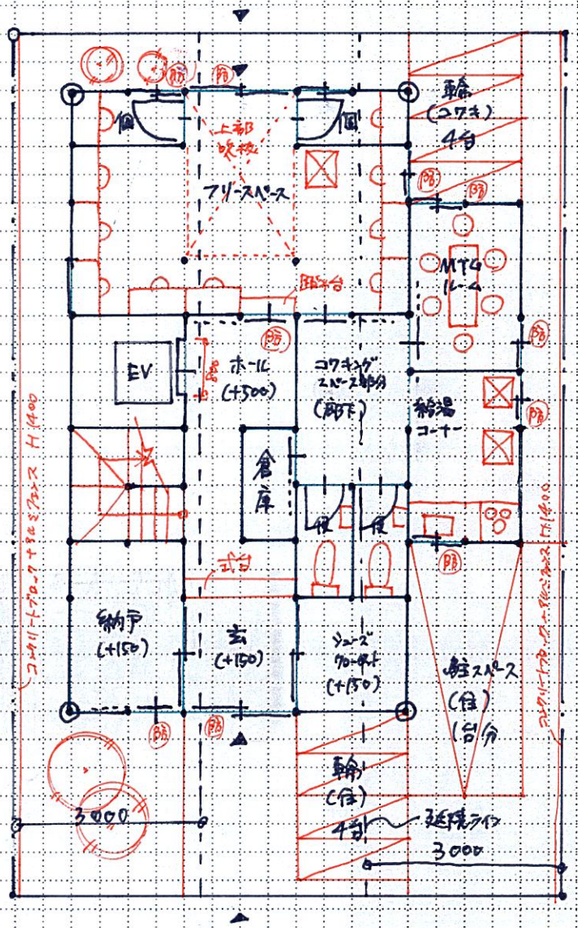

「２階平面プラン」を記入してください。（縮尺1／100）

（注）不正確な内容では、皆さんのプランを正しく評価できません。屋根、庇、室名、柱、開口部、寸法等を正確に記入してください。

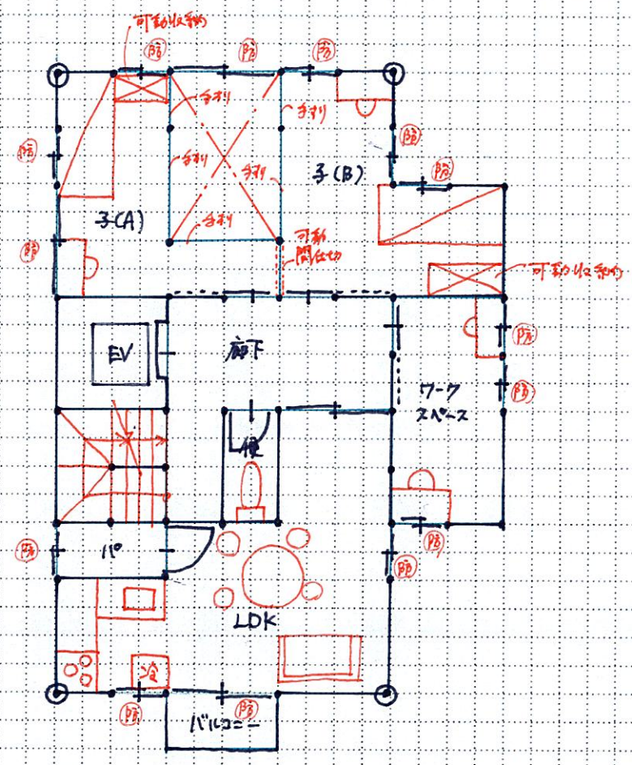


※全て延焼ライン内

校名	池袋	学生番号	－ －	受験番号	－	氏名	小村 赳来	②

「３階平面プラン」を記入してください。（縮尺1／100）

(注)不正確な内容では、皆さんのプランを正しく評価できません。屋根、庇、室名、柱、開口部、寸法等を正確に記入してください。

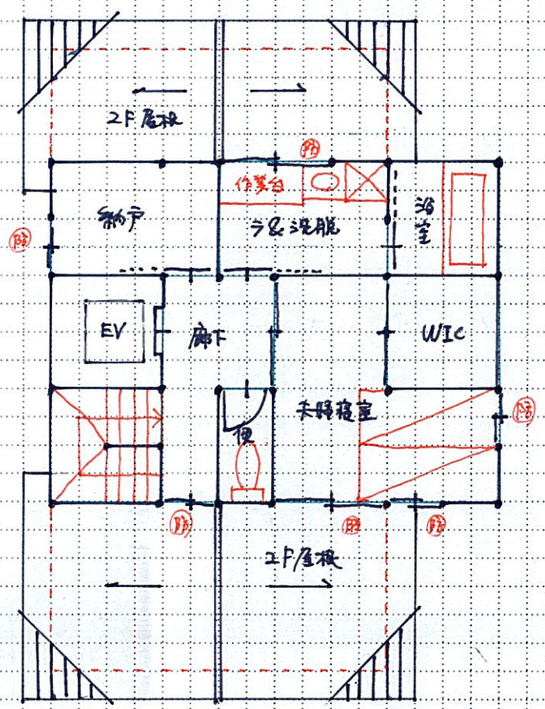

※全て延焼ライン内

氏名 小村 和史

「計画の要点等の回答」を記入してください。

設問①：コワーキングスペース部分を道路側に寄せることで利用者が自然に立ち寄れるよう計画した。また住宅部は道路からある程度セットバックさせ、玄関にパッシブセンサーを設置することでセキュリティに配慮した計画とした。

設問②：吹抜けを道路側にもってくることで採光の向上を図った。また玄関に近い位置にすることで子ども室をコワーキング化や隣接への変更もしやすい計画とした。

設問③：準防火地域の建築物のため主要構造部を準耐火構造にて計画した。

「面積表」を記入してください。（※印は出題された場合に記入してください）

敷地面積				㎡
建築面積		(計算式) (10.01×5.46)+(1.82×5.46)	64.59	㎡
床面積	1階	(計算式) (10.01×5.46)+(1.82×5.46)	64.59	㎡
	2階	(計算式) (10.01×5.46)+(1.82×5.46)	64.59	㎡
	3階	(計算式) 7.28×5.46	39.74	㎡
延べ面積			168.92	㎡
※建蔽率		建築面積 / 敷地面積		%
※容積率		延べ面積 / 敷地面積		%

「作業時間・見直しの有無など」を記入してください。

プランニング	90 分	プラン完成後の見直し ☑した ☐していない
記述・面積表	20 分	作業に要した時間は普段と比べてどうでしたか？ ☑短い ☐同じ ☐長い
平面図	70 分	作業に要した時間は普段と比べてどうでしたか？ ☐短い ☑同じ ☐長い
立面図	60 分	作業に要した時間は普段と比べてどうでしたか？ ☐短い ☐同じ ☑長い
伏図	20 分	作業に要した時間は普段と比べてどうでしたか？ ☑短い ☐同じ ☐長い
部分詳細図	20 分	作業に要した時間は普段と比べてどうでしたか？ ☑短い ☐同じ ☐長い
見直し・仕上げ	20 分	答案完成後の見直し ☑した ☐していない

「本試験を受験して気になる事」を記入してください。（例：○○の意味が分からなかった。）

・書いて消してをくりかえしたため時間立面が辛い…

・子ども独立ユニットをコワーキングスペースとした時へ導線も考慮すべきかわからず無視した…


・計画再点③ 何を書けばいいのか…

・部詳 書きすぎはしたが自信なし。床伏は自信ありです。

講師記入欄


「１階平面兼配置プラン」を記入してください。（縮尺1／100）

(注)不正確な内容では、皆さんのプランを正しく評価できません。敷地、屋外施設、室名、柱、開口部、寸法等を正確に記入してください。

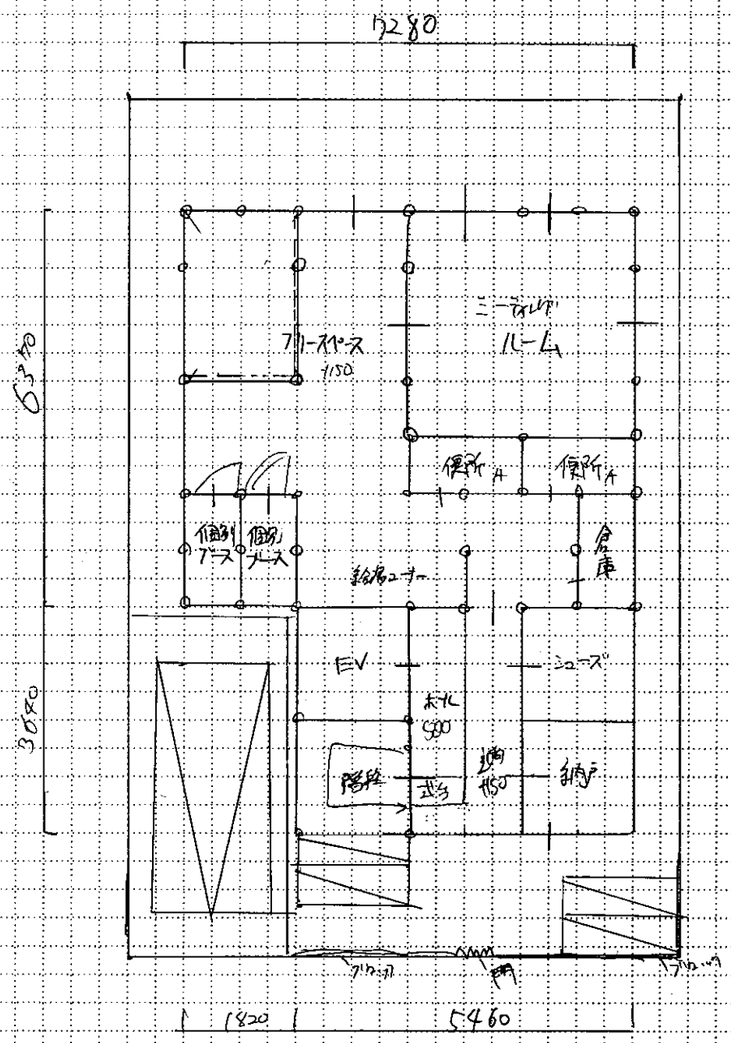

「２階平面プラン」を記入してください。（縮尺1／100）

(注)不正確な内容では、皆さんのプランを正しく評価できません。屋根、庇、室名、柱、開口部、寸法等を正確に記入してください。

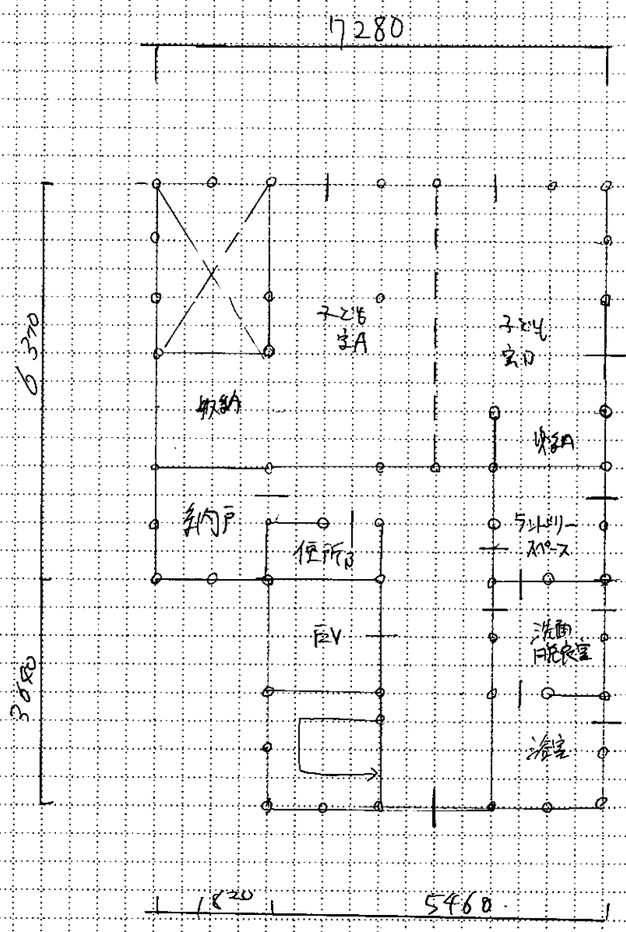


校名		学生番号	—	—	受験番号	—	氏名	滝谷太雅	

２０２６年度 ２級建築士 プラン復元用紙 〔2/2〕（本試験プランを丁寧に記入しましょう。）

日建学院

「3階平面プラン」を記入してください。（縮尺1／100）

(注)不正確な内容では、皆さんのプランを正しく評価できません。屋根、庇、室名、柱、開口部、寸法等を正確に記入してください。

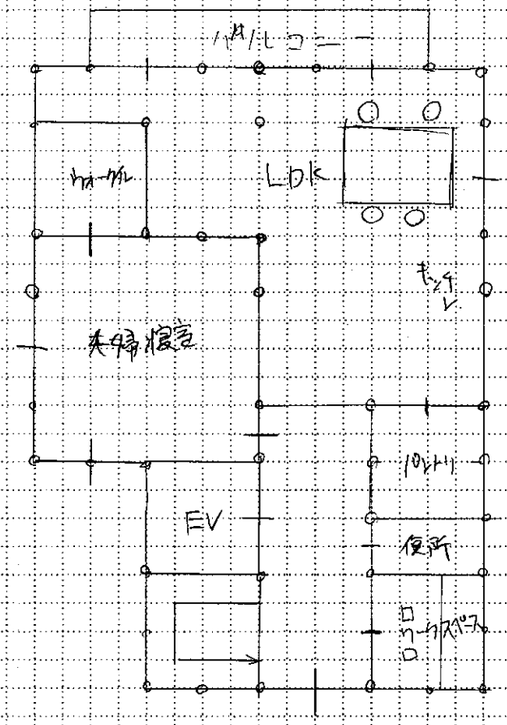

氏名 近畑 大拓

「計画の要点等の回答」を記入してください。

設問①：コーキングスペースの離隔距離をなるべく小さくし、開口部を多く設けて、視認性を高め、LDKの面したバルコニーを設け柱線をさえぎりプライバシーを確保し、間にエリヤセキュリティを高めた。

設問②：将来 子ども室が隣接している、吹き抜けを将来階段として使うために吹き抜けた子ども室2つを隣接した。

設問③：主要構造部を耐火構造とし、延焼の防止のため、開口部を防火設備とした。

「面積表」を記入してください。（※印は出題された場合に記入してください）

敷地面積		126.00	㎡
建築面積	(計算式) (7.28×6.37)+(3.64×5.46)	66.25	㎡
床面積 1階	(計算式) (7.28×6.37)+(3.64×5.46)	66.25	㎡
床面積 2階	(計算式) (7.28×6.37)+(3.64×5.46)−(1.82×2.73)	61.28	㎡
床面積 3階	(計算式) (7.28×6.37)+(3.64×5.46)	66.25	㎡
延べ面積		193.78	㎡
※建蔽率	建築面積 66.25 / 敷地面積 126	52	%
※容積率	延べ面積 193.78 / 敷地面積 126	153	%

「作業時間・見直しの有無など」を記入してください。

プランニング	2時間30 分	プラン完成後の見直し □した □していない
記述・面積表	5 分	作業に要した時間は普段と比べてどうでしたか？ □短い □同じ □長い
平面図	1:30 分	作業に要した時間は普段と比べてどうでしたか？ □短い □同じ □長い
立面図	20 分	作業に要した時間は普段と比べてどうでしたか？ □短い □同じ □長い
伏図	20 分	作業に要した時間は普段と比べてどうでしたか？ □短い □同じ □長い
部分詳細図	20 分	作業に要した時間は普段と比べてどうでしたか？ □短い □同じ □長い
見直し・仕上げ	分	答案完成後の見直し □した □していない


「本試験を受験して気になる事」を記入してください。（例：○○の意味が分からなかった。）

伏図の部分に 一点鎖線を忘れてはい [3.64×5.46] ←この部分に 文字を書いてしまった

講師記入欄


「１階平面兼配置プラン」を記入してください。（縮尺1／100）

(注) 不正確な内容では、皆さんのプランを正しく評価できません。敷地、屋外施設、室名、柱、開口部、寸法等を正確に記入してください。

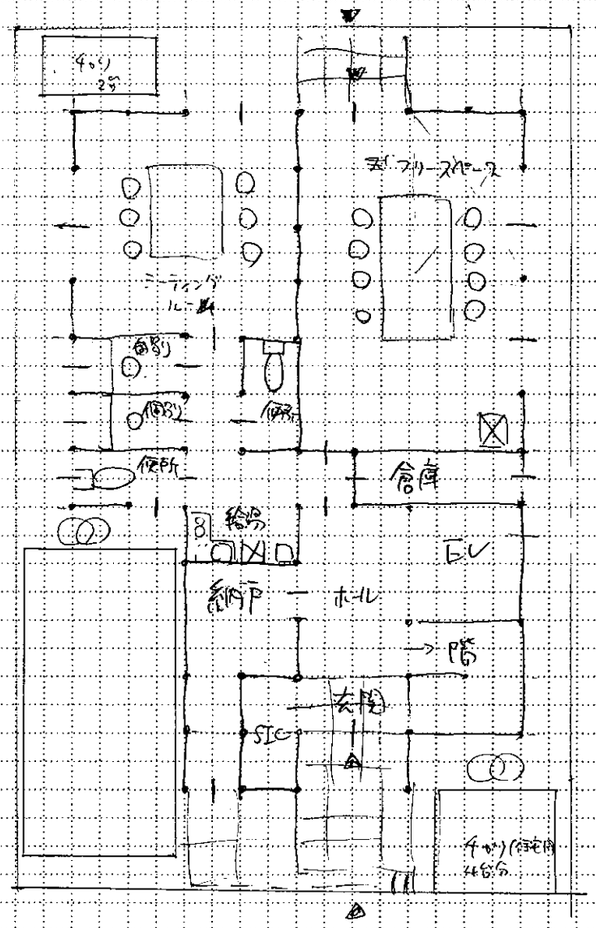

「２階平面プラン」を記入してください。（縮尺1／100）

(注) 不正確な内容では、皆さんのプランを正しく評価できません。屋根、庇、室名、柱、開口部、寸法等を正確に記入してください。

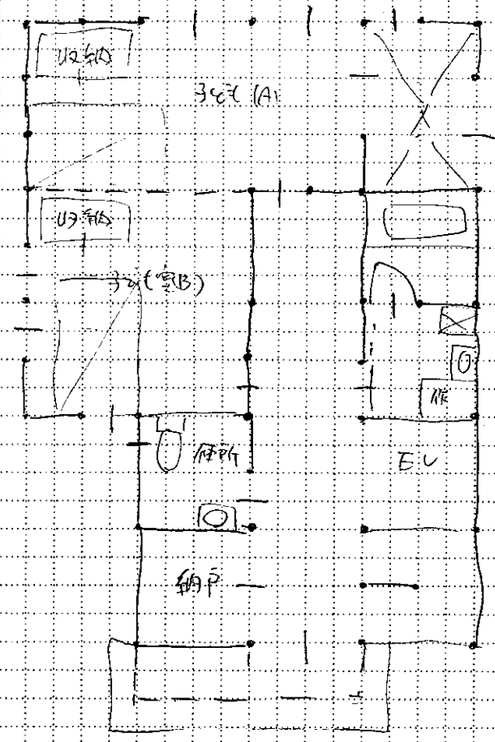


校名		学生番号	00280 － 0013 － 0255	受験番号	2F － 115756	氏名	小森谷 玲雄	(2)

2026年度 2級建築士 プラン復元用紙 〔2/2〕（本試験プランを丁寧に記入しましょう。）

日建学院

「3階平面プラン」を記入してください。（縮尺1／100）

(注)不正確な内容では、皆さんのプランを正しく評価できません。屋根、庇、室名、柱、開口部、寸法等を正確に記入してください。

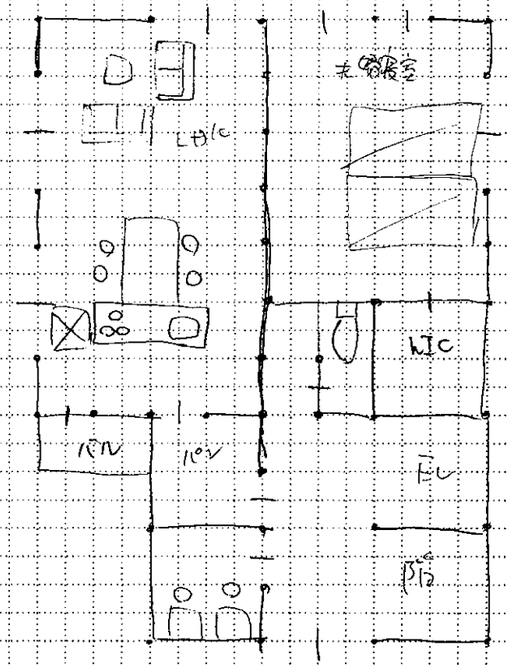

「計画の要点等の回答」を記入してください。

設問①：プライバシー確保のためにバルコニーを南側に計画した。セキュリティーの確保のために鍵つきの伸縮門扉にした。

設問②：吹抜部分に窓を設け，採光を確保した。また，取外し間仕切り壁をとると大きな空間になるようにした。

設問③：延焼ライン内の外に面している設備を含て防火設備とした。また，店舗と住宅部分で付き来できる設備も防火設備とした。

「面積表」を記入してください。（※印は出題された場合に記入してください）

敷地面積			126.00	m²
建築面積		(計算式) (7.28×10.01)-(1.82×3.64)+(1.82×0.91)	67.90	m²
床面積	1階	(計算式) (7.28×10.01)-(1.82×3.64)+(1.82×0.91)	67.90	m²
	2階	(計算式) (7.28×10.01)-(1.82×3.64)-(1.82×2.73)	61.27	m²
	3階	(計算式) (7.28×10.01)-(1.82×3.64)	66.24	m²
延べ面積			195.41	m²
※建蔽率		建築面積 67.90 ／ 敷地面積 126.00 m²	53.88	%
※容積率		延べ面積 195.41 ／ 敷地面積 126.00 m²	155.08	%

「作業時間・見直しの有無など」を記入してください。

プランニング	80 分	プラン完成後の見直し ☑した ☐していない
記述・面積表	5+10 分	作業に要した時間は普段と比べてどうでしたか？ ☐短い ☑同じ ☐長い
平面図	90 分	作業に要した時間は普段と比べてどうでしたか？ ☐短い ☑同じ ☐長い
立面図	20 分	作業に要した時間は普段と比べてどうでしたか？ ☐短い ☑同じ ☐長い
伏図	30 分	作業に要した時間は普段と比べてどうでしたか？ ☐短い ☑同じ ☐長い
部分詳細図	30 分	作業に要した時間は普段と比べてどうでしたか？ ☐短い ☐同じ ☐長い
見直し・仕上げ	15+20 分	答案完成後の見直し ☑した ☐していない

「本試験を受験して気になる事」を記入してください。（例：○○の意味が分からなかった。）


・耐力壁を2階，3階に書き忘れた可能性大

講師記入欄

氏名 小森谷 瑞樹


「１階平面兼配置プラン」を記入してください。（縮尺1／100）

(注) 不正確な内容では、皆さんのプランを正しく評価できません。敷地、屋外施設、室名、柱、開口部、寸法等を正確に記入してください。

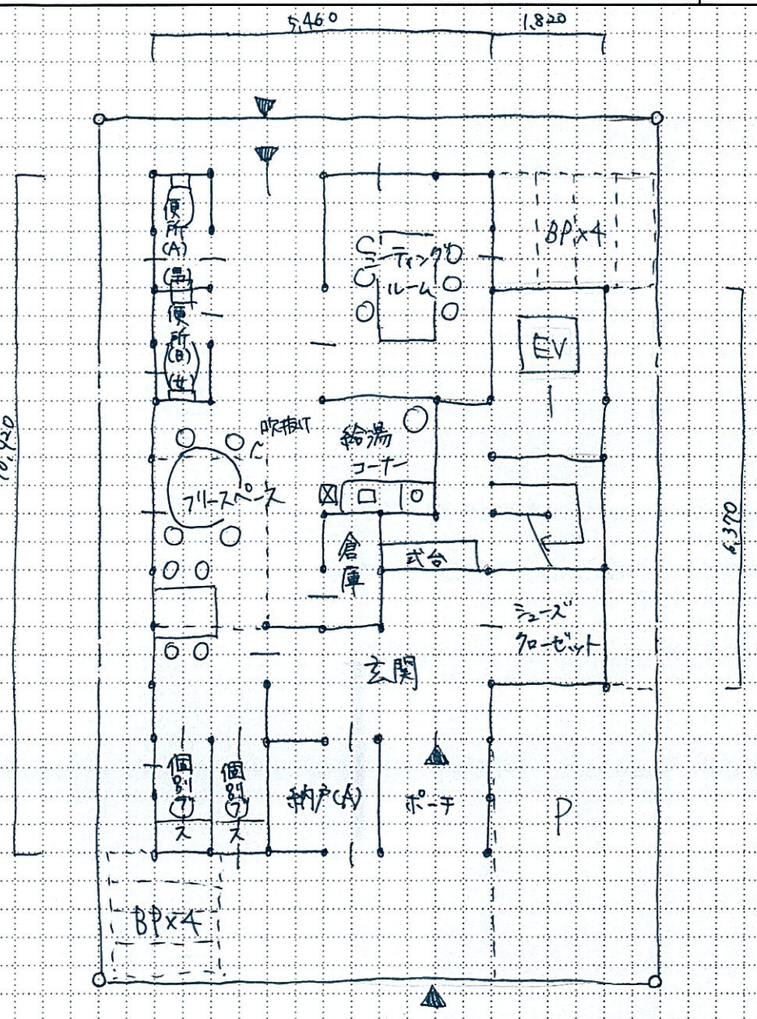

「２階平面プラン」を記入してください。（縮尺1／100）

(注) 不正確な内容では、皆さんのプランを正しく評価できません。屋根、庇、室名、柱、開口部、寸法等を正確に記入してください。

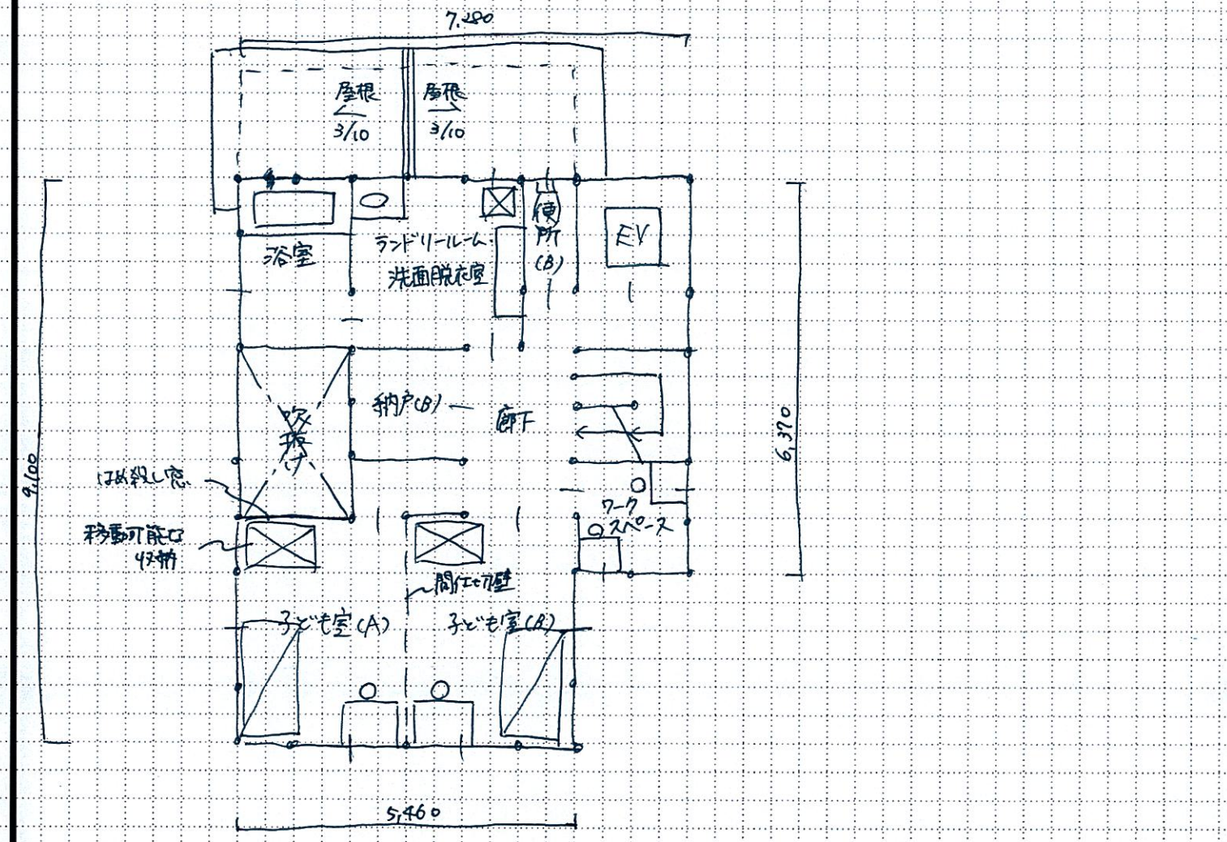


校名	池袋校	学生番号	02800 − 0013 − 0240	受験番号	−	氏名	谷川　真理愛	②

２０２６年度 ２級建築士 プラン復元用紙 〔2/2〕（本試験プランを丁寧に記入しましょう。）

日建学院

「３階平面プラン」を記入してください。（縮尺1／100）

（注）不正確な内容では、皆さんのプランを正しく評価できません。屋根、庇、室名、柱、開口部、寸法等を正確に記入してください。

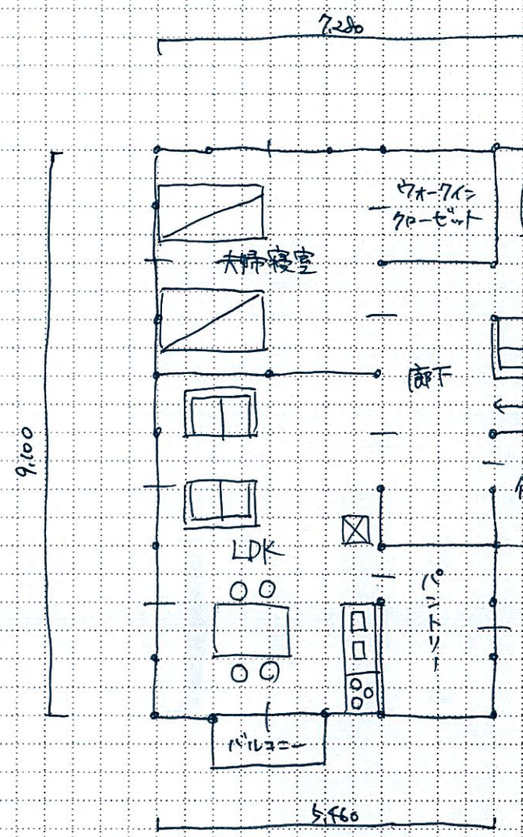

「計画の要点等の回答」を記入してください。

設問①：コワーキングスペース部分は商店側の道路にできる限り寄せて視認性を上げた。一方で，住宅部分は道路から離隔距離を取ることで，セキュリティやプライバシーを確保した。

設問②：子ども室は将来2室合わせてコワーキングスペース部分として活用することを想定し、間仕切壁を外しても整形な室となるようにし，吹抜けの開放感が全体で感じられるよう工夫した。

設問③：住宅部分が200m²以下のため，コワーキングスペース部分と住宅部分の出入口を防火設備として，防火区画した。

いいというようなニュアンスで書きました。

「面積表」を記入してください。（※印は出題された場合に記入してください）

敷地面積			126,00	m²
建築面積		(計算式) 5,46×10,92+1,82×6,37	71,21	m²
床面積	1階	(計算式) 5,46×10,92+1,82×6,37-1,82×1,82	67,90	m²
	2階	(計算式) 5,46×9,1+1,82×6,37-1,82×2,73	56,31	m²
	3階	(計算式) 5,46×9,1+1,82×6,37	61,27	m²
延べ面積			185,49	m²
※建蔽率		建築面積 71,21 ／ 敷地面積 126,00 m²	56,51	%
※容積率		延べ面積 185,49 ／ 敷地面積 126,00 m²	147,21	%

「作業時間・見直しの有無など」を記入してください。

プランニング	60 分	プラン完成後の見直し ☑した □していない
記述・面積表	30 分	作業に要した時間は普段と比べてどうでしたか？ □短い □同じ ☑長い
平面図	分	作業に要した時間は普段と比べてどうでしたか？ □短い □同じ □長い
立面図	180 分	作業に要した時間は普段と比べてどうでしたか？ □短い □同じ □長い
伏　図	分	作業に要した時間は普段と比べてどうでしたか？ □短い □同じ □長い
部分詳細図	分	作業に要した時間は普段と比べてどうでしたか？ □短い □同じ □長い
見直し・仕上げ	30 分	答案完成後の見直し ☑した □していない

「本試験を受験して気になる事」を記入してください。（例：○○の意味が分からなかった。）

・平面図
- 2階吹抜けに面する窓に㊙をかいてしまった。
- フリースペースの採光が，隣地側に窓1つしかない。
- 納戸(A)は下足利用で良いのか？
- 玄関が大きすぎる気がする。


・部分詳細図
- 吹抜けのある部分で切断したので，階高をどうすればいいか分からず，1FLまでしか書いていない。
- 開口部(窓)で切断したが，納まり自信ない。
- GLのコレかき忘れ。

講師記入欄

氏名	谷川 真理愛


「１階平面兼配置プラン」を記入してください。（縮尺1／100）

(注)不正確な内容では、皆さんのプランを正しく評価できません。敷地、屋外施設、室名、柱、開口部、寸法等を正確に記入してください。

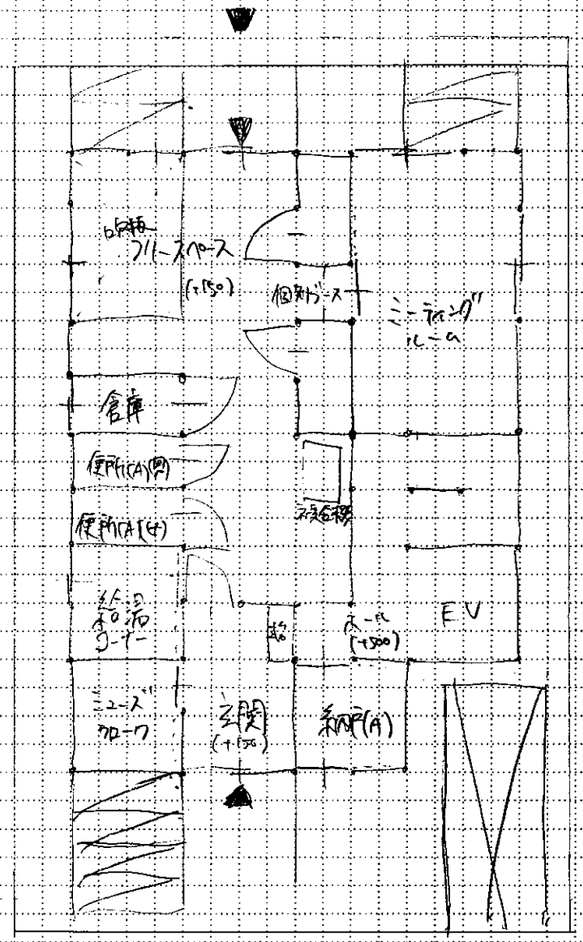

「２階平面プラン」を記入してください。（縮尺1／100）


(注)不正確な内容では、皆さんのプランを正しく評価できません。屋根、庇、室名、柱、開口部、寸法等を正確に記入してください。

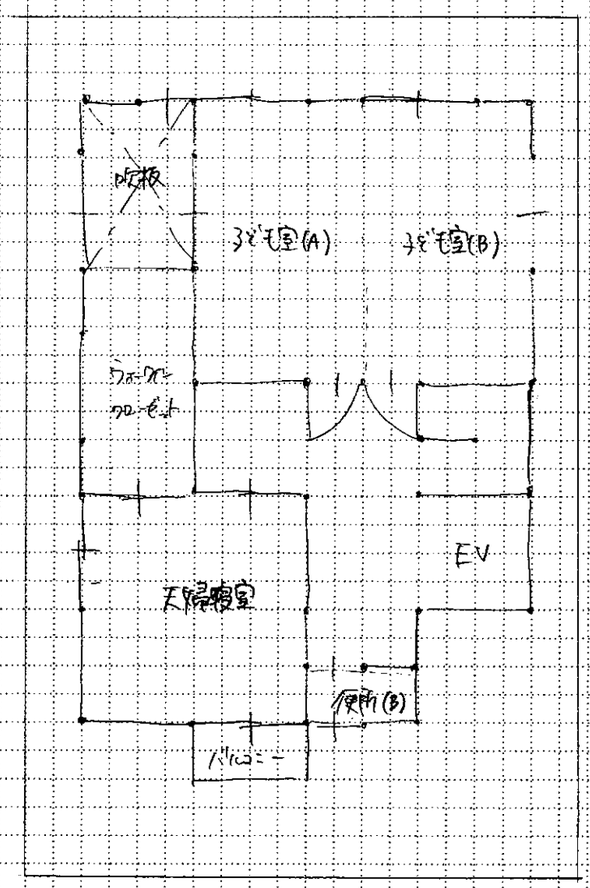

校名		学生番号	－	－	受験番号	－	氏 名	田中伯征

「３階平面プラン」を記入してください。（縮尺1／100）

（注）不正確な内容では、皆さんのプランを正しく評価できません。屋根、庇、室名、柱、開口部、寸法等を正確に記入してください。

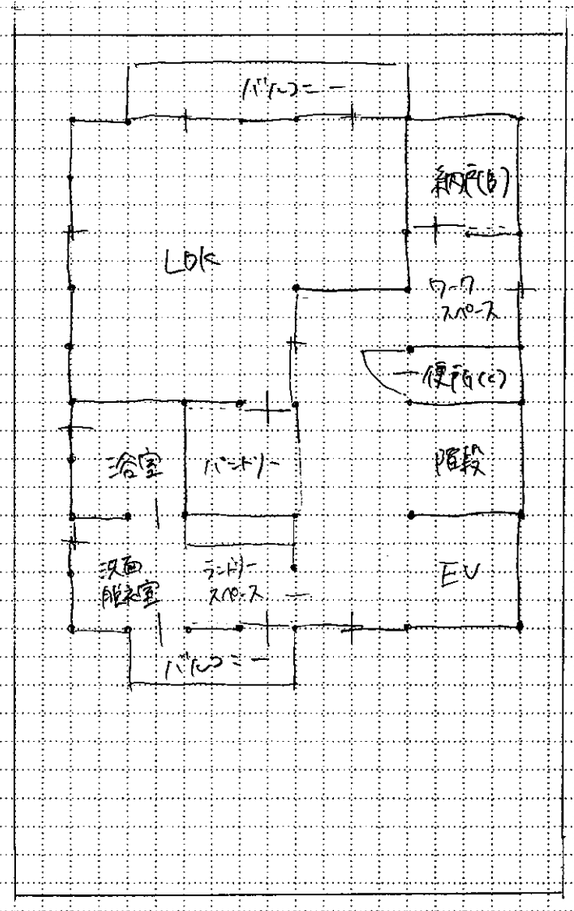

「計画の要点等の回答」を記入してください。

設問①：コワーキングスペース部分を商店街に面するよう設け気軽に利用できるよう計画した。3階のしたには道路面にバルコニーを設け，住宅用入口には門扉を設けてセキュリティとプライベート確保に配慮した。

設問②：子ども室で将来1室で使った際に整形となるよう工夫した。個室の利用も吹抜から採光がとれるよう計画した。

設問③：外壁をRC造の鋼板ネダと遮温防水シートを使うことで耐久構造に配慮した。

「面積表」を記入してください。（※印は出題された場合に記入してください）

敷地面積			126.00 ㎡	
建築面積		(計算式) 7.28×8.19+5.46×1.82	69.56 ㎡	
床面積	1階	(計算式) 7.28×8.19+5.46×1.82	69.56 ㎡	
	2階	(計算式) 7.28×8.19+5.46×1.82 −1.82×2.73	64.59 ㎡	
	3階	(計算式) 7.28×8.19	59.62 ㎡	
延べ面積			193.77 ㎡	
※建蔽率		建築面積 69.56 ／ 敷地面積 126.00 ㎡	55 %	
※容積率		延べ面積 193.77 ／ 敷地面積 126.00 ㎡	153.7%	

「作業時間・見直しの有無など」を記入してください。

プランニング	100 分	プラン完成後の見直し ☑した ☐していない
記述・面積表	15 分	作業に要した時間は普段と比べてどうでしたか？ ☐短い ☑同じ ☐長い
平面図	112 分	作業に要した時間は普段と比べてどうでしたか？ ☐短い ☐同じ ☐長い
立面図	30 分	作業に要した時間は普段と比べてどうでしたか？ ☐短い ☐同じ ☐長い
伏　図	18 分	作業に要した時間は普段と比べてどうでしたか？ ☑短い ☐同じ ☐長い
部分詳細図	20 分	作業に要した時間は普段と比べてどうでしたか？ ☑短い ☐同じ ☐長い
見直し・仕上げ	5 分	答案完成後の見直し ☑した ☐していない

「本試験を受験して気になる事」を記入してください。（例：○○の意味が分からなかった。）


要点③がよくわからなかった。

講師記入欄

氏名 田中佑佳


「１階平面兼配置プラン」を記入してください。（縮尺1／100）

(注) 不正確な内容では、皆さんのプランを正しく評価できません。敷地、屋外施設、室名、柱、開口部、寸法等を正確に記入してください。

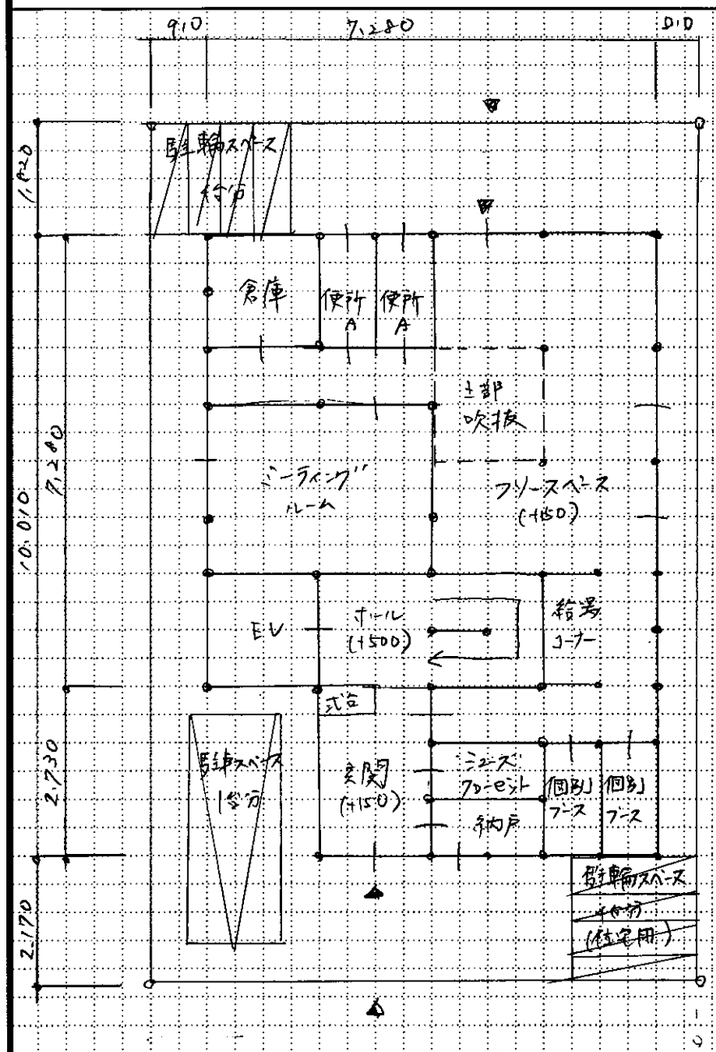

「２階平面プラン」を記入してください。（縮尺1／100）

(注) 不正確な内容では、皆さんのプランを正しく評価できません。屋根、庇、室名、柱、開口部、寸法等を正確に記入してください。

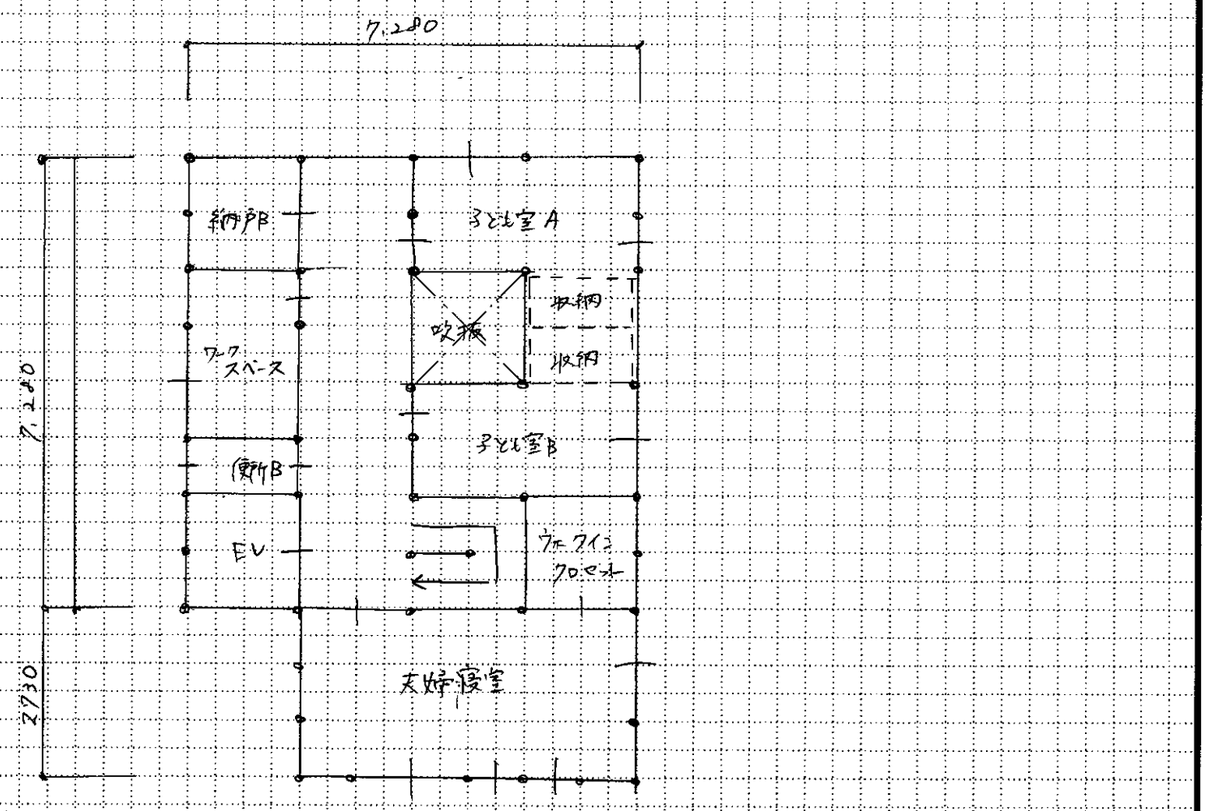


校名	池袋	学生番号	—	—	受験番号	—	氏名	高宮こおり

2026年度 2級建築士 プラン復元用紙 〔2/2〕（本試験プランを丁寧に記入しましょう。）

日建学院

「3階平面プラン」を記入してください。（縮尺1／100）

（注）不正確な内容では、皆さんのプランを正しく評価できません。屋根、庇、室名、柱、開口部、寸法等を正確に記入してください。

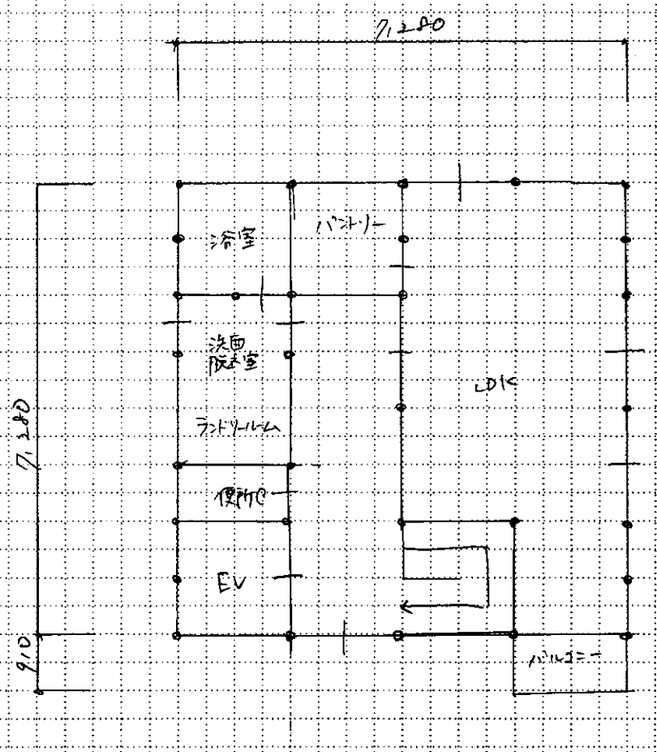

「計画の要点等の回答」を記入してください。

設問①：

コアキングスペースは駐輪場スペースを確保した後、なるべく北側道路に寄せ、集客性に配慮する計画とした。

住宅部分には防犯カメラを設置し、セキュリティーを高める計画とした。

設問②：

子ども室A・Bは移動可能な収納で間仕切ることにより、将来的に一室となる計画とした。

設問③：

主要構造部は準耐火性能を有する構造とした。

また、室内の天井・壁は準不燃性能を有するビニルクロスを仕様した。

「面積表」を記入してください。（※印は出題された場合に記入してください）

敷地面積		126.00		㎡
建築面積		(計算式) (7,28×7,28)+(5,46×2,73)	67.90	㎡
床面積	1階	(計算式) (7,28×7,28)+(5,46×2,73)	67.90	㎡
	2階	(計算式) (7,28×7,28)+(5,46×2,73)−(1,82×1,82)	64.59	㎡
	3階	(計算式) 7,28×7,28	52.99	㎡
延べ面積		185.48		㎡
※建蔽率		建築面積 67.9 ／ 敷地面積 126 ㎡	53	%
※容積率		延べ面積 ／ 敷地面積 126 ㎡	147	%

「作業時間・見直しの有無など」を記入してください。

プランニング	90 分	プラン完成後の見直し ☐した ☑していない
記述・面積表	20 分	作業に要した時間は普段と比べてどうでしたか？ ☐短い ☑同じ ☐長い
平面図	115 分	作業に要した時間は普段と比べてどうでしたか？ ☐短い ☐同じ ☐長い
立面図	20 分	作業に要した時間は普段と比べてどうでしたか？ ☐短い ☑同じ ☐長い
伏　図	30 分	作業に要した時間は普段と比べてどうでしたか？ ☑短い ☐同じ ☐長い
部分詳細図	25 分	作業に要した時間は普段と比べてどうでしたか？ ☐短い ☐同じ ☑長い
見直し・仕上げ	0 分	答案完成後の見直し ☐した ☑していない

「本試験を受験して気になる事」を記入してください。（例：○○の意味が分からなかった。）

・バルコニーの位置が下屋にあたる事に採光的に気づいた

・子ども室や吹抜、住の納戸、シューズクローゼットの広さが足りてない気がする


・ファミリールームの広さ

講師記入欄

氏名 高宮 さおり


「１階平面兼配置プラン」を記入してください。（縮尺1／100）

(注)不正確な内容では、皆さんのプランを正しく評価できません。敷地、屋外施設、室名、柱、開口部、寸法等を正確に記入してください。

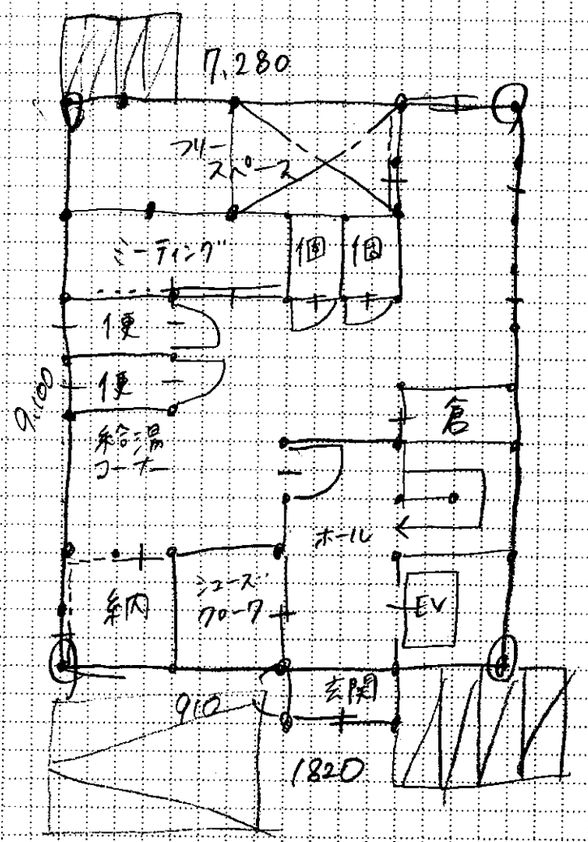

「２階平面プラン」を記入してください。（縮尺1／100）


(注)不正確な内容では、皆さんのプランを正しく評価できません。屋根、庇、室名、柱、開口部、寸法等を正確に記入してください。

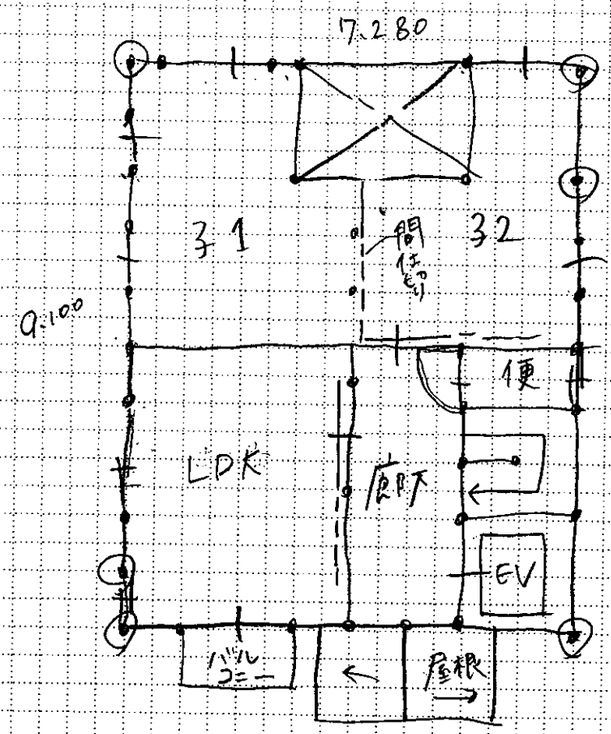

校名		学生番号	—	—	受験番号	—	氏名	渡部 ゆり	

「３階平面プラン」を記入してください。（縮尺1／100）

（注）不正確な内容では、皆さんのプランを正しく評価できません。屋根、庇、室名、柱、開口部、寸法等を正確に記入してください。

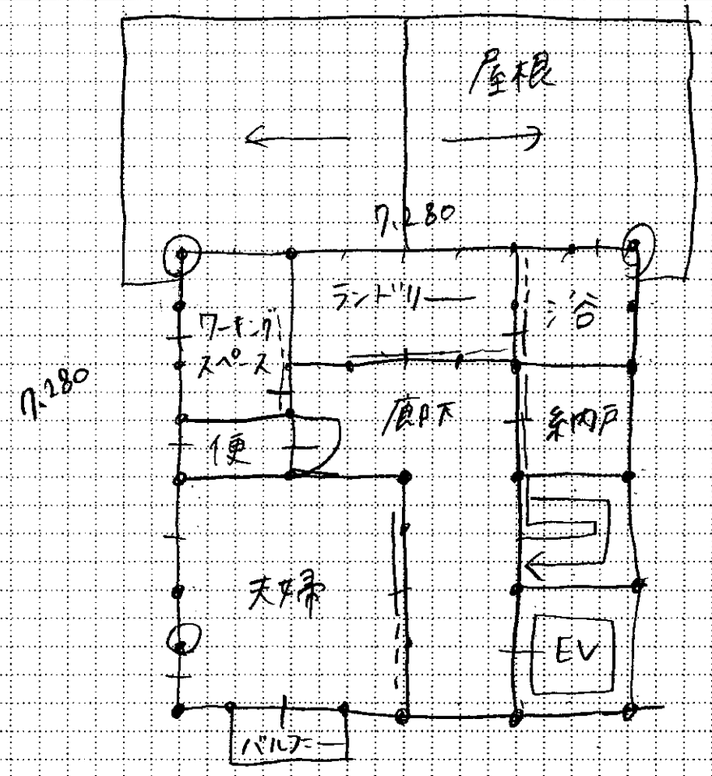

6624

氏名 渡部ひろり

「計画の要点等の回答」を記入してください。

設問①：コワーキングスペースの集客のため、北側にできるだけ併用店舗を寄せた。

設問②：子ども室がコワーキングスペースとなる可能性があるため、2Fに寝室や浴室などのプライベート空間をさけた。南側のLDK寝室にバルコニーをもうけてプライバシー自確保した。

設問③：延べ面積が200㎡以内のためコワーキングスペースから住宅にはいる扉を防火扉とした。

「面積表」を記入してください。（※印は出題された場合に記入してください）

敷地面積			126.00	㎡
建築面積		(計算式) (7.28×9.100)+(1.82×0.91)	67.89	㎡
床面積	1階	(計算式) (7.28×9.100)+(1.82×0.9)	67.89	㎡
	2階	(計算式) (7.28×9.10)−4.95	61.29	㎡
	3階	(計算式) (7.28×7.28)−4.95	48.04	㎡
延べ面積			177.22	㎡
※建蔽率		建築面積 67.89 ／ 敷地面積 126 ㎡	53.8	%
※容積率		延べ面積 177.22 ／ 敷地面積 126 ㎡	140	%

「作業時間・見直しの有無など」を記入してください。

プランニング	120 分	プラン完成後の見直し	☐した ☑していない
記述・面積表	20 分	作業に要した時間は普段と比べてどうでしたか？	☑短い ☐同じ ☐長い
平面図	100 分	作業に要した時間は普段と比べてどうでしたか？	☑短い ☐同じ ☐長い
立面図	20 分	作業に要した時間は普段と比べてどうでしたか？	☐短い ☑同じ ☐長い
伏　図	20 分	作業に要した時間は普段と比べてどうでしたか？	☐短い ☑同じ ☐長い
部分詳細図	20 分	作業に要した時間は普段と比べてどうでしたか？	☐短い ☑同じ ☐長い
見直し・仕上げ	分	答案完成後の見直し	☐した ☑していない


「本試験を受験して気になる事」を記入してください。（例：○○の意味が分からなかった。）

講師記入欄

日建学院


「１階平面兼配置プラン」を記入してください。（縮尺1／100）

(注)不正確な内容では、皆さんのプランを正しく評価できません。敷地、屋外施設、室名、柱、開口部、寸法等を正確に記入してください。

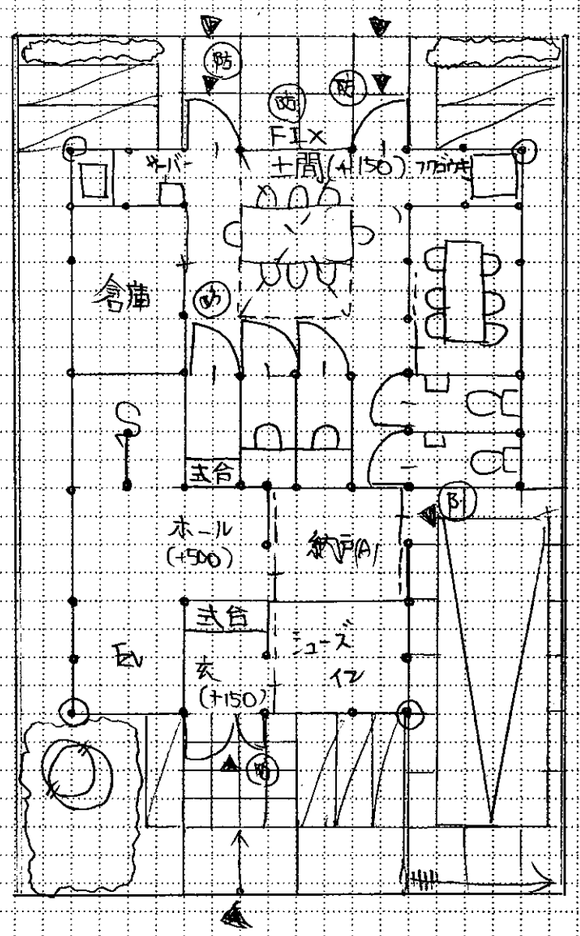

「２階平面プラン」を記入してください。（縮尺1／100）

(注)不正確な内容では、皆さんのプランを正しく評価できません。屋根、庇、室名、柱、開口部、寸法等を正確に記入してください。

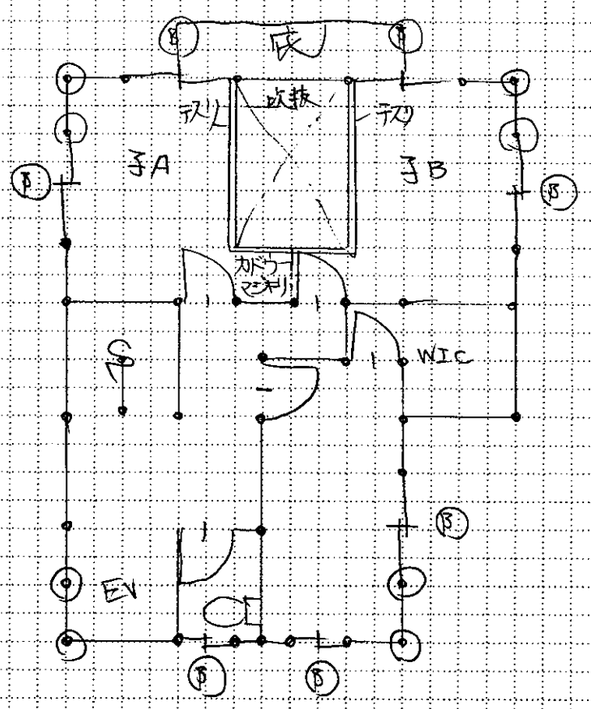


校名	池袋	学生番号	09800 - 0013 - 0219	受験番号	2F-122194	氏名	藤原 俊哉

２０２６年度 ２級建築士 プラン復元用紙 〔2/2〕（本試験プランを丁寧に記入しましょう。）

日建学院

「３階平面プラン」を記入してください。（縮尺1／100）

(注) 不正確な内容では、皆さんのプランを正しく評価できません。屋根、庇、室名、柱、開口部、寸法等を正確に記入してください。

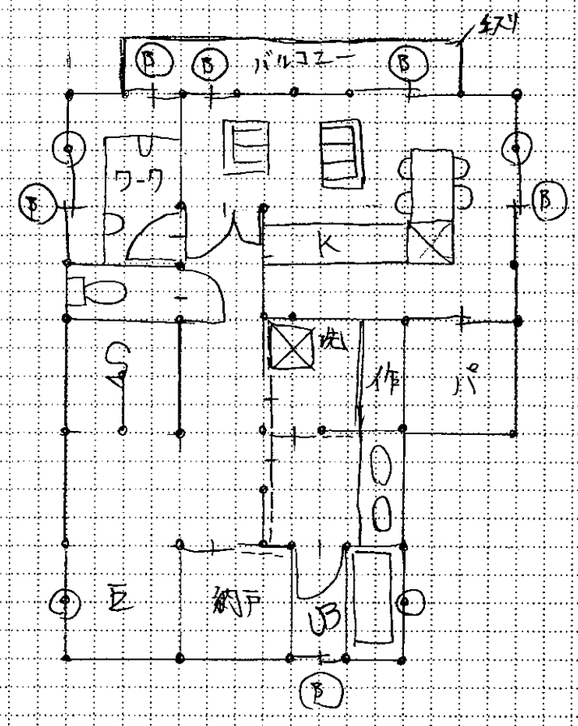

氏名 藤原俊哉

「計画の要点等の回答」を記入してください。

設問①：

設問②：

設問③：

「面積表」を記入してください。（※印は出題された場合に記入してください）

敷地面積		—	m²
建築面積	(計算式)		m²
床面積 1階	(計算式)		m²
床面積 2階	(計算式)		m²
床面積 3階	(計算式)		m²
延べ面積			m²
※建蔽率	建築面積 ／ 敷地面積	m²	%
※容積率	延べ面積 ／ 敷地面積	m²	%

「作業時間・見直しの有無など」を記入してください。

プランニング	60 分	プラン完成後の見直し ☑した ☐していない
記述・面積表	30 分	作業に要した時間は普段と比べてどうでしたか？ ☐短い ☑同じ ☐長い
平面図	120 分	作業に要した時間は普段と比べてどうでしたか？ ☐短い ☐同じ ☑長い
立面図	20 分	作業に要した時間は普段と比べてどうでしたか？ ☑短い ☐同じ ☐長い
伏図	20 分	作業に要した時間は普段と比べてどうでしたか？ ☑短い ☐同じ ☐長い
部分詳細図	30 分	作業に要した時間は普段と比べてどうでしたか？ ☐短い ☐同じ ☑長い
見直し・仕上げ	20 分	答案完成後の見直し ☐した ☐していない

「本試験を受験して気になる事」を記入してください。（例：○○の意味が分からなかった。）


・完成後、30分見直し。　・忘れ物：1Fミニキッチンの天井、立面図のフェンス、
・2F. 吹抜面積は引いた。　立面図の勾配表示。

・感想：廊下を1365とした。フリースペースとリビングルームが狭い。外から納戸に入りにくい。
↳現在気づいた点でした。

講師記入欄


「１階平面兼配置プラン」を記入してください。（縮尺1／100）

(注)不正確な内容では、皆さんのプランを正しく評価できません。敷地、屋外施設、室名、柱、開口部、寸法等を正確に記入してください。

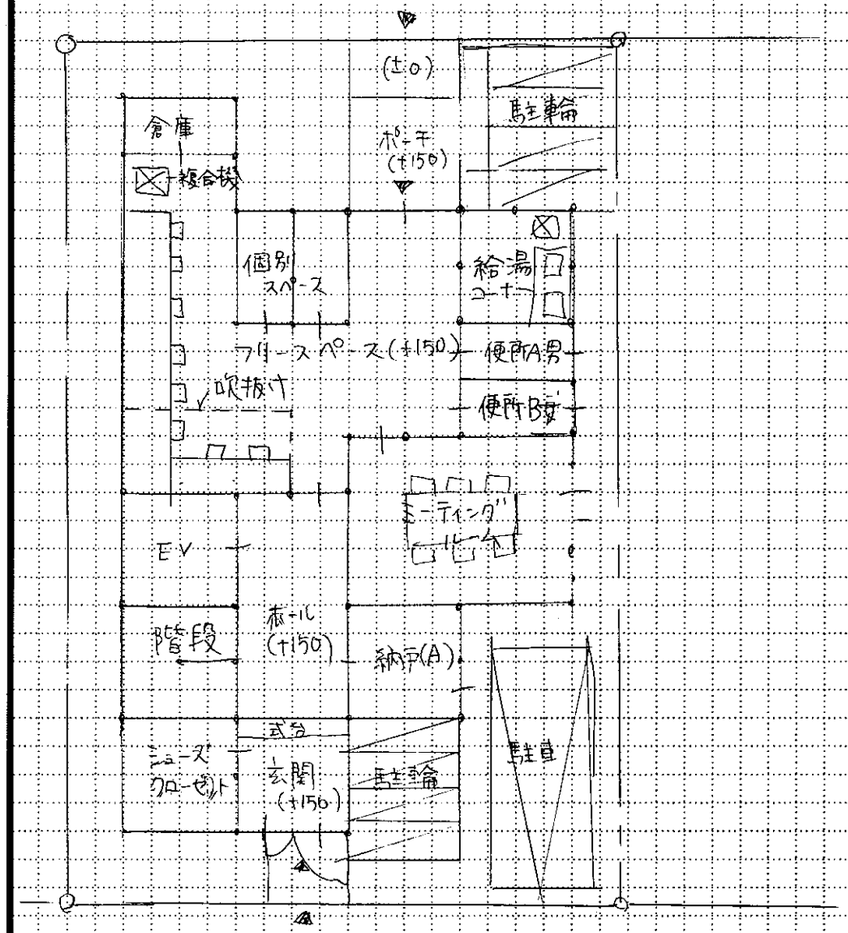

「２階平面プラン」を記入してください。（縮尺1／100）

(注)不正確な内容では、皆さんのプランを正しく評価できません。屋根、庇、室名、柱、開口部、寸法等を正確に記入してください。

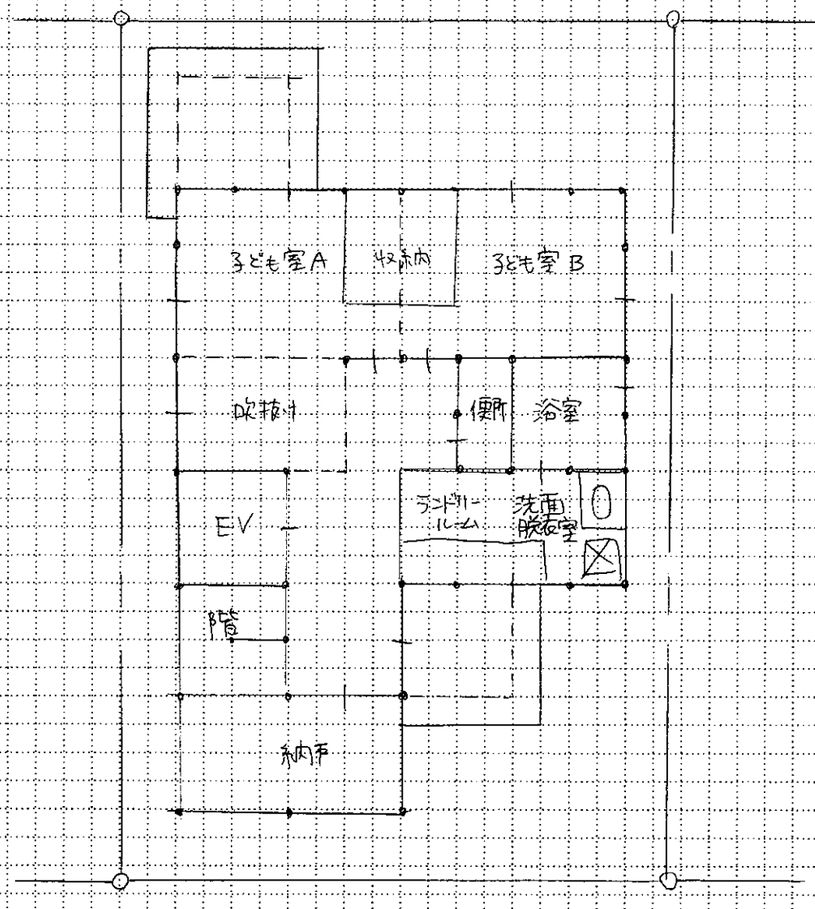


校名	池袋	学生番号	－	－	受験番号	－	氏名	後藤　聡子	②

２０２６年度 ２級建築士 プラン復元用紙 〔2/2〕（本試験プランを丁寧に記入しましょう。）

日建学院

「３階平面プラン」を記入してください。（縮尺1／100）

(注) 不正確な内容では、皆さんのプランを正しく評価できません。屋根、庇、室名、柱、開口部、寸法等を正確に記入してください。

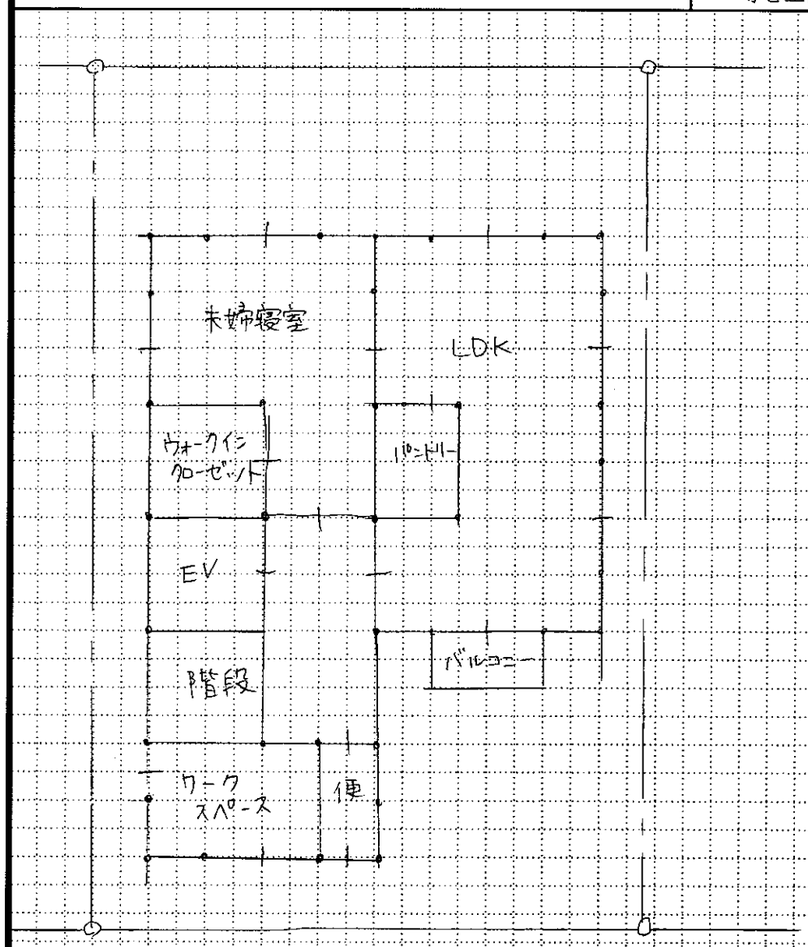

氏名 後藤 聡子

「計画の要点等の回答」を記入してください。

設問①： 出入口を明確に分離し、コワーキングスペース部分と住宅部分を整形に近くまとめることで動線がまじわらないよう計画した

設問②： 将来的にコワーキングスペースとして使用することを想定して、商店街側の北面に計画した。吹抜け部分は階段となることを想定し、2階住宅部分と明確に分離できる配置とした

設問③： 住宅部分の延べ面積が200㎡以下なので、竪穴区画とせず、1階のコワーキング部分と住宅部分を行き来する扉を防火設備とした。

「面積表」を記入してください。（※印は出題された場合に記入してください）

敷地面積		126.00 ㎡	
建築面積	(計算式) 7.28×6.37＋3.64×3.64＋(1.82×1.82)×2	66.24 ㎡	
床面積	1階	(計算式) 7.28×6.37＋3.64×3.64＋(1.82×1.82)×2	66.24 ㎡
	2階	(計算式) 7.28×6.37＋3.64×3.64	59.61 ㎡
	3階	(計算式) 7.28×3.67＋3.64×3.64	59.61 ㎡
延べ面積		185.46 ㎡	
※建蔽率	建築面積 ／ 敷地面積 ㎡		%
※容積率	延べ面積 ／ 敷地面積 ㎡		%

「作業時間・見直しの有無など」を記入してください。

プランニング	80 分	プラン完成後の見直し ☑した ☐していない
記述・面積表	20 分	作業に要した時間は普段と比べてどうでしたか？ ☑短い ☐同じ ☐長い
平面図	分	作業に要した時間は普段と比べてどうでしたか？ ☐短い ☑同じ ☐長い
立面図	分	作業に要した時間は普段と比べてどうでしたか？ ☐短い ☑同じ ☐長い
伏　図	分	作業に要した時間は普段と比べてどうでしたか？ ☐短い ☑同じ ☐長い
部分詳細図	分	作業に要した時間は普段と比べてどうでしたか？ ☐短い ☑同じ ☐長い
見直し・仕上げ	10 分	答案完成後の見直し ☑した ☐していない

「本試験を受験して気になる事」を記入してください。（例：○○の意味が分からなかった。）

吹抜けの表現が指定されていてよくわからなかった。子ども部屋の間仕切壁と可能できる収納の表現もわからなかった。

2階、3階どちらでもいい室を入れるのが難しかった。


プランニング完成後に見直しをしたつもりだったが、1階の倉庫とLDKのパントリーを入れていて後から入れたので無理矢理になった。

床伏の場所をまちがえて描き直したら最初とはかなり違ってしまい多分補強がぬけてる

講師記入欄


「１階平面兼配置プラン」を記入してください。（縮尺1／100）

(注)不正確な内容では、皆さんのプランを正しく評価できません。敷地、屋外施設、室名、柱、開口部、寸法等を正確に記入してください。

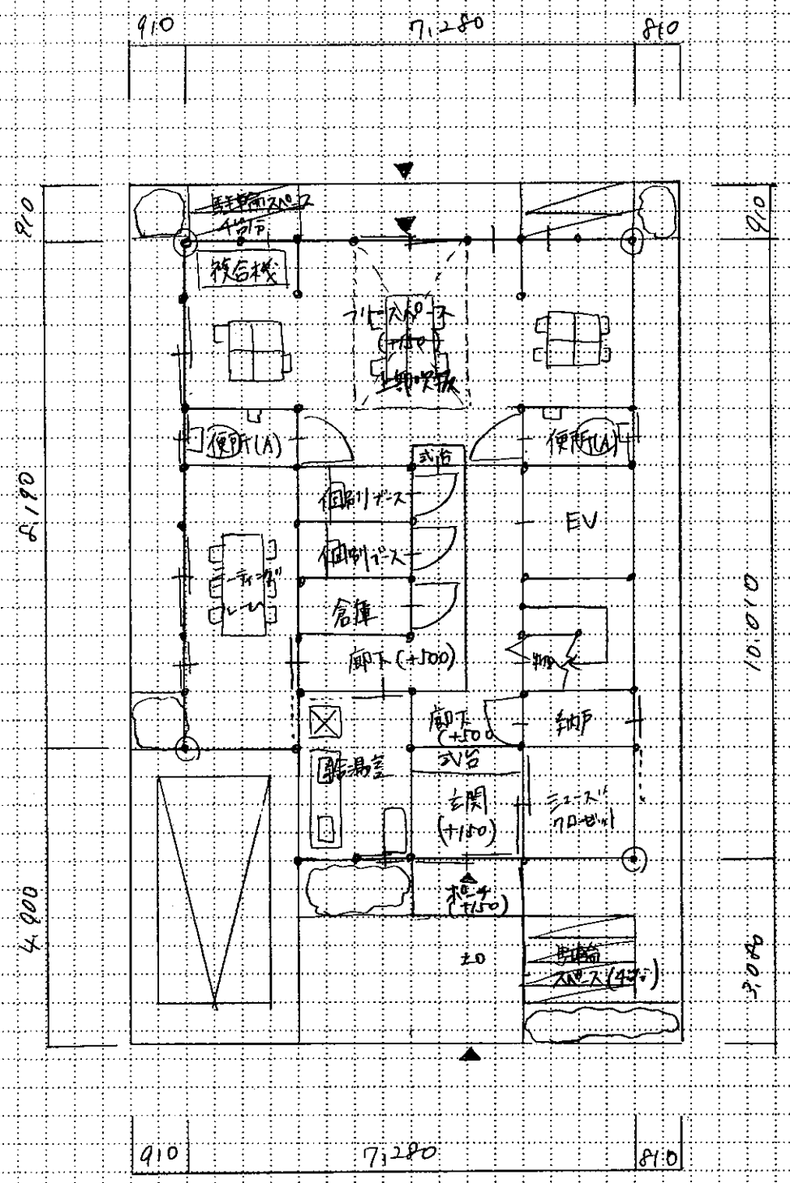

「２階平面プラン」を記入してください。（縮尺1／100）

(注)不正確な内容では、皆さんのプランを正しく評価できません。屋根、庇、室名、柱、開口部、寸法等を正確に記入してください。

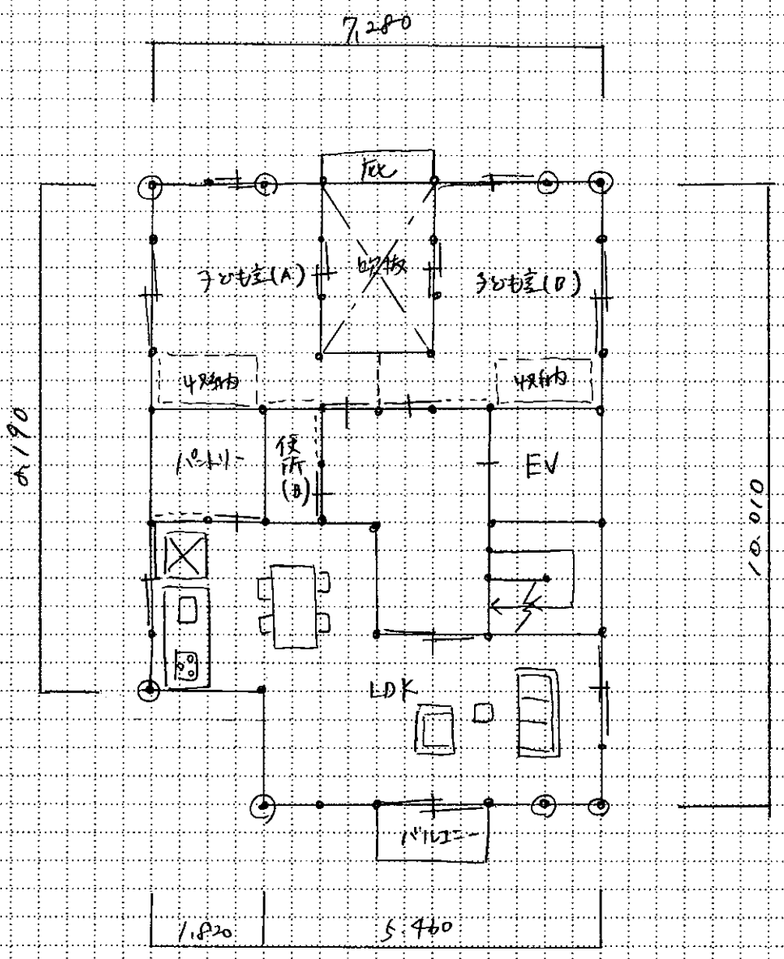


校名	池袋	学生番号	02800 － 0013 － 0202	受験番号	2F － 21446L	氏名	和田 未穂心	②

2026年度 2級建築士 プラン復元用紙 〔2/2〕（本試験プランを丁寧に記入しましょう。）

日建学院

「3階平面プラン」を記入してください。（縮尺1／100）

（注）不正確な内容では、皆さんのプランを正しく評価できません。屋根、庇、室名、柱、開口部、寸法等を正確に記入してください。

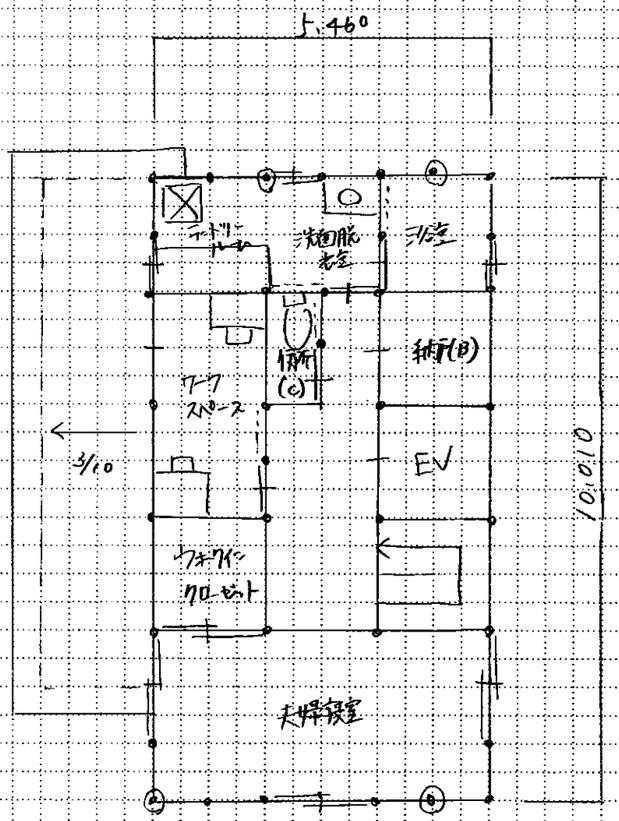

「計画の要点等の回答」を記入してください。

設問①：
コワーキングスペースと北側道路の離隔をとることで、利用者が気軽に入りやすいようにした。また、コワーキングスペース部分と住宅部分の間には金属性の間仕切扉を設け、住宅部分のセキュリティやプライバシーに配慮した。

設問②：
子ども室に吹抜を面するように配置し、採光コワーキングスペースとして利用する際にも一体感があるようにした。また、2部屋とも角部屋とし、子ども室としてはもちろん、コワーキングスペースとしても十分な採光がとれるように窓を2面に設けた。

設問③：
延焼のおそれのある部分には防火設備を設け、商店街にも被害が広がりにくい準耐火建築とした。

「面積表」を記入してください。（※印は出題された場合に記入してください）

敷地面積		126 m²	
建築面積		(計算式) (5.46×10.01)+(1.82×8.19)	69.56 m²
床面積	1階	(計算式) (5.46×10.01)+(1.82×8.19)	69.56 m²
	2階	(計算式) (5.46×10.01)+(1.82×8.19)−(1.82×2.73)	64.60 m²
	3階	(計算式) 5.46×10.01	54.65 m²
延べ面積		188.81 m²	
※建蔽率		建築面積 69.56 ／ 敷地面積 126 m²	55.20 %
※容積率		延べ面積 188.81 ／ 敷地面積 126 m²	149.84 %

「作業時間・見直しの有無など」を記入してください。

プランニング	90 分	プラン完成後の見直し ☑した ☐していない
記述・面積表	15 分	作業に要した時間は普段と比べてどうでしたか？ ☐短い ☑同じ ☐長い
平面図	60 分	作業に要した時間は普段と比べてどうでしたか？ ☐短い ☑同じ ☐長い
立面図	20 分	作業に要した時間は普段と比べてどうでしたか？ ☐短い ☑同じ ☐長い
伏図	15 分	作業に要した時間は普段と比べてどうでしたか？ ☑短い ☐同じ ☐長い
部分詳細図	25 分	作業に要した時間は普段と比べてどうでしたか？ ☐短い ☐同じ ☑長い
見直し・仕上げ	30 分	答案完成後の見直し ☑した ☐していない

「本試験を受験して気になる事」を記入してください。（例：○○の意味が分からなかった。）

・「子ども室2つを隣接させる」とあるが、一部隣接していればOKなのか？


・東西方向の延焼ラインが全範囲に及ぶ場合、(防)は全開口部につけていいのか？

講師記入欄

氏名 池袋 和田未穂


「１階平面兼配置プラン」を記入してください。（縮尺1／100）

(注)不正確な内容では、皆さんのプランを正しく評価できません。敷地、屋外施設、室名、柱、開口部、寸法等を正確に記入してください。

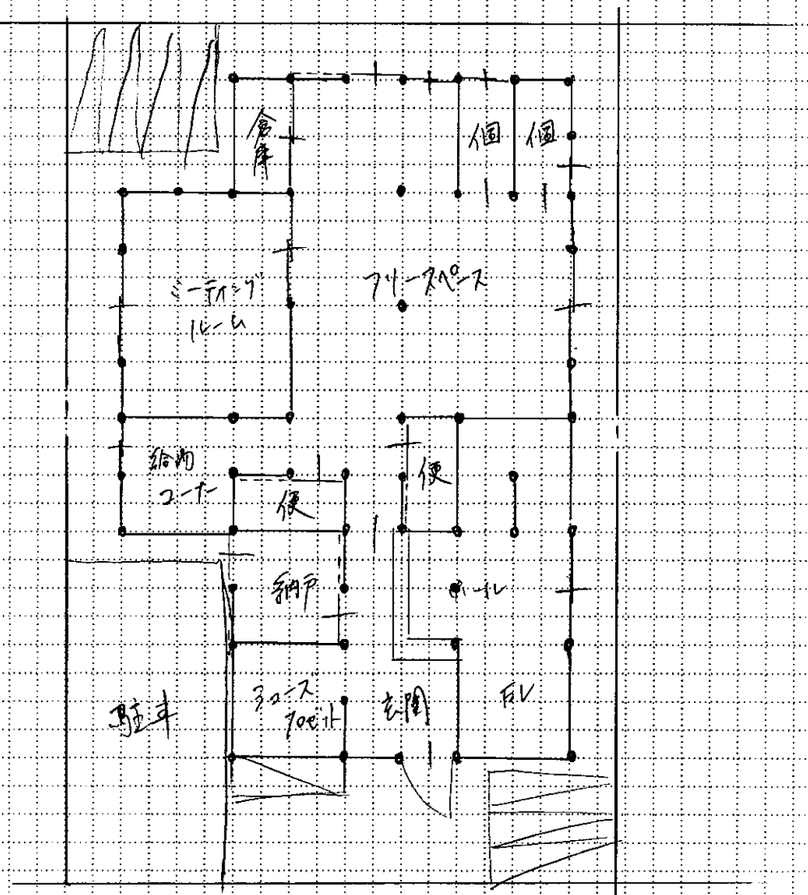

「２階平面プラン」を記入してください。（縮尺1／100）

(注)不正確な内容では、皆さんのプランを正しく評価できません。屋根、庇、室名、柱、開口部、寸法等を正確に記入してください。

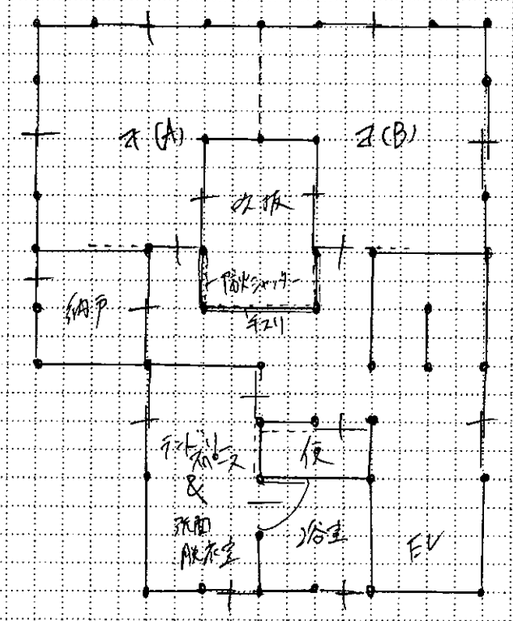


校名		学生番号	—	—	受験番号	—	氏名	金丸 龍子

日建学院

「３階平面プラン」を記入してください。（縮尺1／100）

(注)不正確な内容では、皆さんのプランを正しく評価できません。屋根、庇、室名、柱、開口部、寸法等を正確に記入してください。

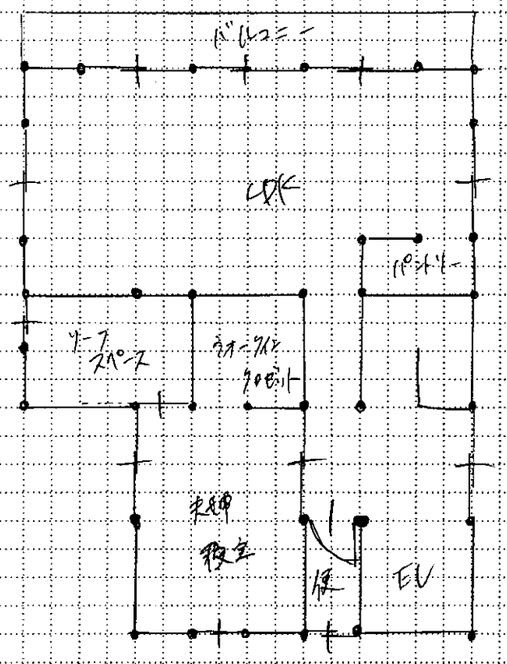

「計画の要点等の回答」を記入してください。

設問①：視認性を高めるために、道路とコワーキングスペースとの距離を短くした。住宅への通り土を1箇所（玄関）にし、塀で囲った。

設問②：子ども室が出窓だけでなく、廊下からも吹抜けに面するようにした。
（子ども室の将来対応は、意味を取り違えて記述してしまいました。）

設問③：近隣のかぶれのある部分に所定の防火設備を設けた。
廊下と吹抜けが面する所に、防火シャッターを設けた。

「面積表」を記入してください。（※印は出題された場合に記入してください）

敷地面積				m²
建築面積		(計算式) 5.75×10.02+1.22×5.76	69.55	m²
床面積	1階	(計算式) 5.75×10.02+1.22×5.76	69.55	m²
	2階	(計算式) 7.22×5.76+5.76×3.69−1.22×2.55	57.14	m²
	3階	(計算式) 7.22×5.76+5.76×2.69	59.61	m²
延べ面積			186.3	m²
※建蔽率		建築面積 ／ 敷地面積 m²		%
※容積率		延べ面積 ／ 敷地面積 m²		%

「作業時間・見直しの有無など」を記入してください。

プランニング	60 分	プラン完成後の見直し	☑した ☐していない
記述・面積表	30 分	作業に要した時間は普段と比べてどうでしたか？	☐短い ☐同じ ☑長い
平面図	60 分	作業に要した時間は普段と比べてどうでしたか？	☐短い ☑同じ ☐長い
立面図	30 分	作業に要した時間は普段と比べてどうでしたか？	☐短い ☑同じ ☐長い
伏図	30 分	作業に要した時間は普段と比べてどうでしたか？	☐短い ☐同じ ☐長い
部分詳細図	60 分	作業に要した時間は普段と比べてどうでしたか？	☐短い ☐同じ ☑長い
見直し・仕上げ	30 分	答案完成後の見直し	☑した ☐していない


「本試験を受験して気になる事」を記入してください。（例：○○の意味が分からなかった。）

講師記入欄

氏名 金井 恵子


「１階平面兼配置プラン」を記入してください。（縮尺1／100）

(注)不正確な内容では、皆さんのプランを正しく評価できません。敷地、屋外施設、室名、柱、開口部、寸法等を正確に記入してください。

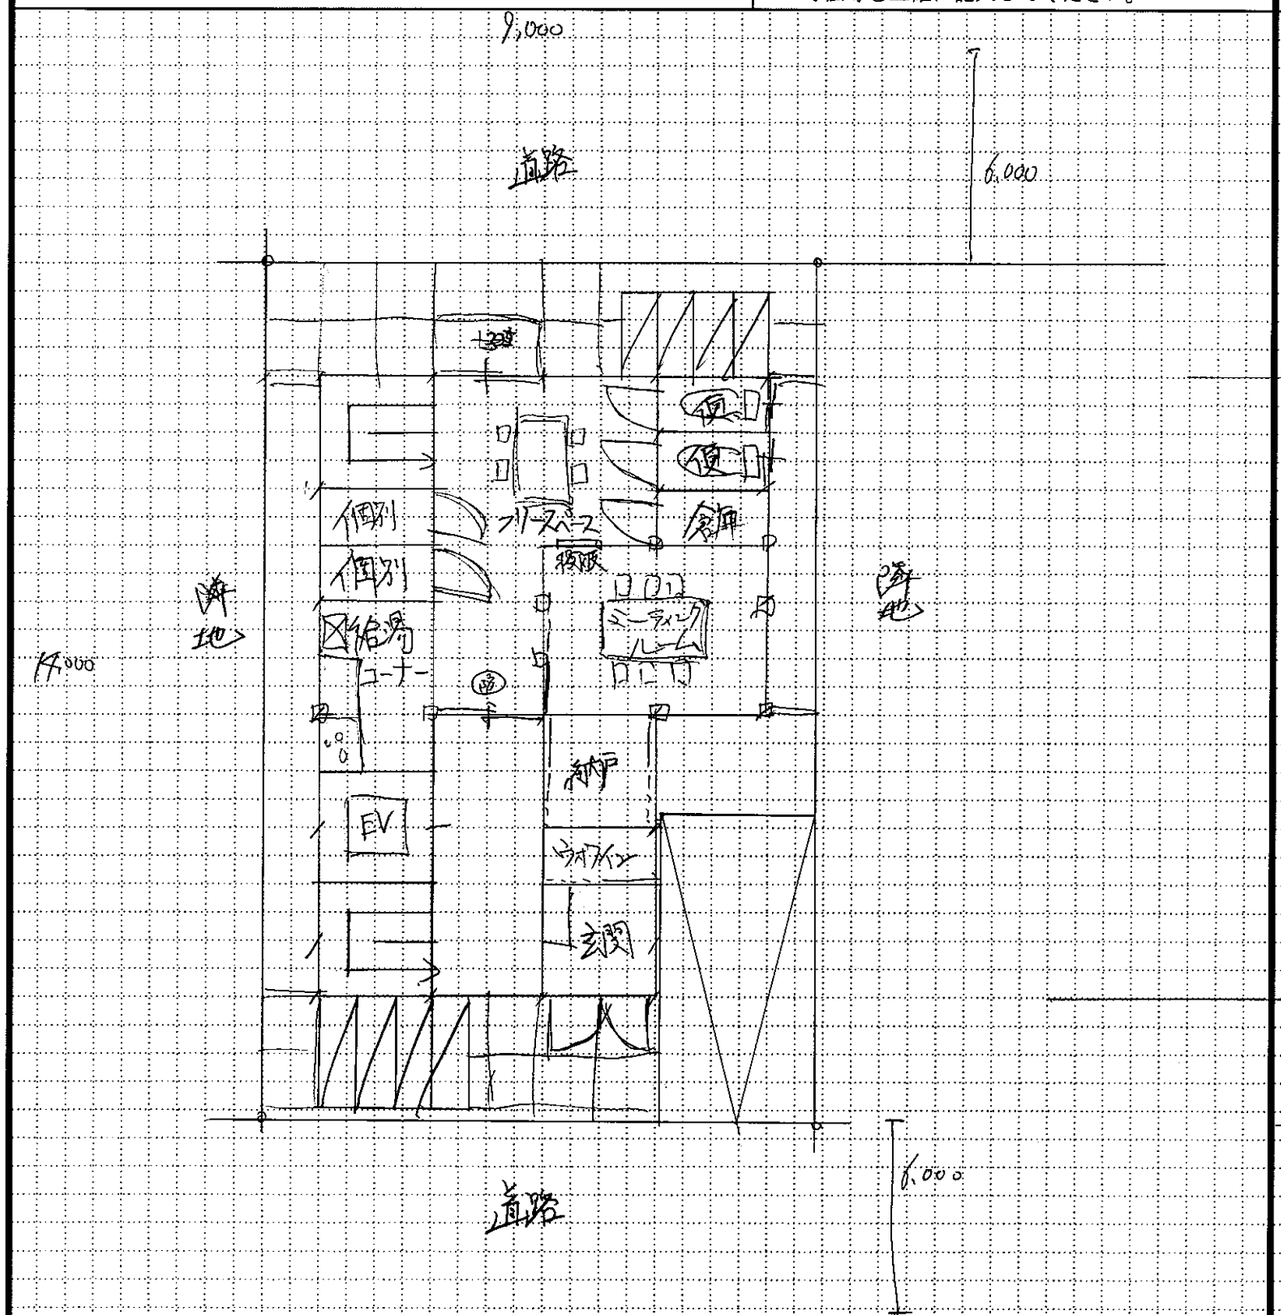

「２階平面プラン」を記入してください。（縮尺1／100）


(注)不正確な内容では、皆さんのプランを正しく評価できません。屋根、庇、室名、柱、開口部、寸法等を正確に記入してください。

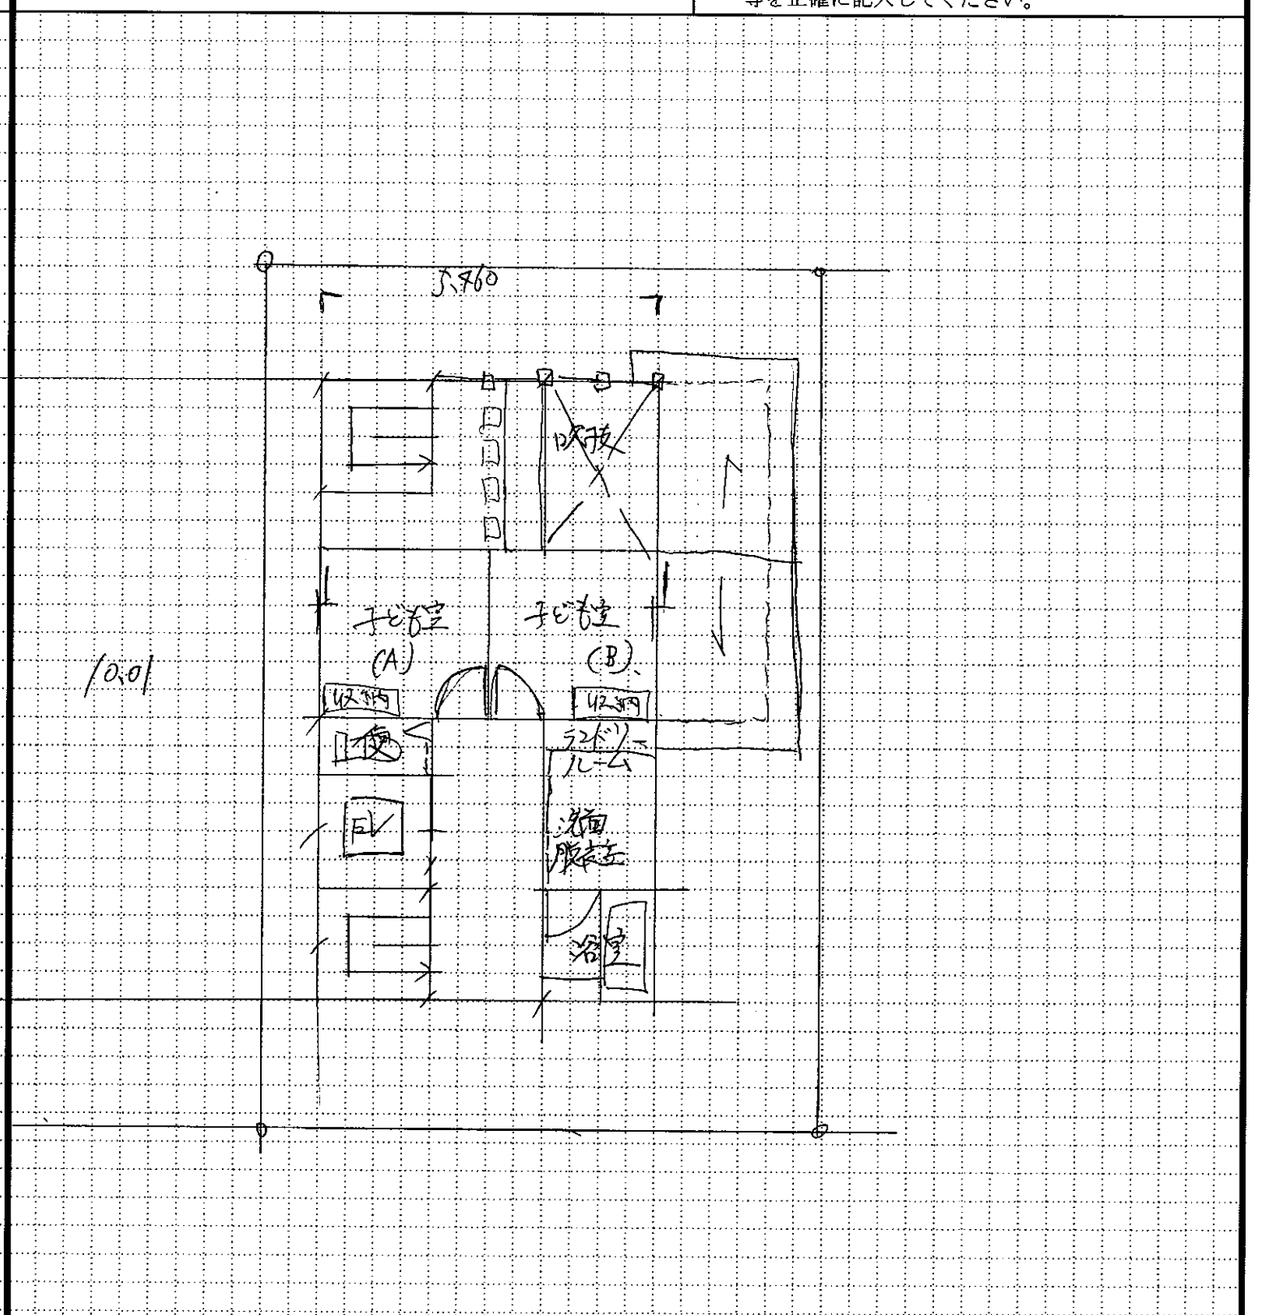

校名	池袋	学生番号	02800 − 0013 − 0201	受験番号	2F − 207567	氏名	南水裕貴

「３階平面プラン」を記入してください。（縮尺1／100）

(注)不正確な内容では、皆さんのプランを正しく評価できません。屋根、庇、室名、柱、開口部、寸法等を正確に記入してください。

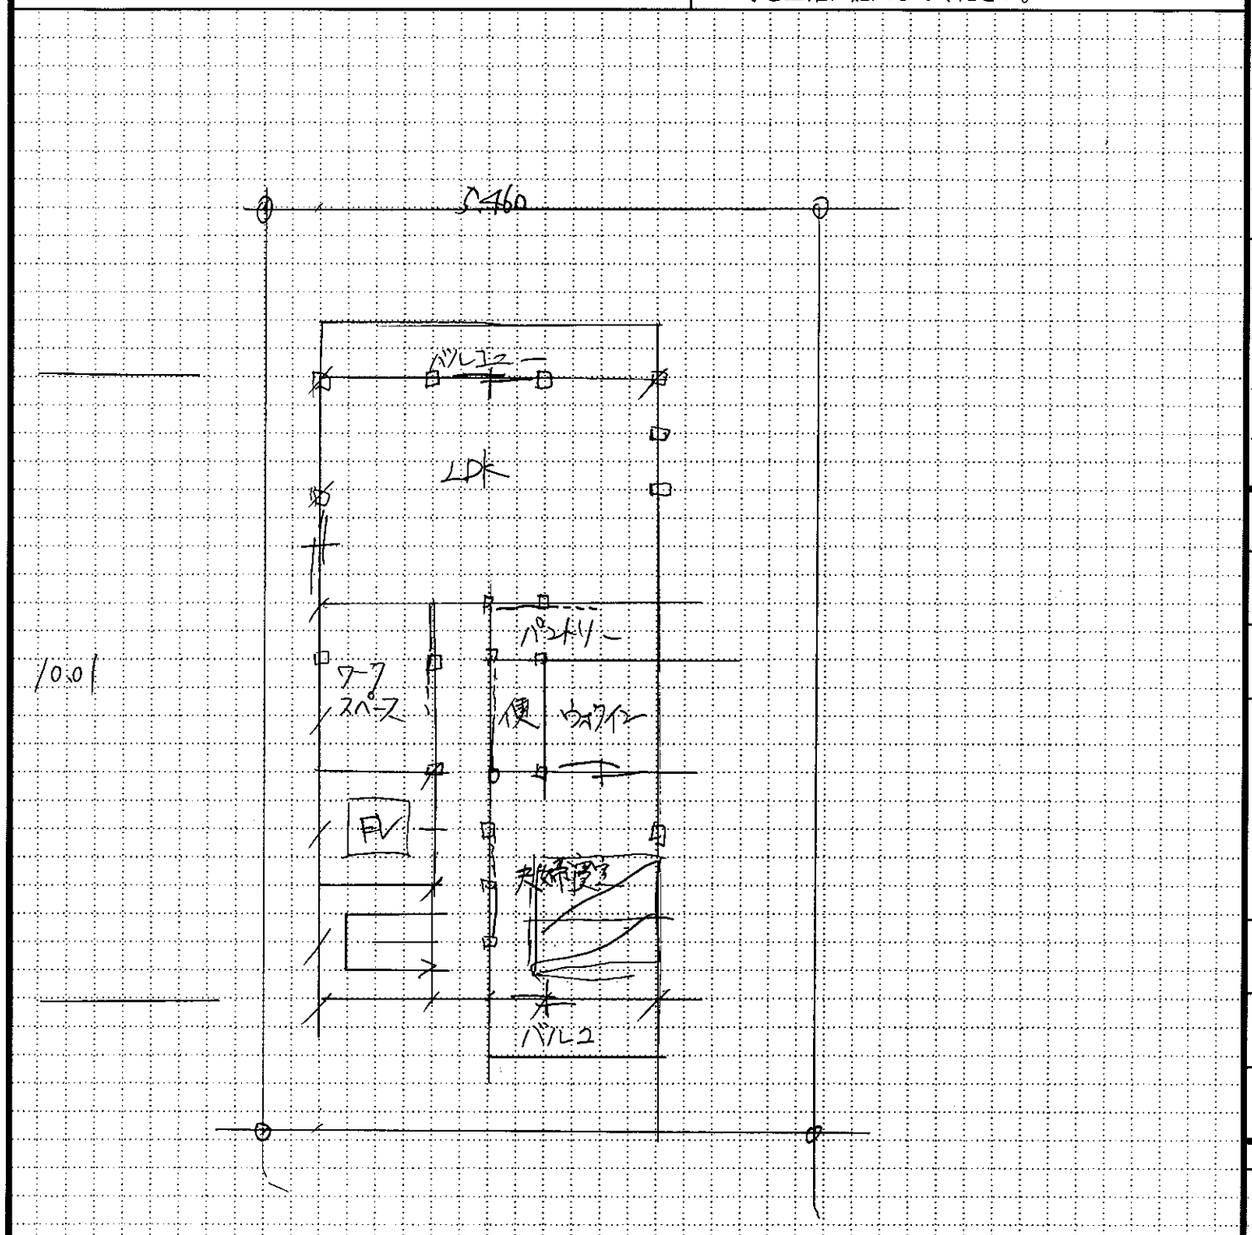

氏名 高木裕貴

「計画の要点等の回答」を記入してください。

設問①：

設問②：

設問③：

「面積表」を記入してください。（※印は出題された場合に記入してください）

敷地面積			126,00	㎡
建築面積		(計算式) (5,46×7,28)+(4,55×5,46)	64,59	㎡
床面積	1階	(計算式) (5,46×7,28)+(4,55×5,46)	64,59	㎡
	2階	(計算式) (10,01×5,46)−(2,73×1,82)	49,68	㎡
	3階	(計算式) (10,01×5,46)	54,65	㎡
延べ面積			168,92	㎡
※建蔽率		建築面積 64,59 ／ 敷地面積 126 ㎡	51	%
※容積率		延べ面積 168,92 ／ 敷地面積 126 ㎡	134	%

「作業時間・見直しの有無など」を記入してください。


プランニング	80 分	プラン完成後の見直し ☐した ☑していない
記述・面積表	15 分	作業に要した時間は普段と比べてどうでしたか？ ☑短い ☐同じ ☐長い
平面図	135 分	作業に要した時間は普段と比べてどうでしたか？ ☐短い ☐同じ ☐長い
立面図	20 分	作業に要した時間は普段と比べてどうでしたか？ ☐短い ☑同じ ☐長い
伏　図	15 分	作業に要した時間は普段と比べてどうでしたか？ ☑短い ☐同じ ☐長い
部分詳細図	20 分	作業に要した時間は普段と比べてどうでしたか？ ☐短い ☑同じ ☐長い
見直し・仕上げ	15 分	答案完成後の見直し ☐した ☑していない

「本試験を受験して気になる事」を記入してください。（例：○○の意味が分からなかった。）

講師記入欄


「１階平面兼配置プラン」を記入してください。（縮尺1／100）

(注)不正確な内容では、皆さんのプランを正しく評価できません。敷地、屋外施設、室名、柱、開口部、寸法等を正確に記入してください。

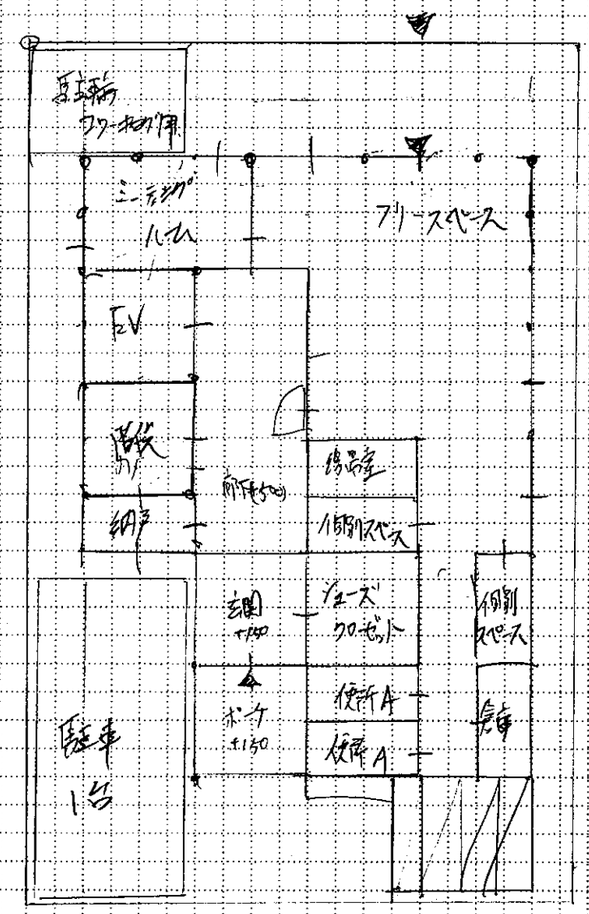

「２階平面プラン」を記入してください。（縮尺1／100）


(注)不正確な内容では、皆さんのプランを正しく評価できません。屋根、庇、室名、柱、開口部、寸法等を正確に記入してください。

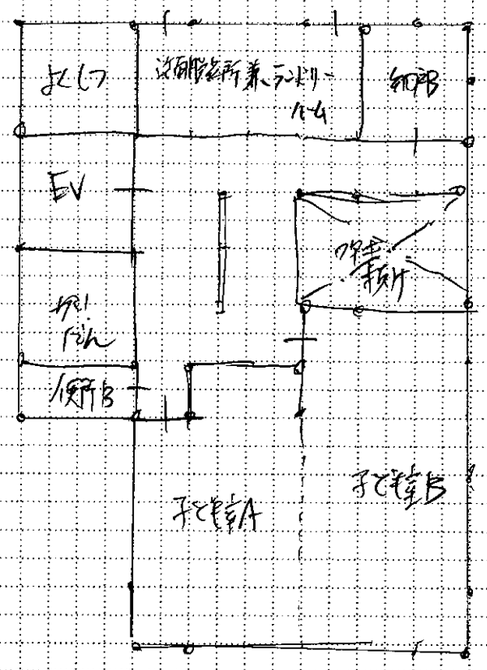

校名	池袋校	学生番号	02800 - 0013 - 0232	受験番号	2D - 11969	氏名	小野寺	2

「３階平面プラン」を記入してください。（縮尺1／100）

（注）不正確な内容では、皆さんのプランを正しく評価できません。屋根、庇、室名、柱、開口部、寸法等を正確に記入してください。

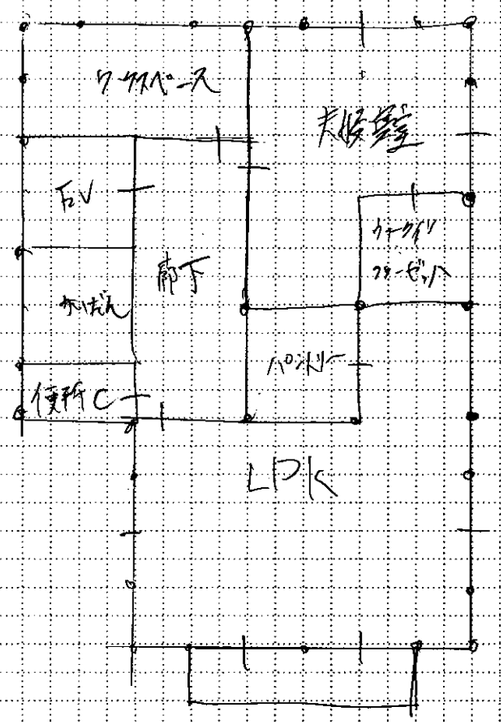

氏名 小野寺也

「計画の要点等の回答」を記入してください。

設問①：北側の開口部を広く設け、道路からのコワーキングスペースの視認性を高め気軽に利用できるようにした。南側の住宅部分のアプローチにおいて玄関までの敷地内通路を確保しプライバシーに配慮した性に配慮した。

設問②：子ども室を南に窓を設け、部屋の内部から吹抜けを見下ろせる計画にした。子ども室A,Bを将来一つの部屋にできるよう間仕切りの配置を考えた。

設問③：1階の隣地境界線と道路中心線から3,000、2階は5,000の延焼の恐れのあるラインに含まれる開口部には防火設備を用いた。

「面積表」を記入してください。（※印は出題された場合に記入してください）

敷地面積			126.00	㎡
建築面積		(計算式) (6,37×7,28)+(3,64×5,46)	66.24	㎡
床面積	1階	(計算式) (6,37×7,28)+(3,64×5,46)-(1,82×1,82)	62.93	㎡
	2階	(計算式) (6,37×7,28)+(3,64×5,46)-(1,82×2,73)	61.27	㎡
	3階	(計算式) (6,37×7,28)+(3,64×5,46)	66.24	㎡
延べ面積			190.44	㎡
※建蔽率		建築面積 / 敷地面積 126 ㎡	52.5	%
※容積率		延べ面積 / 敷地面積 190.44 / 126 ㎡	151	%

「作業時間・見直しの有無など」を記入してください。

プランニング	75 分	プラン完成後の見直し	☑した ☐していない
記述・面積表	15 分	作業に要した時間は普段と比べてどうでしたか？	☑短い ☐同じ ☑長い
平面図	130 分	作業に要した時間は普段と比べてどうでしたか？	☐短い ☐同じ ☑長い
立面図	20 分	作業に要した時間は普段と比べてどうでしたか？	☐短い ☐同じ ☐長い
伏図	20 分	作業に要した時間は普段と比べてどうでしたか？	☑短い ☐同じ ☐長い
部分詳細図	20 分	作業に要した時間は普段と比べてどうでしたか？	☐短い ☐同じ ☐長い
見直し・仕上げ	5 分	答案完成後の見直し	☑した ☐していない


「本試験を受験して気になる事」を記入してください。（例：○○の意味が分からなかった。）

立面の屋根勾配、伏図の火打記入ミス

講師記入欄


「１階平面兼配置プラン」を記入してください。（縮尺1／100）

(注)不正確な内容では、皆さんのプランを正しく評価できません。敷地、屋外施設、室名、柱、開口部、寸法等を正確に記入してください。

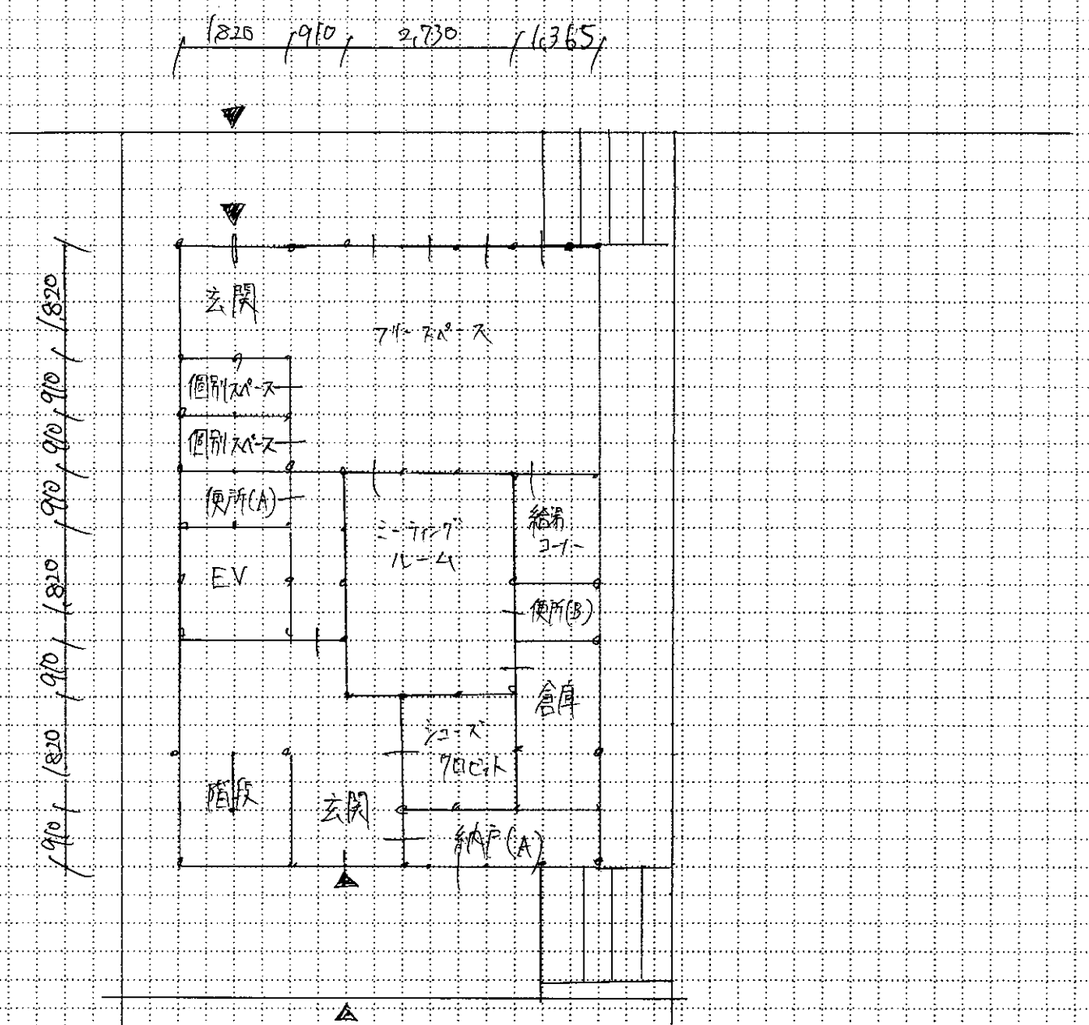

「２階平面プラン」を記入してください。（縮尺1／100）


(注)不正確な内容では、皆さんのプランを正しく評価できません。屋根、庇、室名、柱、開口部、寸法等を正確に記入してください。

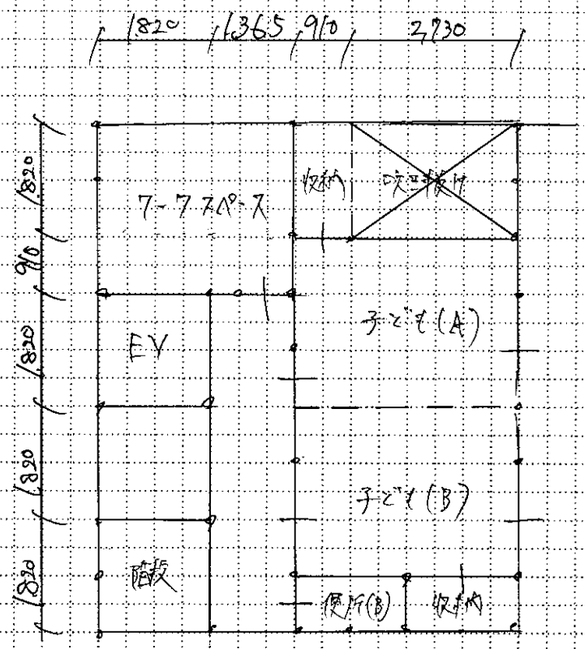

校名		学生番号	—	—	受験番号	2F — 151140	氏名	高橋	

「３階平面プラン」を記入してください。（縮尺1／100）

(注)不正確な内容では、皆さんのプランを正しく評価できません。屋根、庇、室名、柱、開口部、寸法等を正確に記入してください。

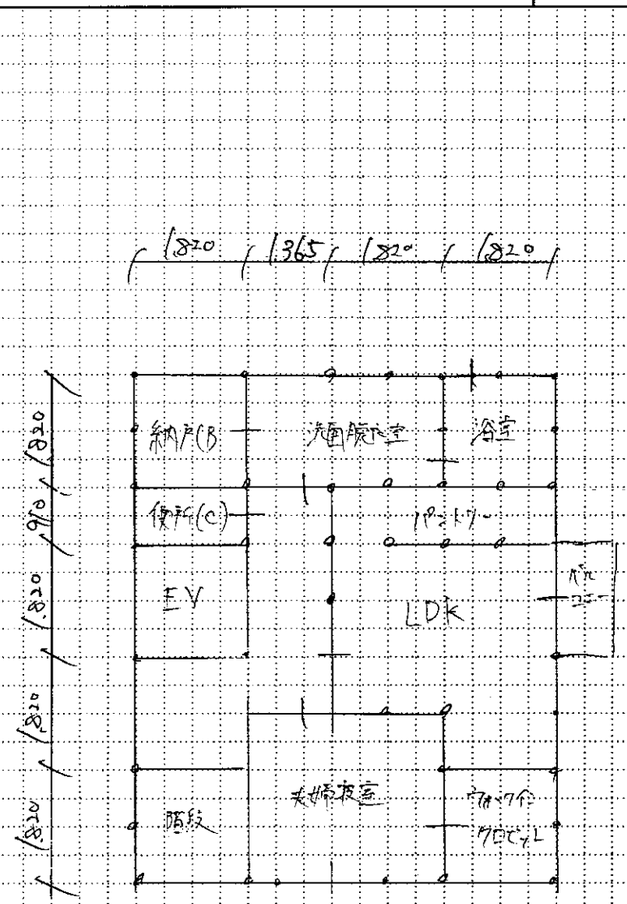

「計画の要点等の回答」を記入してください。

設問①：

・フリースペースを北側に配置したことで、通り抜けの目立ちにくい、視認性を向上した。

設問②：

・子ども室1と子ども室2、吹き抜けを一直線に配置することで、コワーキングスペースとして~~兼用することで~~使用する際に大空間となるよう計画した。

設問③：

・耐力壁を上下階にバランスよく配置することで、強い建物にした。

「面積表」を記入してください。（※印は出題された場合に記入してください）

敷地面積			m^2	
建築面積	(計算式) (6.825 × 10.01)		68.31	m^2
床面積 1階	(計算式) (6.825×10.01)		68.31	m^2
床面積 2階	(計算式) (6.825×8.19) - (2.73×1.82)		50.92	m^2
床面積 3階	(計算式) (6.825×8.19)		55.89	m^2
延べ面積			175.12	m^2
※建蔽率	建築面積 ／ 敷地面積	m^2		%
※容積率	延べ面積 ／ 敷地面積	m^2		%

「作業時間・見直しの有無など」を記入してください。

プランニング	75 分	プラン完成後の見直し □した □していない
記述・面積表	20 分	作業に要した時間は普段と比べてどうでしたか？ □ 短い □ 同じ □ 長い
平面図	120 分	作業に要した時間は普段と比べてどうでしたか？ □ 短い □ 同じ □ 長い
立面図	25 分	作業に要した時間は普段と比べてどうでしたか？ □ 短い □ 同じ □ 長い
伏 図	30 分	作業に要した時間は普段と比べてどうでしたか？ □ 短い □ 同じ □ 長い
部分詳細図	30 分	作業に要した時間は普段と比べてどうでしたか？ □ 短い □ 同じ □ 長い
見直し・仕上げ	0 分	答案完成後の見直し □した □していない

「本試験を受験して気になる事」を記入してください。（例：○○の意味が分からなかった。）

・駐車スペース書き忘れたら一発アウトなの？

講師記入欄


氏名 高橋 昊吾

２０２６年度 ２級建築士 プラン復元用紙 〔1/2〕（本試験プランを丁寧に記入しましょう。）

日建学院


「１階平面兼配置プラン」を記入してください。（縮尺1／100）

（注）不正確な内容では、皆さんのプランを正しく評価できません。敷地、屋外施設、室名、柱、開口部、寸法等を正確に記入してください。

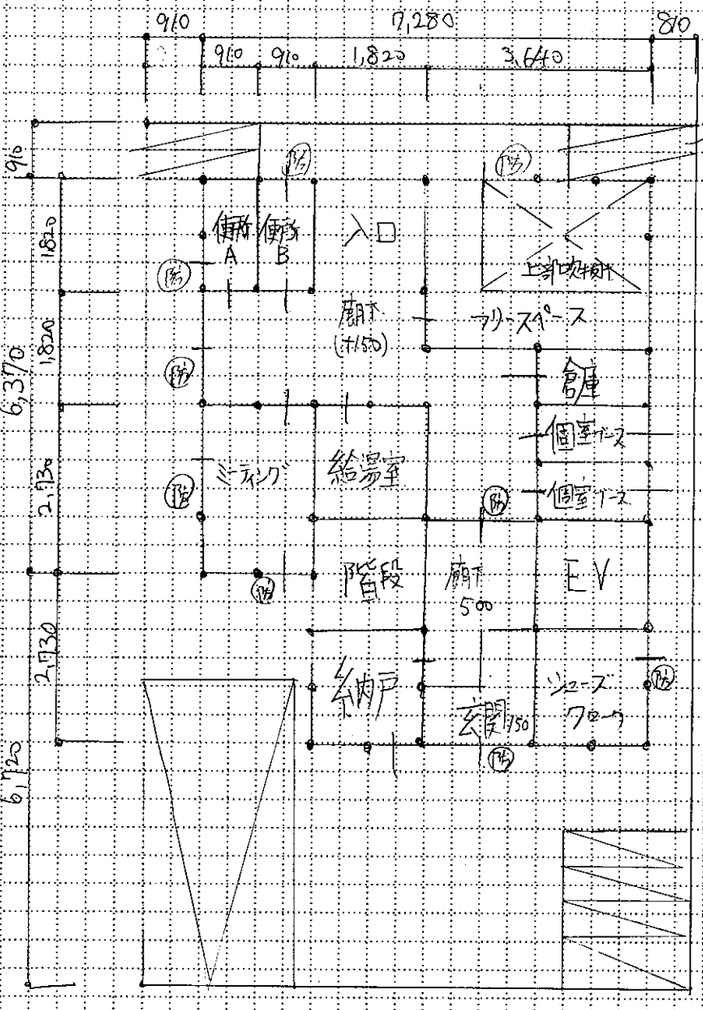

「２階平面プラン」を記入してください。（縮尺1／100）

（注）不正確な内容では、皆さんのプランを正しく評価できません。屋根、庇、室名、柱、開口部、寸法等を正確に記入してください。

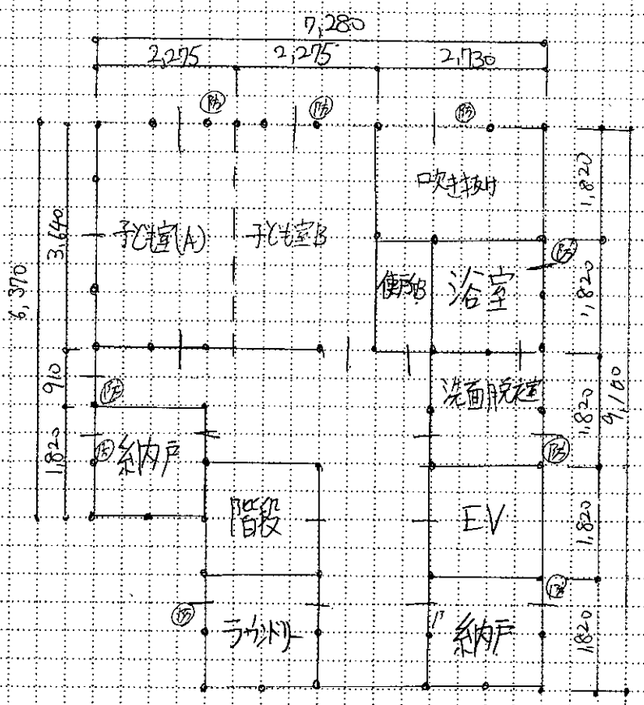


校名	池袋	学生番号	02800 − 0013 − 0231	受験番号	2F − 10472V	氏名	原田 義彬

２０２６年度 ２級建築士 プラン復元用紙 〔2/2〕（本試験プランを丁寧に記入しましょう。）

日建学院

「３階平面プラン」を記入してください。（縮尺1／100）

(注)不正確な内容では、皆さんのプランを正しく評価できません。屋根、庇、室名、柱、開口部、寸法等を正確に記入してください。

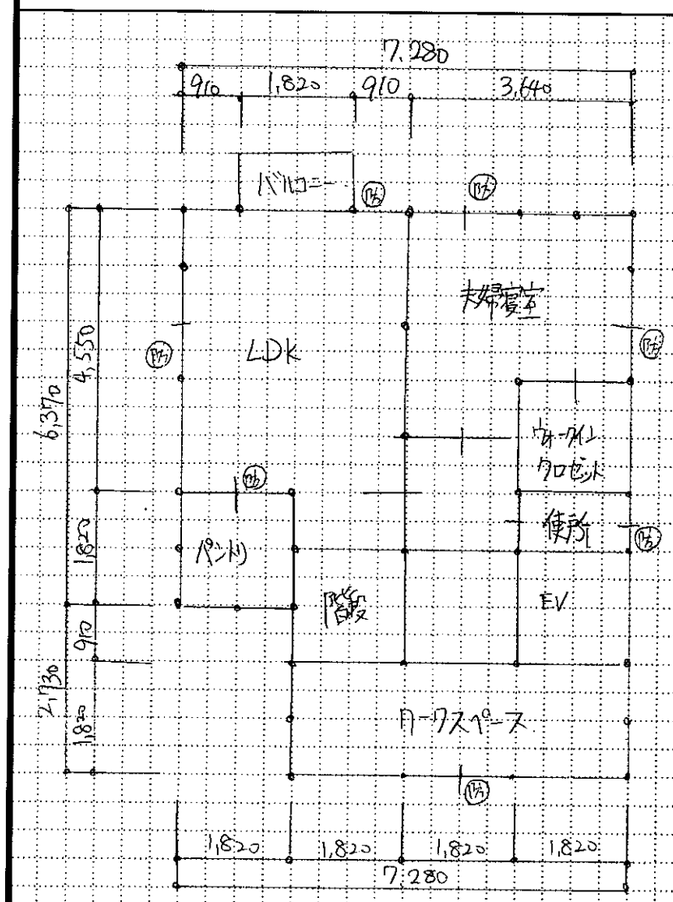

氏名 原田 義彬

「計画の要点等の回答」を記入してください。

設問①：

北側にユーキングスペースをまとめるとともに南側は敷地内にスペースを持つことで、プライバシーセキュリティに関して配慮した。

設問②：

子供室を隣接させて将来一つの部屋になった時でも吹抜けに部屋として開放感を感じられるようにした

設問③：壁材にガルバリウム金属材の利用

「面積表」を記入してください。（※印は出題された場合に記入してください）

敷地面積		126	㎡
建築面積	(計算式) 6.37m×7.28m+2.73m×5.46m	61.27	㎡
床面積 1階	(計算式) 〃	61.27	㎡
床面積 2階	(計算式) 〃 −1.82×2.73	56.31	㎡
床面積 3階	(計算式) 〃	61.27	㎡
延べ面積		178.86	㎡
※建蔽率	建築面積 ／ 敷地面積		%
※容積率	延べ面積 ／ 敷地面積		%

「作業時間・見直しの有無など」を記入してください。

プランニング	80 分	プラン完成後の見直し ☑した ☐していない
記述・面積表	15 分	作業に要した時間は普段と比べてどうでしたか？ ☐短い ☑同じ ☐長い
平面図	分	作業に要した時間は普段と比べてどうでしたか？ ☑短い ☐同じ ☐長い
立面図	分	作業に要した時間は普段と比べてどうでしたか？ ☑短い ☐同じ ☐長い
伏図	分	作業に要した時間は普段と比べてどうでしたか？ ☑短い ☐同じ ☐長い
部分詳細図	分	作業に要した時間は普段と比べてどうでしたか？ ☑短い ☐同じ ☐長い
見直し・仕上げ	5 分	答案完成後の見直し ☑した ☐していない

「本試験を受験して気になる事」を記入してください。（例：○○の意味が分からなかった。）

- 表入れ忘れ
- 部分詳細図にてレベル無視（3Fが150としたのに+500にしてしまった）
- 要点②が書きにくかった
- 要点③はよくわからなかった
- 西側の建築可能範囲を910mmとらなかった。
- 外壁面で表札等を入れ忘れた。

講師記入欄